


DOOR SCHEDULE

| TAG | TYPE                | SIZE W x H    | FROM → TO                       | LEAF OPENS                 |
|-----|---------------------|---------------|---------------------------------|----------------------------|
| D1  | DT-0 6'-0" DOUBLE   | 6'-0" x 7'-0" | Car porch landing ↔ Foyer       | both leaves out to landing |
| D2  | DT-1 3'-6"          | 3'-6" x 7'-0" | Passage 4'-0" Wide → Bed Room-2 | into Bed Room-2            |
| D4  | DT-2P 2'-6" POCKET  | 2'-6" x 7'-0" | Dress ↔ Bed Room-2              | slides into wall           |
| D3  | DT-3 2'-0"          | 2'-0" x 7'-0" | Dress → Bath                    | into Bath                  |
| D5  | DT-1 3'-6"          | 3'-6" x 7'-0" | Lawn → Passage 4'-0" Wide       | into Passage 4'-0" Wide    |
| D6  | DT-1 3'-6"          | 3'-6" x 7'-0" | Passage 4'-0" Wide → Kitchen    | into Kitchen               |
| D7  | DT-1 3'-6"          | 3'-6" x 7'-0" | Kitchen → Dirty Kitchen         | into Dirty Kitchen         |
| D8  | DT-1 3'-6"          | 3'-6" x 7'-0" | Guest Lobby → Drawing Room      | into Drawing Room          |
| D9  | DT-3 2'-0"          | 2'-0" x 7'-0" | Guest Lobby → Guest Washroom    | into Guest Washroom        |
| D10 | DT-2S 2'-6" SLIDING | 2'-6" x 7'-0" | Guest Lobby ↔ Guest Store       | slides on room face        |
| D11 | DT-1 3'-6"          | 3'-6" x 7'-0" | Bed-1 → Lounge                  | into Lounge                |
| D12 | DT-2S 2'-6" SLIDING | 2'-6" x 7'-0" | Bed-1 ↔ Dressing                | slides on room face        |
| D13 | DT-3 2'-0"          | 2'-0" x 7'-0" | Washroom → Dressing             | into Dressing              |


WINDOW & VENTILATOR SCHEDULE

| TAG | SIZE W x H        | SILL  | HEAD  | ROOM           | OPENS TO  | TYPE    |
|-----|-------------------|-------|-------|----------------|-----------|---------|
| W9  | 1'-6" x 6'-0"     | 1'-0" | 7'-0" | Lounge         | car porch | window  |
| W10 | 1'-6" x 6'-0"     | 1'-0" | 7'-0" | Guest Lobby    | car porch | window  |
| SL1 | 8'-0" x 7'-0"     | 0'-0" | 7'-0" | Bed Room-2     | open air  | sliding |
| W1  | 7'-0" x 4'-6"     | 2'-6" | 7'-0" | Bed Room-2     | open air  | window  |
| V1  | 2'-0" x 1'-0"     | 6'-0" | 7'-0" | Bath           | open air  | vent    |
| W2  | 5'-0" x 3'-6"     | 3'-6" | 7'-0" | Kitchen        | open air  | window  |
| V2  | 1'-6" x 1'-6"     | 5'-0" | 6'-6" | Dirty Kitchen  | OTS       | vent    |
| W3  | 7'-0" x 4'-6"     | 2'-6" | 7'-0" | Drawing Room   | open air  | window  |
| W4  | 5'-0" x 4'-0"     | 3'-0" | 7'-0" | Drawing Room   | open air  | window  |
| V4  | 2'-0" x 1'-0"     | 6'-0" | 7'-0" | Guest Washroom | open air  | vent    |
| W5  | 5'-6" x 4'-0"     | 3'-0" | 7'-0" | Bed-1          | open air  | window  |
| W6  | 3'-0" x 2'-0"     | 5'-0" | 7'-0" | Washroom       | open air  | vent    |
| W7  | 4'-6" x 4'-0"     | 3'-0" | 7'-0" | Lounge         | OTS       | window  |
| W8  | 3'-4 1/2" x 4'-0" | 3'-0" | 7'-0" | Lounge         | OTS       | window  |

DOOR TYPES

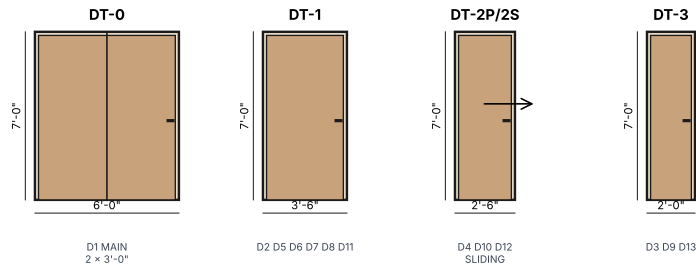

WINDOW & VENT TYPES (HEIGHTS FROM FFL)

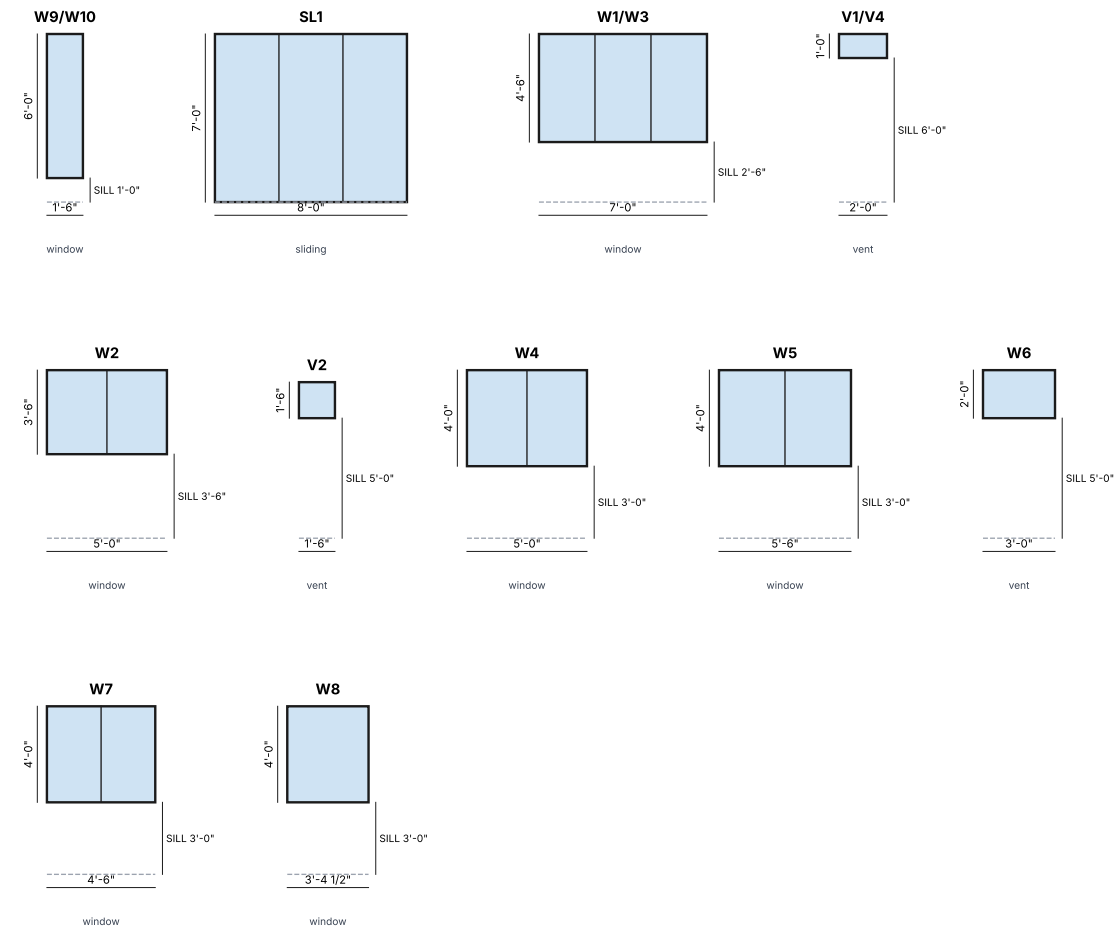

DAATA HAMLET RESIDENCE

Ground floor | Pakistan

|          |                                                                          |
|----------|--------------------------------------------------------------------------|
| PLOT     | 3,129.1 sq ft (290.7 m2)                                                 |
| MARLA    | 13.9 @ 225 sf   11.5 @ 272.25 sf                                         |
| LEVELS   | Datum +/-0 = road at P1 (highest)<br><br>Plot & lawn +/-0, GF FFL +0'-6" |
| FLOOR HT | 11'-0" floor to floor, 10'-6" clear                                      |
| UNITS    | Feet-inches; origin = peg P1                                             |
| REVISION | REV-04 05 OCT 2026                                                       |
| OPTION   | L-TYPE STAIR (OPTION 1)                                                  |

DOOR & WINDOW NOTES

- Door heights 7'-0". Frames 2"x5" seasoned wood.
- Main door D1: 6'-0" double teak (2 × 3'-0"), centred on the porch, opens out to the landing.
- Room doors 3'-6" solid-core flush; baths 2'-0" WPC (water-proof).
- Sliding 2'-6": D4 pocket in the 9" wall; D10 (store) and D12 (Bed-1 dressing) on top tracks. All wardrobes have sliding shutters.
- Lawn door D5 opens INWARD into the passage.
- Swing leaves hinge on the corner side and park flat against the adjoining wall.
- Windows: aluminium, 5mm tinted glass, MS safety grill inside. Vents: frosted louvres.
- W9 is a fixed glazed sidelight to the door.
- Sill / head heights are above the GF FFL.

SHEET TITLE

DOOR & WINDOW SCHEDULE + TYPES


SCALE

1/8" = 1'-0" (TYPES)

SHEET NO.


D-101

ENLARGED PLAN : L-TYPE STAIR (OPTION 1), LOBBY & ENTRANCE (1/4"=1'-0")

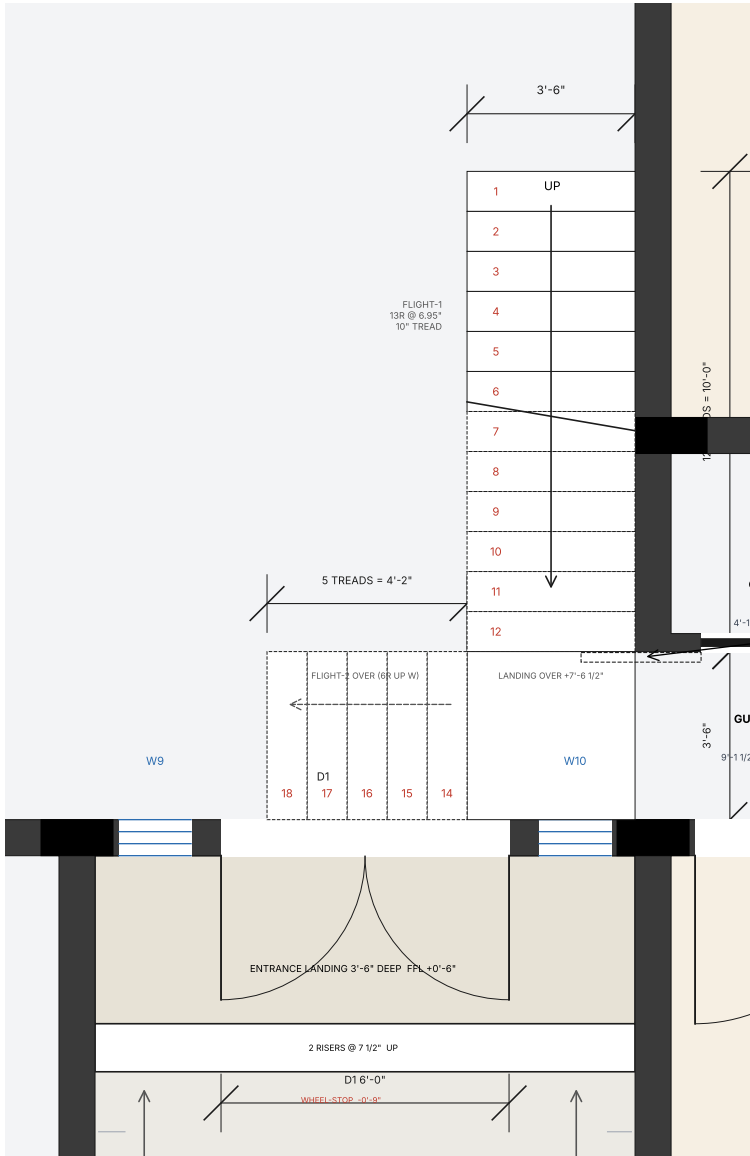


SECTION A-A : STAIR (L-TYPE) + GUEST LOBBY - LOOKING EAST

NORTH (LOUNGE) ← → SOUTH (ENTRANCE) | 19 RISERS @ 6.95" TREAD 10" WIDTH 3'-6"

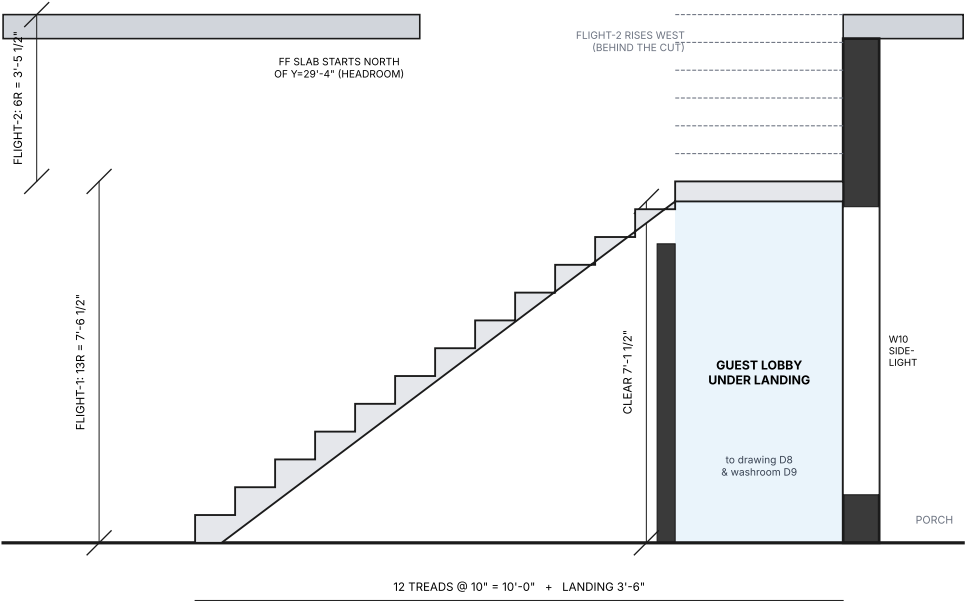

SECTION B-B : CAR PORCH RAMP & ENTRANCE

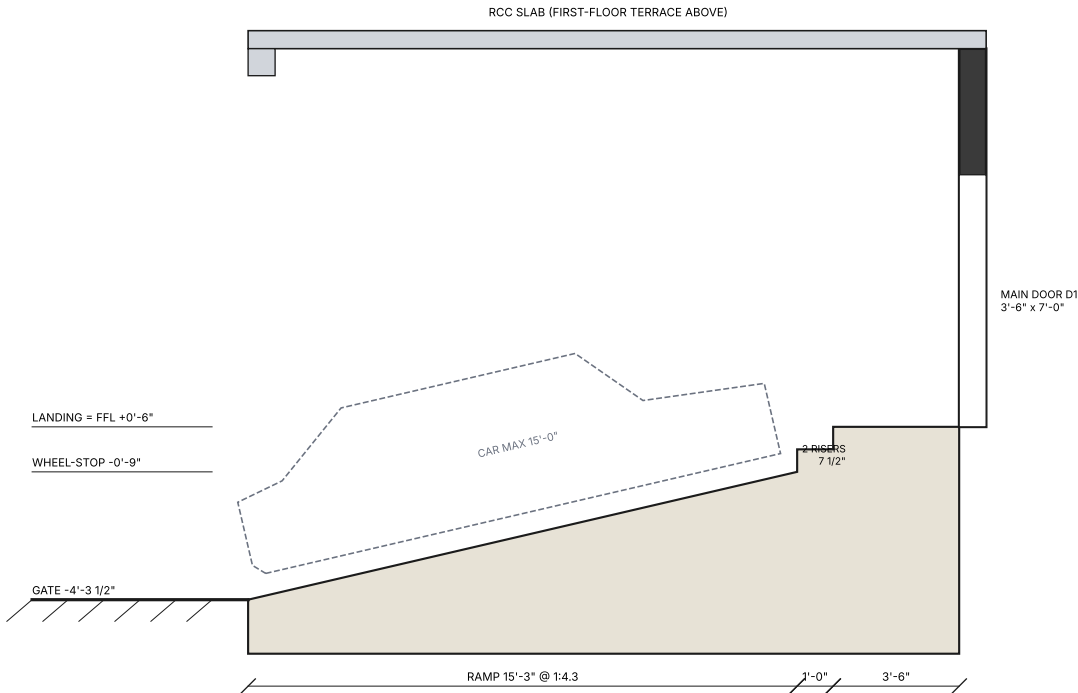

DAATA HAMLET  
RESIDENCE

Ground floor | Pakistan

|          |                                                                          |
|----------|--------------------------------------------------------------------------|
| PLOT     | 3,129.1 sq ft (290.7 m2)                                                 |
| MARLA    | 13.9 @ 225 sf   11.5 @ 272.25 sf                                         |
| LEVELS   | Datum +/-0 = road at P1 (highest)<br><br>Plot & lawn +/-0, GF FFL +0'-6" |
| FLOOR HT | 11'-0" floor to floor, 10'-6" clear                                      |
| UNITS    | Feet-inches; origin = peg P1                                             |
| REVISION | REV-04 05 OCT 2026                                                       |
| OPTION   | L-TYPE STAIR (OPTION 1)                                                  |

STAIR & ENTRANCE NOTES

1. Stair: RCC waist slab 5", treads 10" + 1" nosing, risers 6.95", width 3'-6".
2. Riser count: flight-1 = 13 (to landing +7'-6 1/2"), flight-2 = 6 (to FF +11'-0").
3. Under the landing (7'-1 1/2" clear) is the open guest lobby: foyer → drawing room (D8, 3'-6") and guest washroom (D9). No powder room.
4. Glass balustrade 3'-0" high on open sides.
5. Flight-2 runs west over the foyer; soffit 7'-1 1/2" rising to 10'-6".  
Main door head 7'-0" clears the soffit.
6. Porch ramp: broom-finished grooved RCC, drain channel with grating across the gate.
7. Wheel-stop (6" kerb) at the top of the ramp; max car length 15'-0".

SHEET TITLE

STAIR & ENTRANCE  
DETAILS

SCALE

PLAN & A-A 1/4"=1'-0"  
B-B 3/16"=1'-0"

SHEET NO.

D-102

DAATA HAMLET  
RESIDENCE

Ground floor | Pakistan

|          |                                                                          |
|----------|--------------------------------------------------------------------------|
| PLOT     | 3,129.1 sq ft (290.7 m2)                                                 |
| MARLA    | 13.9 @ 225 sf   11.5 @ 272.25 sf                                         |
| LEVELS   | Datum +/-0 = road at P1 (highest)<br><br>Plot & lawn +/-0, GF FFL +0'-6" |
| FLOOR HT | 11'-0" floor to floor, 10'-6" clear                                      |
| UNITS    | Feet-inches; origin = peg P1                                             |
| REVISION | REV-04 05 OCT 2026                                                       |
| OPTION   | L-TYPE STAIR (OPTION 1)                                                  |

- INTERIOR ELEVATIONS (TRUE VIEW)**
- B-B is what you see standing in the foyer facing the entrance (south): the drawing room & lobby are on your LEFT, the passage on your RIGHT.
  - C-C is the view from the foyer into the guest lobby (east): drawing room door on the right-hand wall, guest washroom ahead.
  - The lobby ceiling is the underside of the stair landing at 7'-1 1/2"; beyond the D-line beam it rises to 10'-6".
  - Doors: D1 6'-0" (2 x 3'-0"), D8 3'-6", D9 2'-0", D10 2'-6" sliding.

SHEET TITLE

INTERIOR ELEVATIONS  
ENTRANCE & LOBBY

SCALE


1/4" = 1'-0"

SHEET NO.

D-102B


INTERIOR ELEVATION B-B (L-STAIR) : FROM THE FOYER LOOKING SOUTH

TRUE VIEW - EAST (DRAWING / LOBBY) ON YOUR LEFT, WEST (PASSAGE) ON YOUR RIGHT

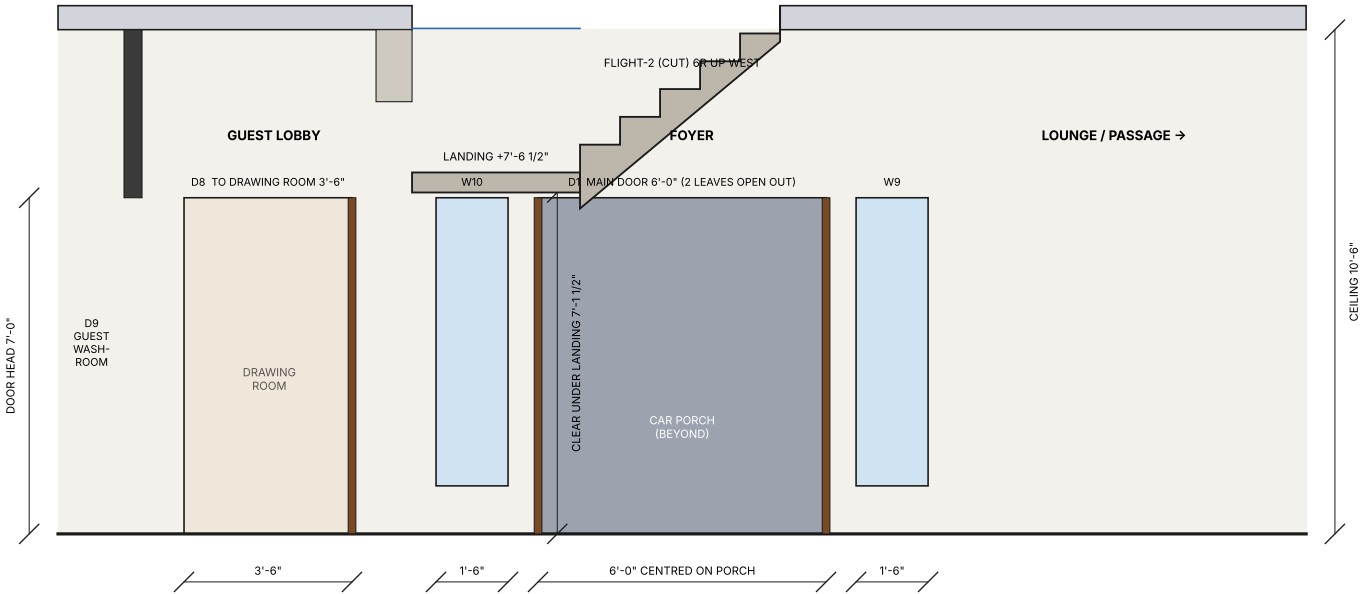

INTERIOR ELEVATION C-C (L-STAIR) : FROM THE FOYER LOOKING EAST INTO THE GUEST LOBBY

NORTH (LOUNGE) ON YOUR LEFT, SOUTH (ENTRANCE) ON YOUR RIGHT

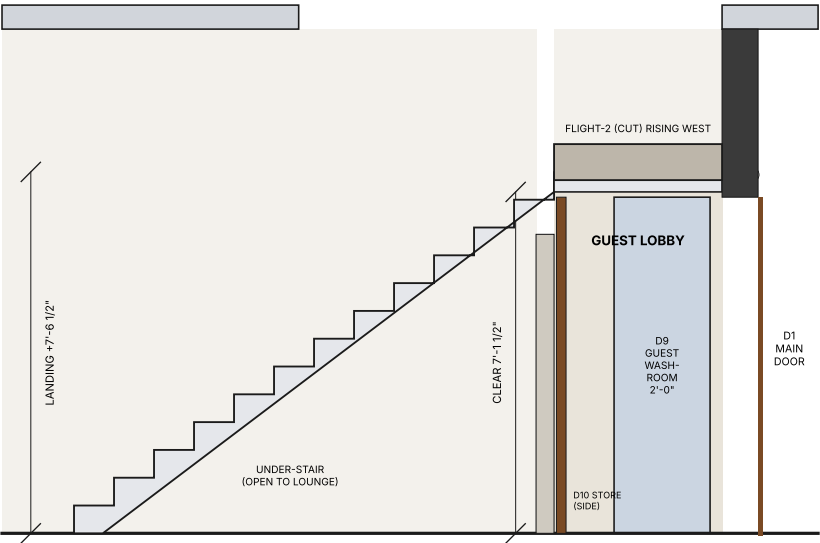

DAATA HAMLET  
RESIDENCE

Ground floor | Pakistan


|          |                                                                          |
|----------|--------------------------------------------------------------------------|
| PLOT     | 3,129.1 sq ft (290.7 m2)                                                 |
| MARLA    | 13.9 @ 225 sf   11.5 @ 272.25 sf                                         |
| LEVELS   | Datum +/-0 = road at P1 (highest)<br><br>Plot & lawn +/-0, GF FFL +0'-6" |
| FLOOR HT | 11'-0" floor to floor, 10'-6" clear                                      |
| UNITS    | Feet-inches; origin = peg P1                                             |
| REVISION | REV-04 05 OCT 2026                                                       |
| OPTION   | L-TYPE STAIR (OPTION 1)                                                  |

3D VIEWS

L-TYPE STAIR (OPTION 1)

Rendered from the 3D model built from the same dimensions as these drawings. Walls are cut at ceiling height so the stair, landing and the space beneath are fully visible.


FROM THE LOUNGE LOOKING SOUTH - stair, landing and the entrance beneath

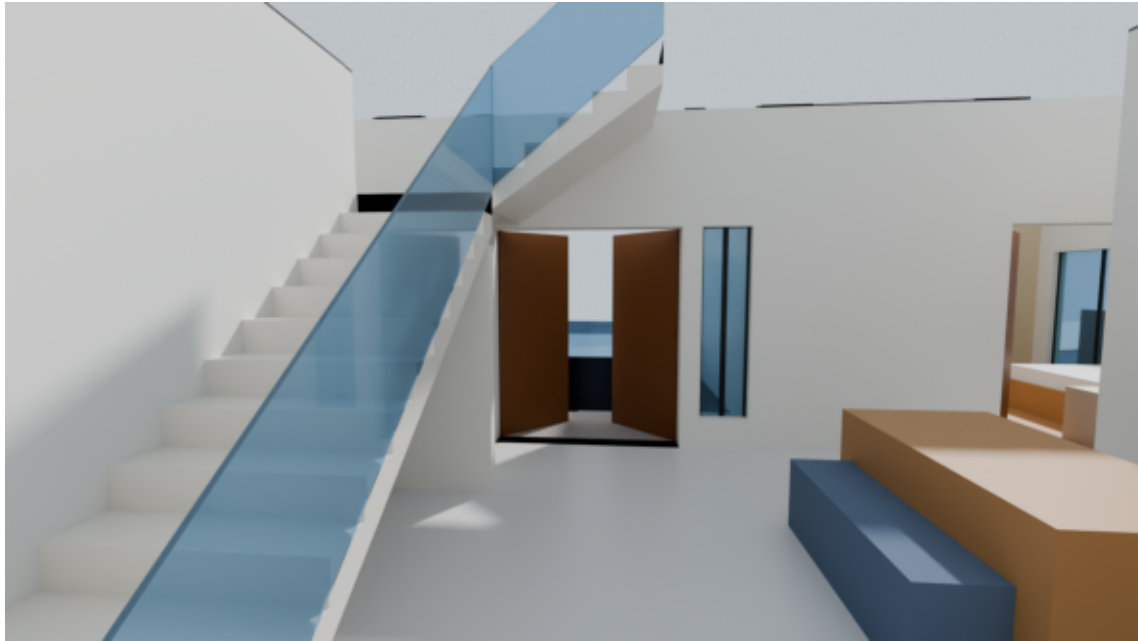


FROM THE FOYER LOOKING EAST - guest lobby under the landing, drawing door & washroom



FROM THE DINING AREA - stair profile and open space under the flights

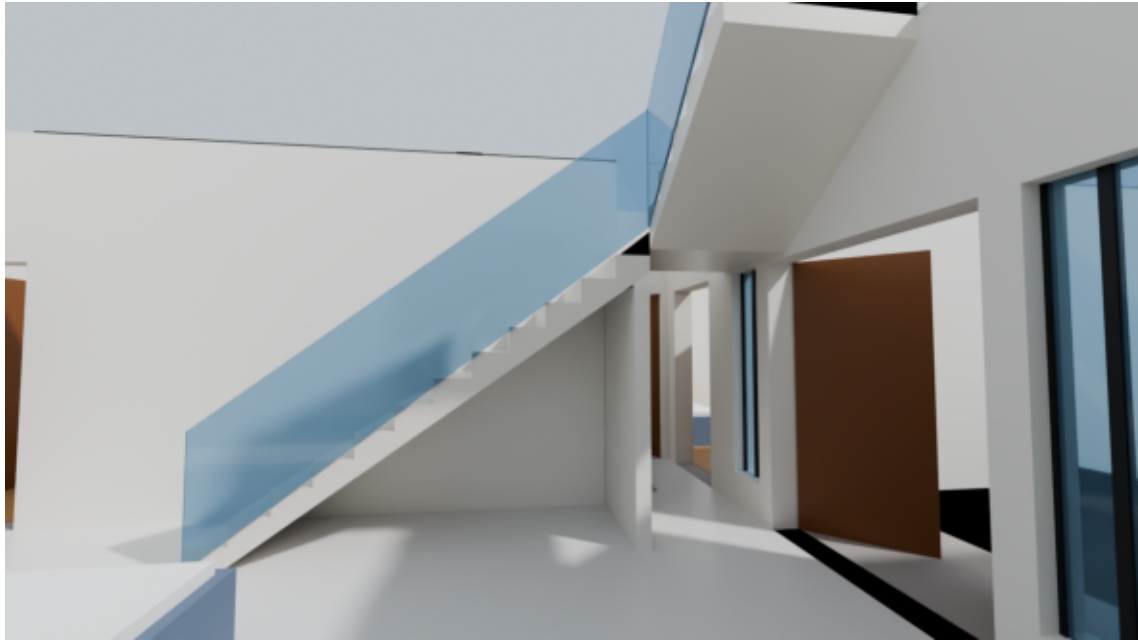

FROM THE CAR PORCH - 6'-0" main door centred, sidelights W9 / W10

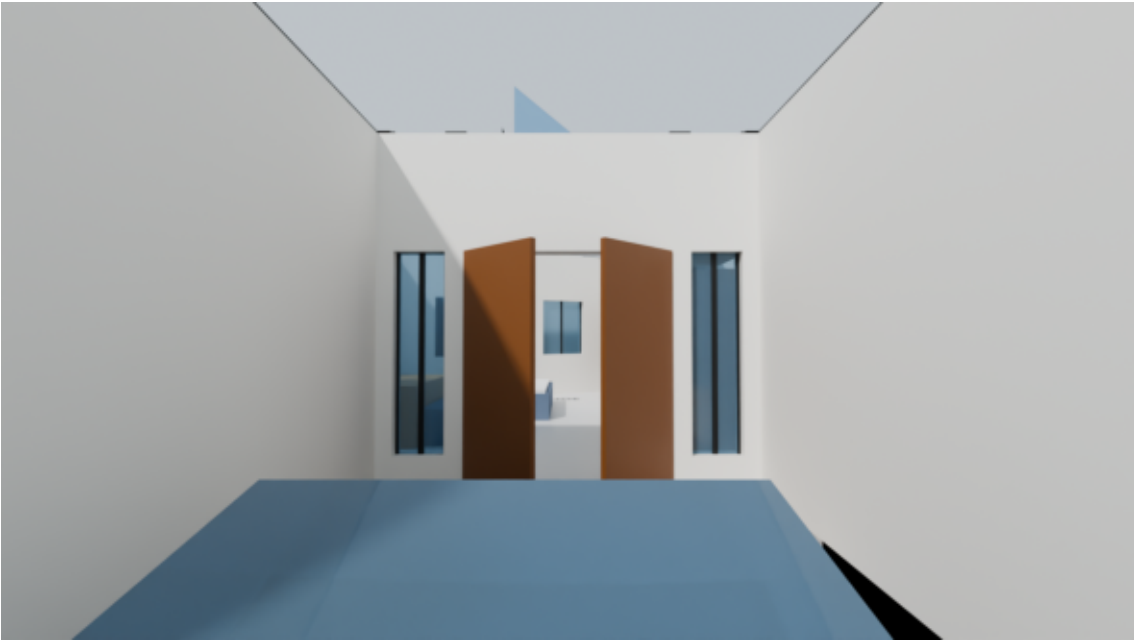

SHEET TITLE

3D VIEWS  
STAIR & ENTRANCE

SCALE

N.T.S.

SHEET NO.

D-105

DAATA HAMLET  
RESIDENCE


Ground floor | Pakistan

|          |                                                                          |
|----------|--------------------------------------------------------------------------|
| PLOT     | 3,129.1 sq ft (290.7 m2)                                                 |
| MARLA    | 13.9 @ 225 sf   11.5 @ 272.25 sf                                         |
| LEVELS   | Datum +/-0 = road at P1 (highest)<br><br>Plot & lawn +/-0, GF FFL +0'-6" |
| FLOOR HT | 11'-0" floor to floor, 10'-6" clear                                      |
| UNITS    | Feet-inches; origin = peg P1                                             |
| REVISION | REV-04 05 OCT 2026                                                       |
| OPTION   | L-TYPE STAIR (OPTION 1)                                                  |


OTS (OPEN-TO-SKY LIGHT WELL)

- Clear width 3'-0" measured square to the north boundary, between the 9" lounge wall and the 9" boundary wall.
- Length on lounge side 18'-7 1/2", on boundary side 18'-7".
- End widths (N-S): 3'-4 1/2" at grid C, 3'-4" at grid D. Area 58.4 sq ft.
- Floor: 4" gravel over brick-on-edge with a 4" floor drain; lounge glazing W7 & W8.
- Dirty kitchen vent V2 opens into the OTS.
- Kept open through every floor up to the roof.

SECTION C-C : OTS (LIGHT WELL)

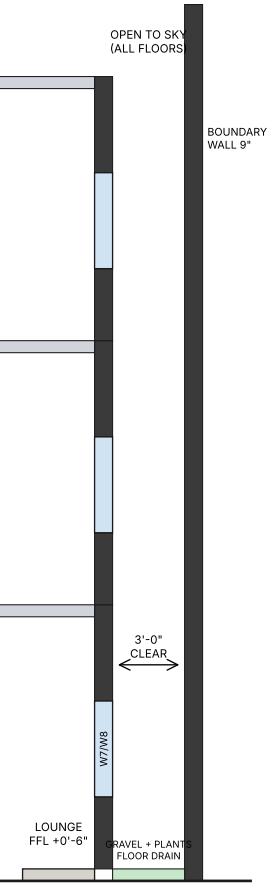

ENLARGED PLAN : OTS (3/8"=1'-0")

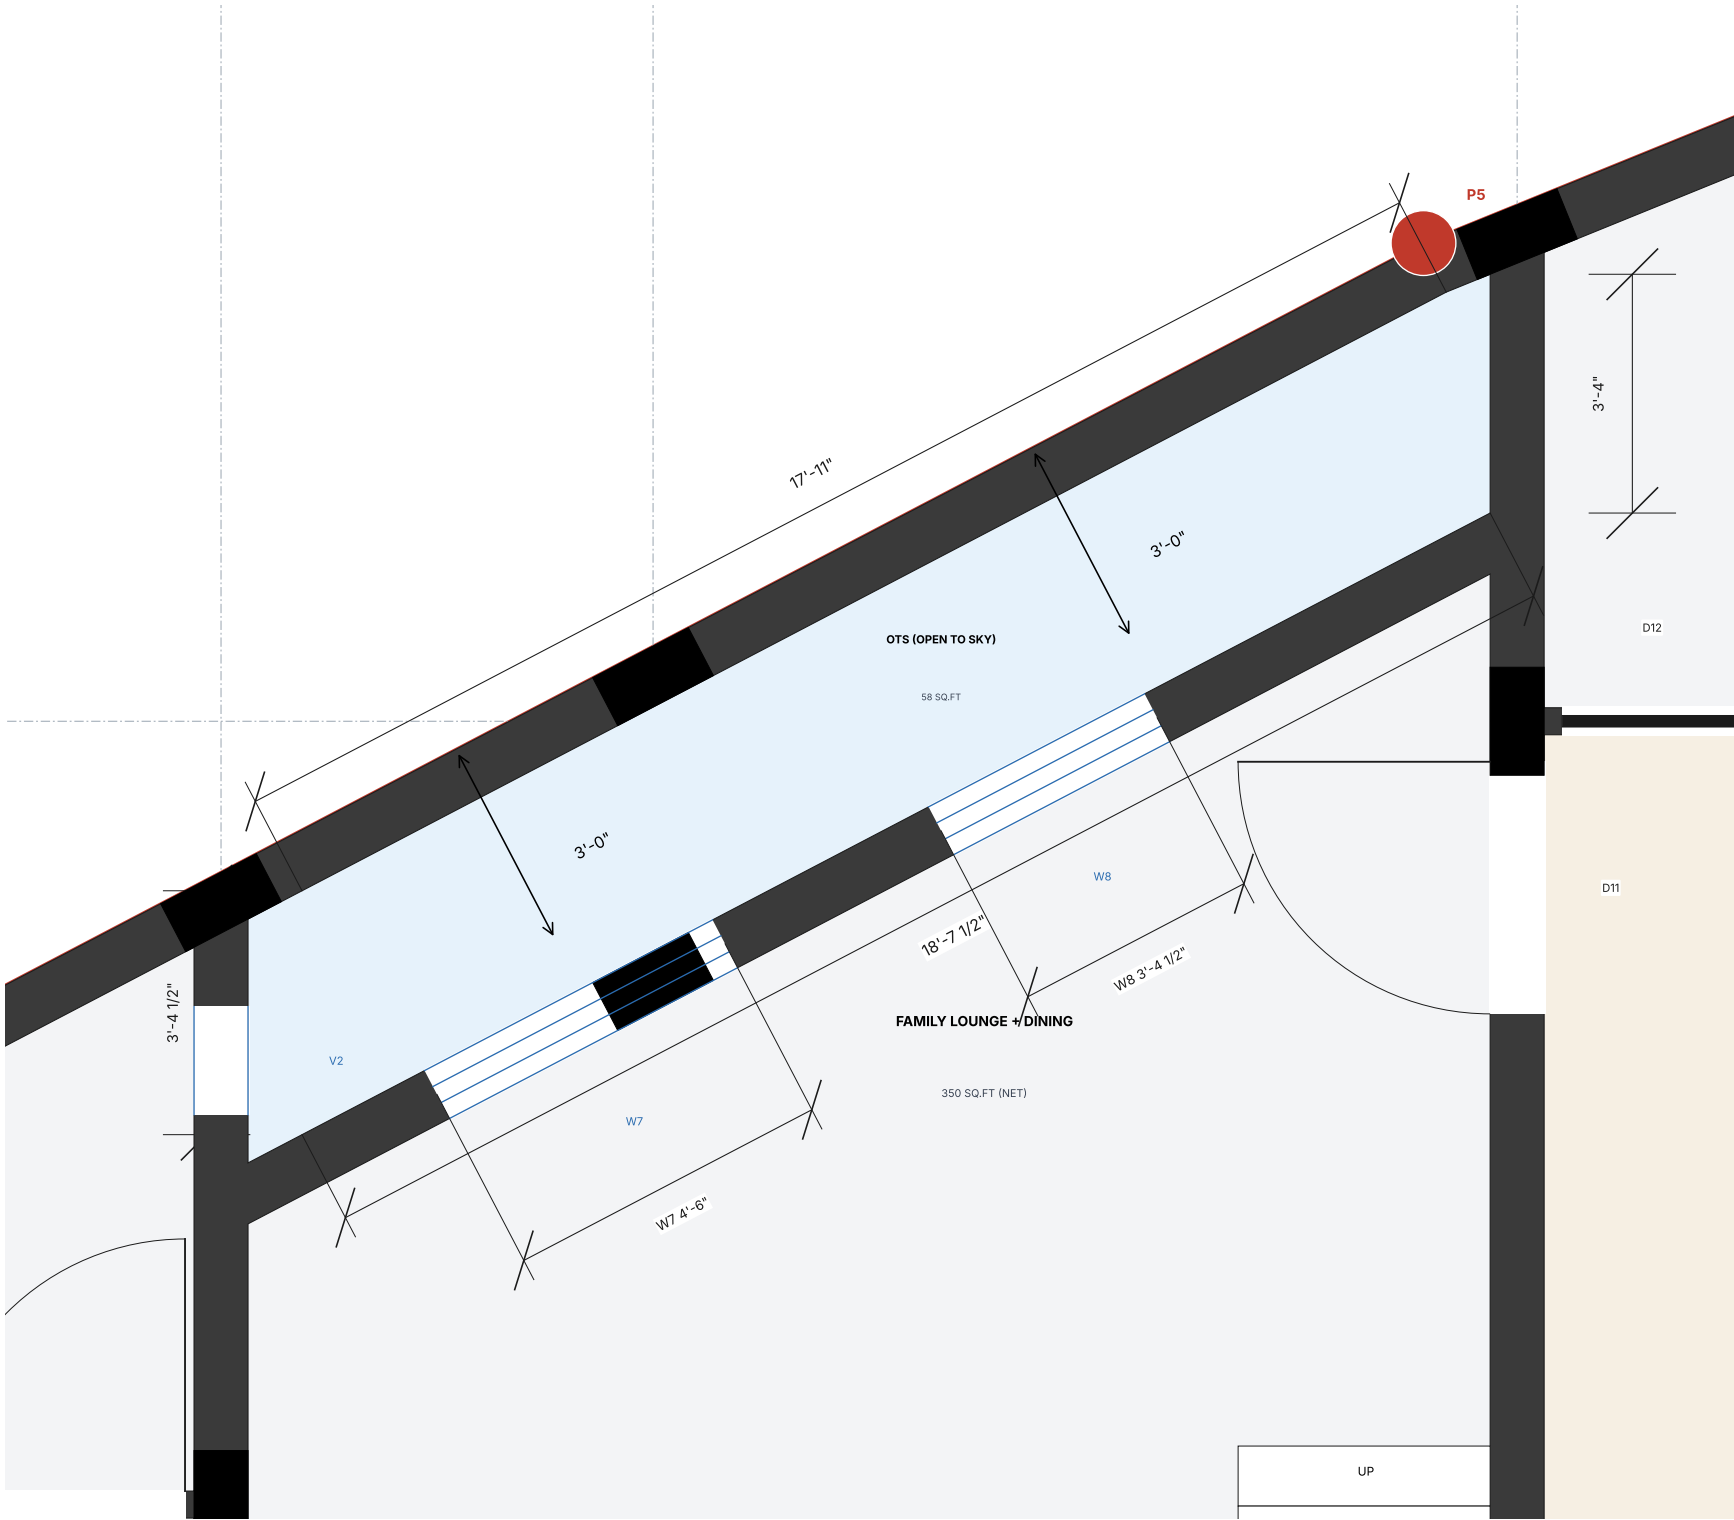

SHEET TITLE

OTS DETAIL  
(PLAN + SECTION)

SCALE

PLAN 3/8"=1'-0"  
SECTION 1/8"=1'-0"

SHEET NO.

D-103

ROOM SCHEDULE - GROUND FLOOR

| SPACE                                  | CLEAR SIZE            | SQ.FT  | FLOOR  |
|----------------------------------------|-----------------------|--------|--------|
| DRAWING ROOM                           | 15'-0" x 16'-0"       | 240.0  | WOOD   |
| BED ROOM-2                             | 13'-9" x 16'-0"       | 220.0  | WOOD   |
| DRESS (BED-2)                          | 5'-3" x 8'-7 1/2"     | 45.3   | TILE   |
| BATH (BED-2)                           | 5'-3" x 7'-0"         | 36.8   | WET    |
| LOUNGE + DINING                        | irregular             | 350.3  | TILE   |
| KITCHEN                                | 13'-9" x 8'-1 1/2"    | 111.7  | WET    |
| DIRTY KITCHEN                          | 13'-5" x 7'-6 1/2"    | 53.0   | WET    |
| PASSAGE 4'-0" WIDE                     | 14'-6" x 4'-0"        | 58.0   | TILE   |
| GUEST LOBBY                            | 9'-1 1/2" x 3'-6"     | 31.9   | TILE   |
| GUEST STORE                            | 4'-10 1/2" x 3'-9"    | 18.3   | TILE   |
| GUEST WASHROOM                         | 9'-9" x 7'-7 1/2"     | 74.3   | WET    |
| BED-1                                  | 15'-0" x 15'-0"       | 225.0  | WOOD   |
| DRESSING (BED-1)                       | 7'-1 1/2" x 9'-2 1/2" | 55.4   | TILE   |
| WASHROOM (BED-1)                       | 7'-6" x 12'-5"        | 81.7   | WET    |
| CAR PORCH                              | 11'-3" x 19'-9"       | 222.2  | PAVER  |
| OTS (OPEN TO SKY)                      | irregular             | 58.4   | GRAVEL |
| TOTAL NET CARPET AREA                  |                       | 1601.8 |        |
| TOTAL COVERED AREA (WITH WALLS, PORCH) |                       | 2078.4 |        |
| GROUND COVERAGE                        |                       | 66.4 % |        |
| MAIN LAWN                              |                       | 651.5  | GRASS  |

COLUMN SCHEDULE

| MARK | GRID / LOCATION             | SIZE     | 18" ALONG | CENTRE X,Y (FT) |
|------|-----------------------------|----------|-----------|-----------------|
| C1   | B / 1                       | 9" x 18" | E-W       | (36.88, 3.38)   |
| C2   | C / 1                       | 9" x 18" | E-W       | (51.00, 3.38)   |
| C3   | C' / 1                      | 9" x 18" | N-S       | (57.00, 3.75)   |
| C4   | D / 1                       | 9" x 18" | N-S       | (69.00, 3.75)   |
| C5   | E / 1                       | 9" x 18" | E-W       | (84.38, 3.38)   |
| C6   | B / 2                       | 9" x 18" | E-W       | (36.88, 20.12)  |
| C7   | C / 2                       | 9" x 18" | E-W       | (51.00, 20.12)  |
| C8   | C' / 2                      | 9" x 18" | E-W       | (57.00, 20.12)  |
| C9   | D / 2                       | 9" x 18" | E-W       | (69.00, 20.12)  |
| C10  | E / 2                       | 9" x 18" | E-W       | (84.38, 20.12)  |
| C11  | D / 3                       | 9" x 18" | E-W       | (69.38, 28.50)  |
| C12  | D / 5                       | 9" x 18" | N-S       | (69.00, 44.06)  |
| C13  | E / 3                       | 9" x 18" | E-W       | (84.38, 28.50)  |
| C14  | E / 5                       | 9" x 18" | N-S       | (84.75, 44.06)  |
| C15  | B / 4                       | 9" x 18" | N-S       | (36.50, 32.81)  |
| C16  | C / 4                       | 9" x 18" | N-S       | (51.00, 33.19)  |
| C17  | C / boundary wall           | 9" x 18" | E-W       | (51.00, 41.54)  |
| C18  | C' / 5                      | 9" x 18" | E-W       | (57.00, 44.68)  |
| C19  | D / boundary wall           | 9" x 18" | E-W       | (69.00, 50.82)  |
| C20  | E / boundary wall           | 9" x 18" | E-W       | (84.29, 57.04)  |
| C21  | C' / boundary wall          | 9" x 18" | E-W       | (57.00, 40.45)  |
| C22  | B+4'-9 1/2" / boundary wall | 9" x 18" | E-W       | (41.29, 36.49)  |

DAATA HAMLET  
RESIDENCE

Ground floor | Pakistan

|          |                                                                          |
|----------|--------------------------------------------------------------------------|
| PLOT     | 3,129.1 sq ft (290.7 m2)                                                 |
| MARLA    | 13.9 @ 225 sf   11.5 @ 272.25 sf                                         |
| LEVELS   | Datum +/-0 = road at P1 (highest)<br><br>Plot & lawn +/-0, GF FFL +0'-6" |
| FLOOR HT | 11'-0" floor to floor, 10'-6" clear                                      |
| UNITS    | Feet-inches; origin = peg P1                                             |
| REVISION | REV-04 05 OCT 2026                                                       |
| OPTION   | L-TYPE STAIR (OPTION 1)                                                  |

FINISH KEY

- WOOD = engineered wood / laminate
- TILE = 24"x24" porcelain
- WET = anti-skid ceramic + waterproofing
- PAVER = grooved RCC / exterior pavers

CEILINGS

- 10'-6" clear unless noted. Powder west
- half 7'-1 1/2" (under stair landing).

SHEET TITLE

ROOM & COLUMN  
SCHEDULES

SCALE

N.T.S.

SHEET NO.

D-104