

DAATA HAMLET
RESIDENCE

Ground floor | Pakistan

PLOT	3,129.1 sq ft (290.7 m2)
MARLA	13.9 @ 225 sf 11.5 @ 272.25 sf
LEVELS	Datum +/-0 = road at P1 (highest) Plot & lawn +/-0, GF FFL +0'-6"
FLOOR HT	11'-0" floor to floor, 10'-6" clear
UNITS	Feet-inches; origin = peg P1
REVISION	REV-04 05 OCT 2026
OPTION	COMPACT U-STAIR (OPTION 2)

GENERAL NOTES

- Dimensions in feet-inches; follow written dimensions, do not scale the drawing.
- Walls: 9" external & structural, 4.5" partitions.

No wall thicker than 9".
- RCC columns 9" x 18" (22 nos), always inside the 9" wall line. Sizes, steel & footings by structural engineer.
- No construction west of Line B (X=36'-1 1/2").
- Front setback 3'-0". East service passage 2'-9 1/2" at road, 3'-7" at rear.
- All baths & kitchens vent directly to open air (road side, porch, OTS or passage).
- Doors: main 6'-0" double, rooms 3'-6", dressings 2'-6" sliding, baths 2'-0". Swing leaves hinge on the corner side.
- Setbacks & coverage to be verified against the approving authority bylaws before submission.

LEGEND

- black = RCC column 9"x18", grey = wall
blue triple line = window, double = vent
dashed treads = stair above 4'-0" cut
D / W / V / SL = door, window, vent, slider
(sizes on details sheet D-101)

SHEET TITLE

GROUND FLOOR PLAN
(DIMENSIONED, FURNISHED)

SCALE

1/8" = 1'-0" (1:96)

SHEET NO.

A-101

GROUND FLOOR PLAN

GF FFL +0'-6" | PLOT & LAWN +/-0'-0" = ROAD AT P1 (HIGHEST) | CLEAR CEILING 10'-6" | FLOOR-TO-FLOOR 11'-0"



DAATA HAMLET
RESIDENCE

Ground floor | Pakistan

PLOT	3,129.1 sq ft (290.7 m2)
MARLA	13.9 @ 225 sf 11.5 @ 272.25 sf
LEVELS	Datum +/-0 = road at P1 (highest) Plot & lawn +/-0, GF FFL +0'-6"
FLOOR HT	11'-0" floor to floor, 10'-6" clear
UNITS	Feet-inches; origin = peg P1
REVISION	REV-04 05 OCT 2026
OPTION	COMPACT U-STAIR (OPTION 2)

STRUCTURE NOTES

- Grid lines are wall centre lines; columns stand ONLY on grid intersections (plus the P4 bend of the boundary).
- Every building corner and every junction of 9" structural walls has a column; 4.5" partitions carry no columns.
- Max beam span about 16'-0" (D-E bay 15'-9").
- Columns 9" x 18" sit fully inside the 9" walls - nothing projects into rooms/facade.
- Columns continue to roof (3 storeys).
- Footings, reinforcement, beam depths and slabs by structural engineer.
- Plot is filled up to 6'-0" on the east: footings to bear on natural ground, not on fill; retaining wall designed by engineer.

SHEET TITLE


COLUMN & WALL
LAYOUT

SCALE

1/8" = 1'-0" (1:96)

SHEET NO.

A-102

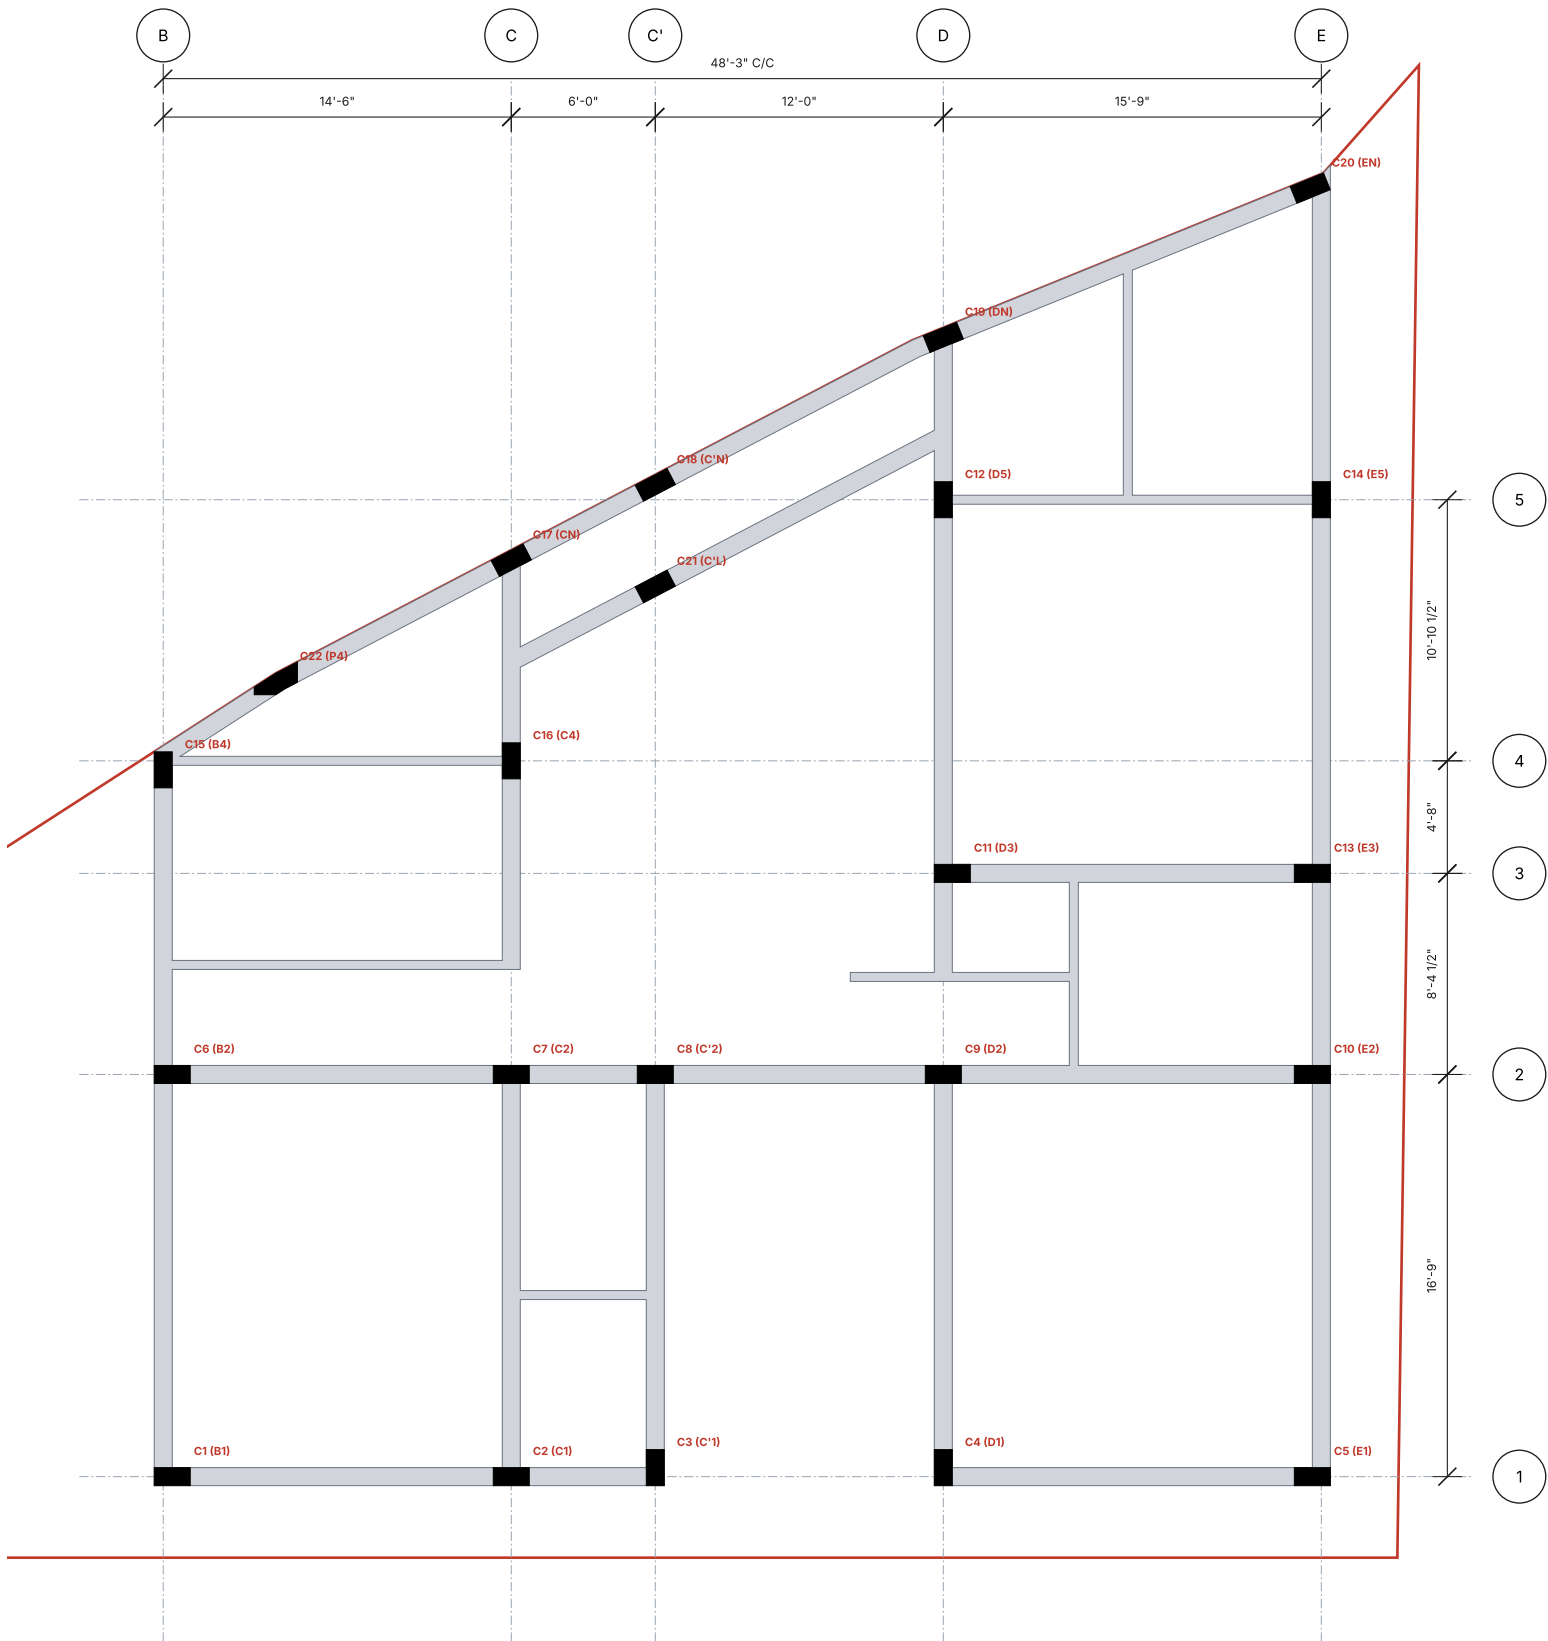

22 RCC COLUMNS 9"x18", LONG SIDE ALONG THE WALL - NONE PROJECTS BEYOND THE 9" WALL FACE

DAATA HAMLET
RESIDENCE

Ground floor | Pakistan

PLOT	3,129.1 sq ft (290.7 m2)
MARLA	13.9 @ 225 sf 11.5 @ 272.25 sf
LEVELS	Datum +/-0 = road at P1 (highest) Plot & lawn +/-0, GF FFL +0'-6"
FLOOR HT	11'-0" floor to floor, 10'-6" clear
UNITS	Feet-inches; origin = peg P1
REVISION	REV-04 05 OCT 2026
OPTION	COMPACT U-STAIR (OPTION 2)


FACADE & SITE

- Road falls 6'-0" from P1 to P0. Plot & lawn level with the road at P1; nothing below road.
- Stone retaining wall along the front, 0 to 6'-0", with a 3'-6" MS railing on the plot edge.
- Car porch: ramp ~1:4.3 (grooved concrete) from the gate to a wheel-stop, 2 risers of 7 1/2", then a 3'-6" landing at FFL.
- Main door 6'-0" double, centred on the porch, between matching sidelights W9 / W10. Guests reach the drawing room & guest washroom through the lobby under the landing.
- W1 & W3: 7'-0" x 4'-6", centred on rooms, sill 2'-6", 1'-6" RCC chajja over.
- V1: 2'-0" x 1'-0" frosted vent at +6'-0".

STAIR (SECTION A-A) - COMPACT U-STAIR (OPTION 2)


- 3'-6" wide, 19 risers of 6.95", treads 10".
- Flight-1: 13 risers to landing +7'-6 1/2" (landing sits over the guest lobby).
- Flight-2: 6 risers, 3'-5 1/2" to first floor, returning north beside flight-1.
- Clear height under landing 7'-1 1/2".

SOUTH (ROAD-SIDE) ELEVATION - GROUND FLOOR

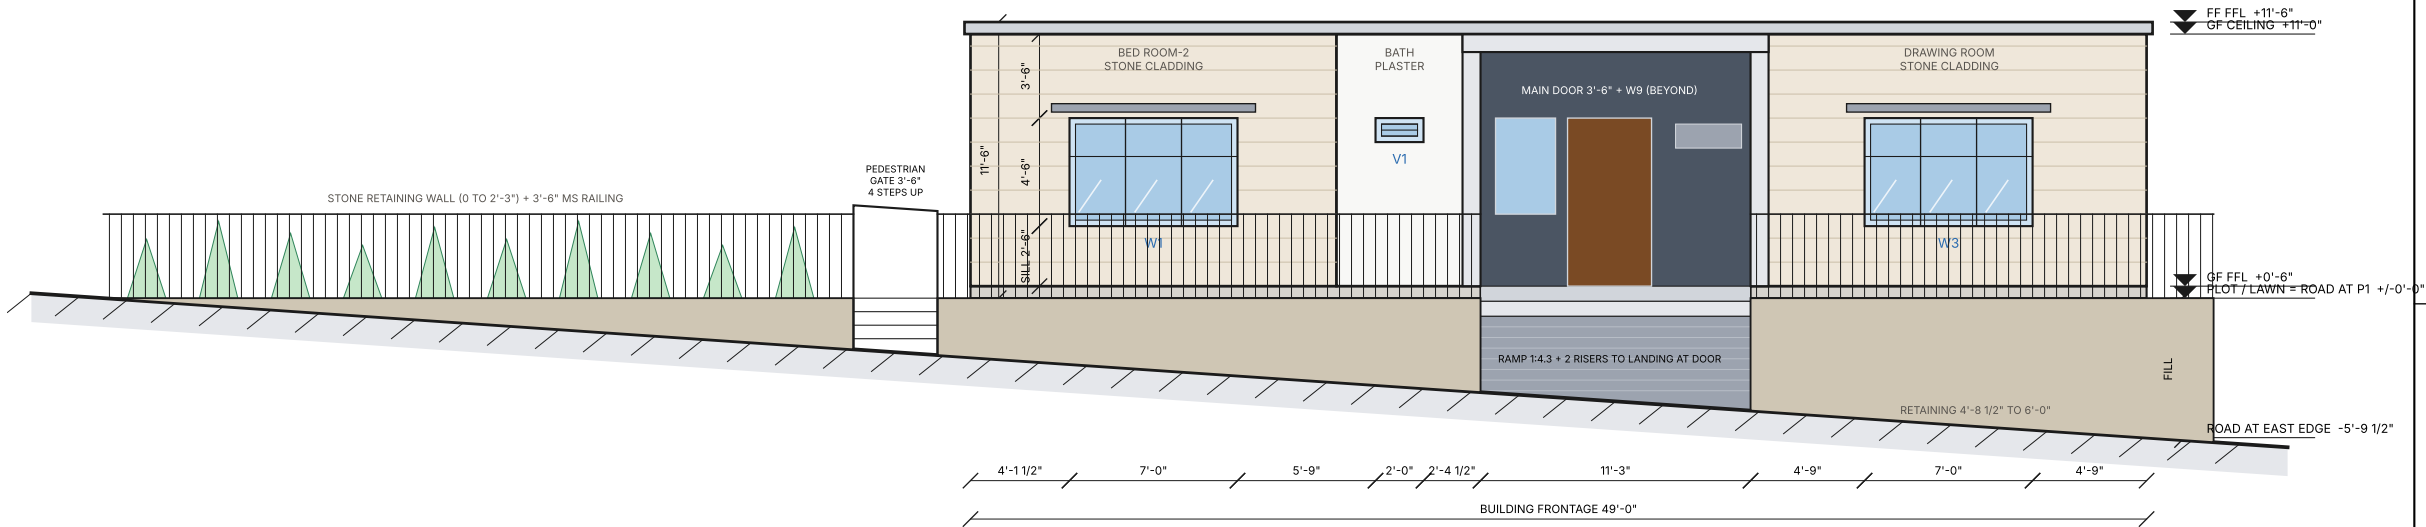

SECTION A-A : STAIR (U-TYPE) + GUEST LOBBY - LOOKING EAST

NORTH (LOUNGE) ← → SOUTH (ENTRANCE) | 19 RISERS @ 6.95" TREAD 10" WIDTH 3'-6"

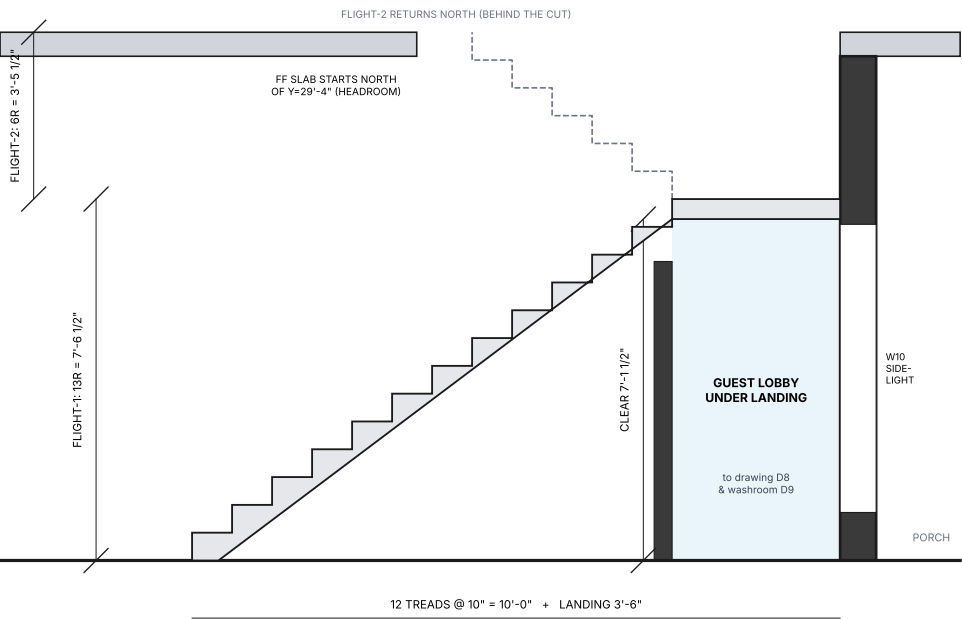

SHEET TITLE

SOUTH ELEVATION
+ SECTION A-A

SCALE

ELEV 1/8"=1'-0"
SECTION 1/4"=1'-0"

SHEET NO.

A-103