



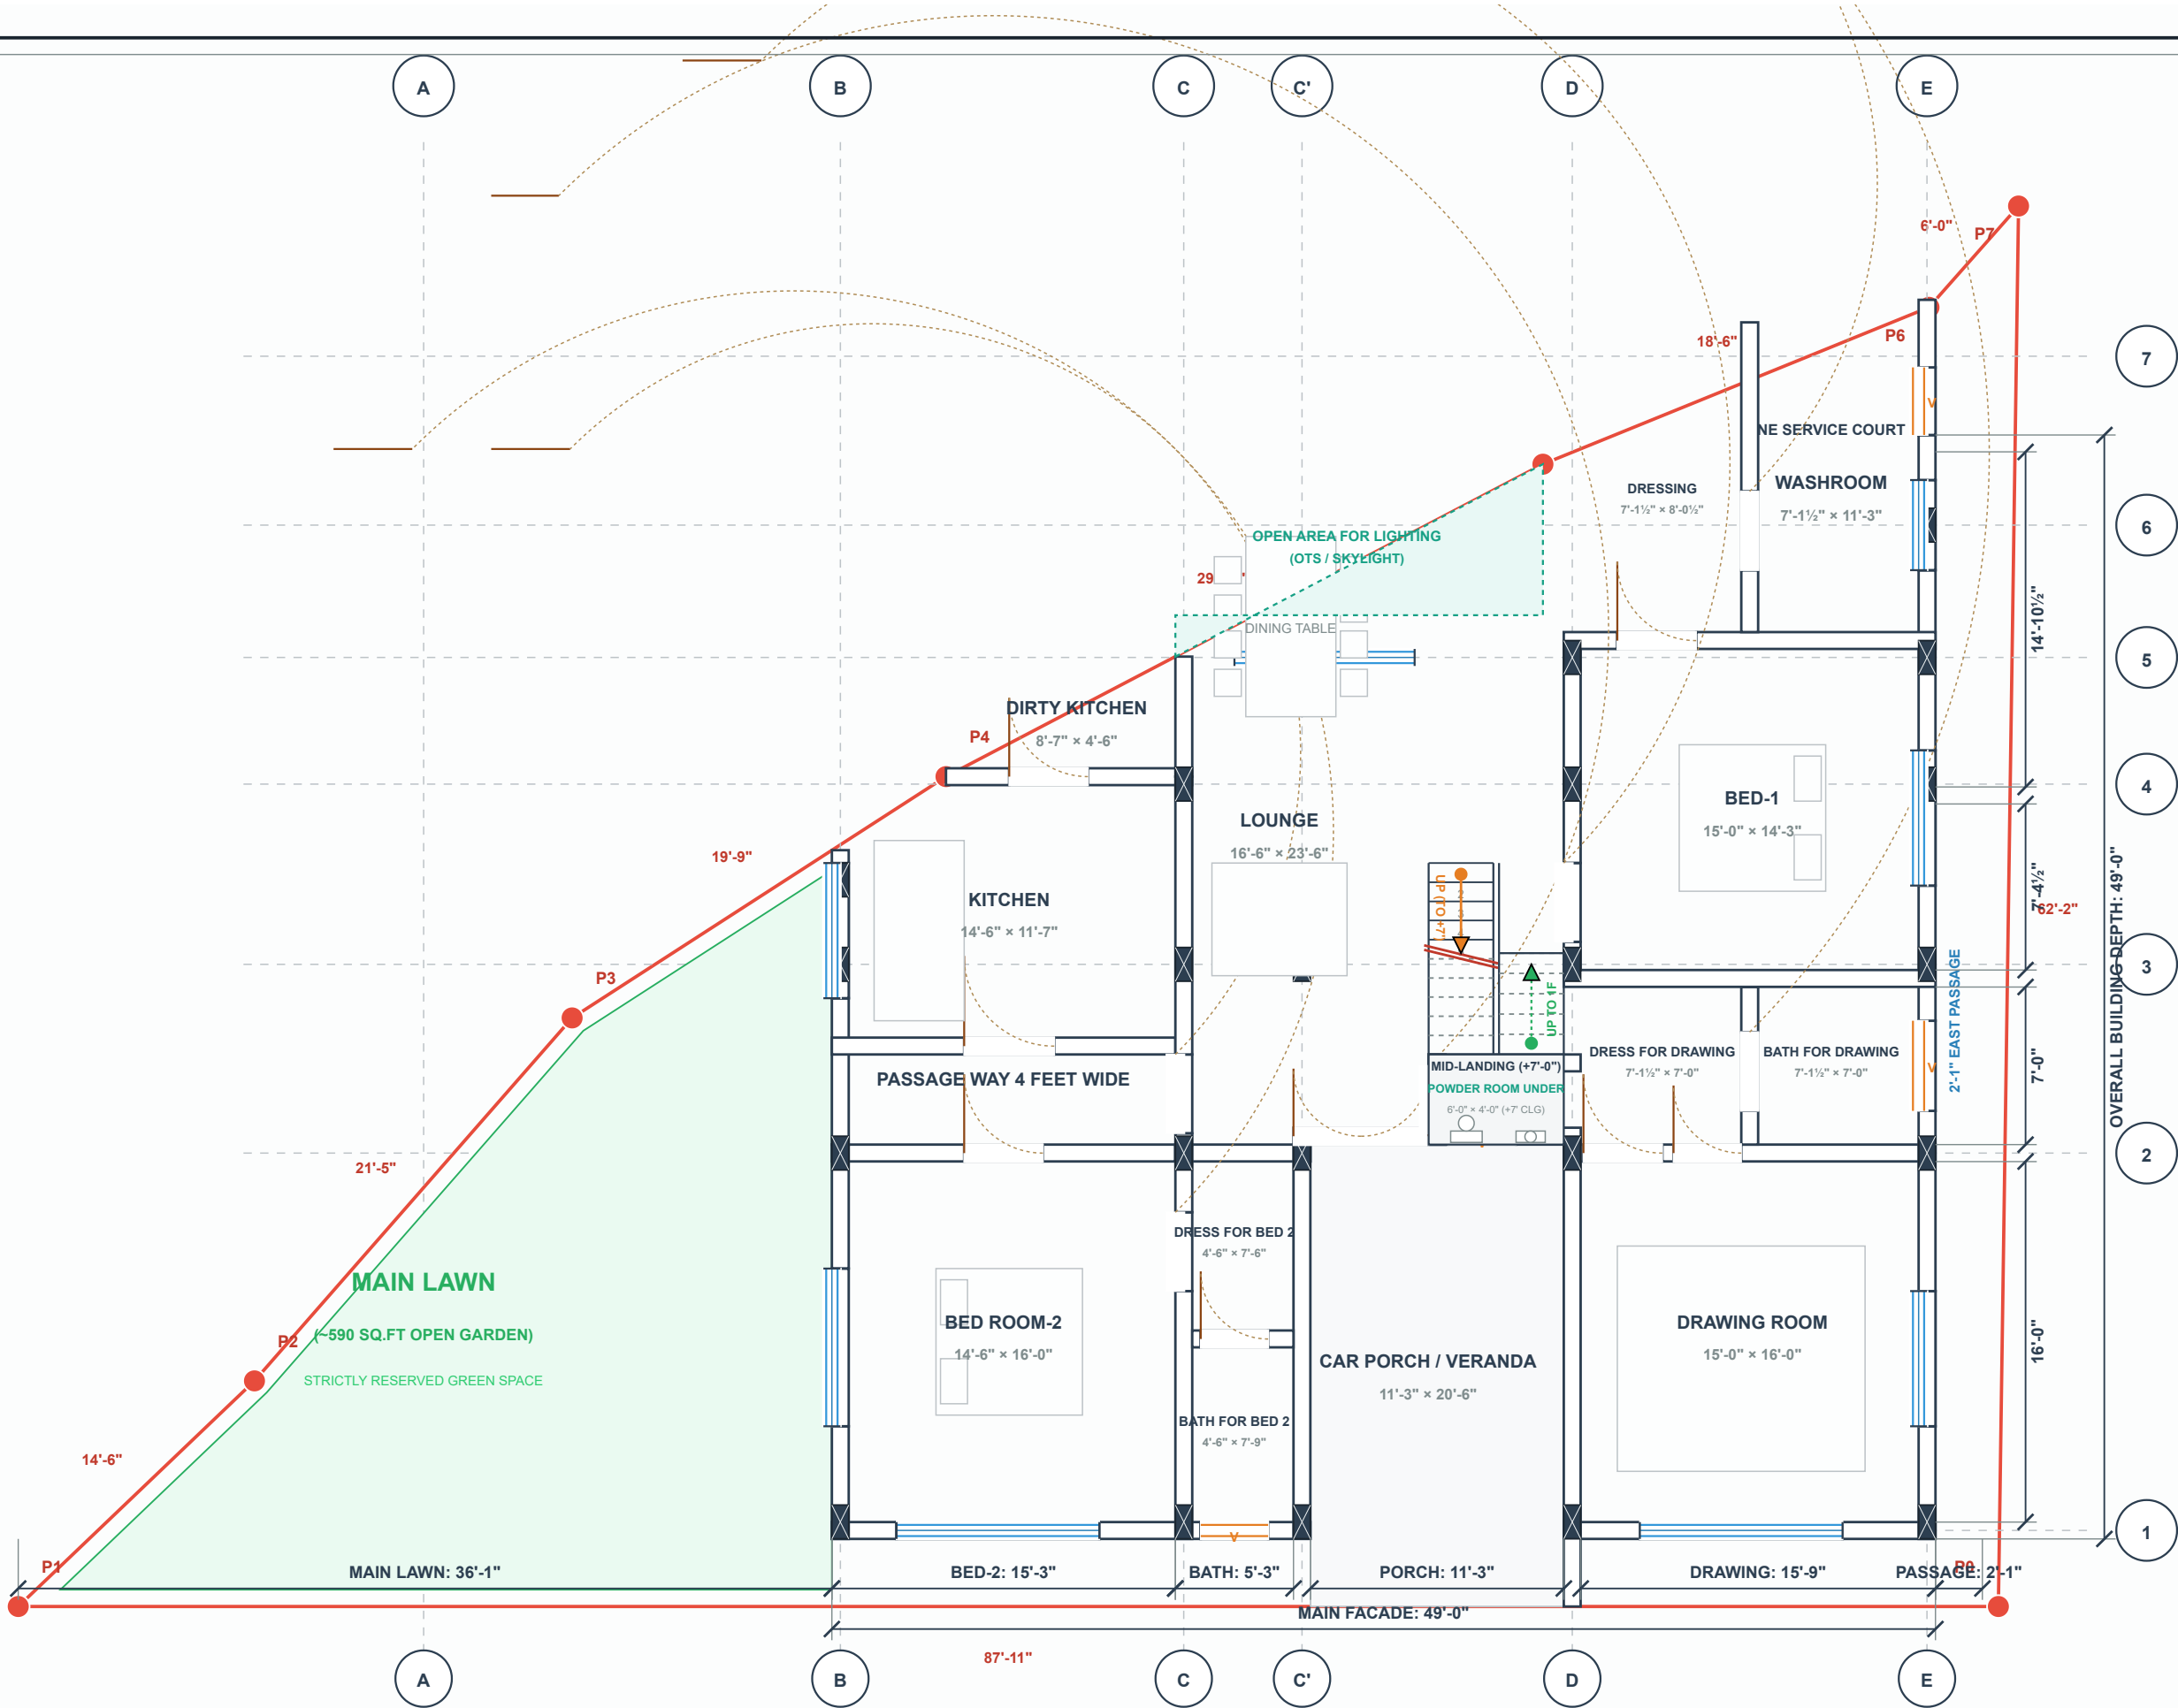


|                                                |  |                      |  |
|------------------------------------------------|--|----------------------|--|
| DAATA HAMLET RESIDENCE                         |  | PLOT: 3,129.1 SQ.FT. |  |
| DRAWING: GROUND FLOOR ARCHITECTURAL PLAN       |  | SHEET: A-101         |  |
| SCALE: 1/8" = 1'-0"   STATUS: APPROVED FOR CAD |  | UNITS: FEET-INCHES   |  |


PUBLIC ACCESS ROAD (87'-11" FRONTAGE)

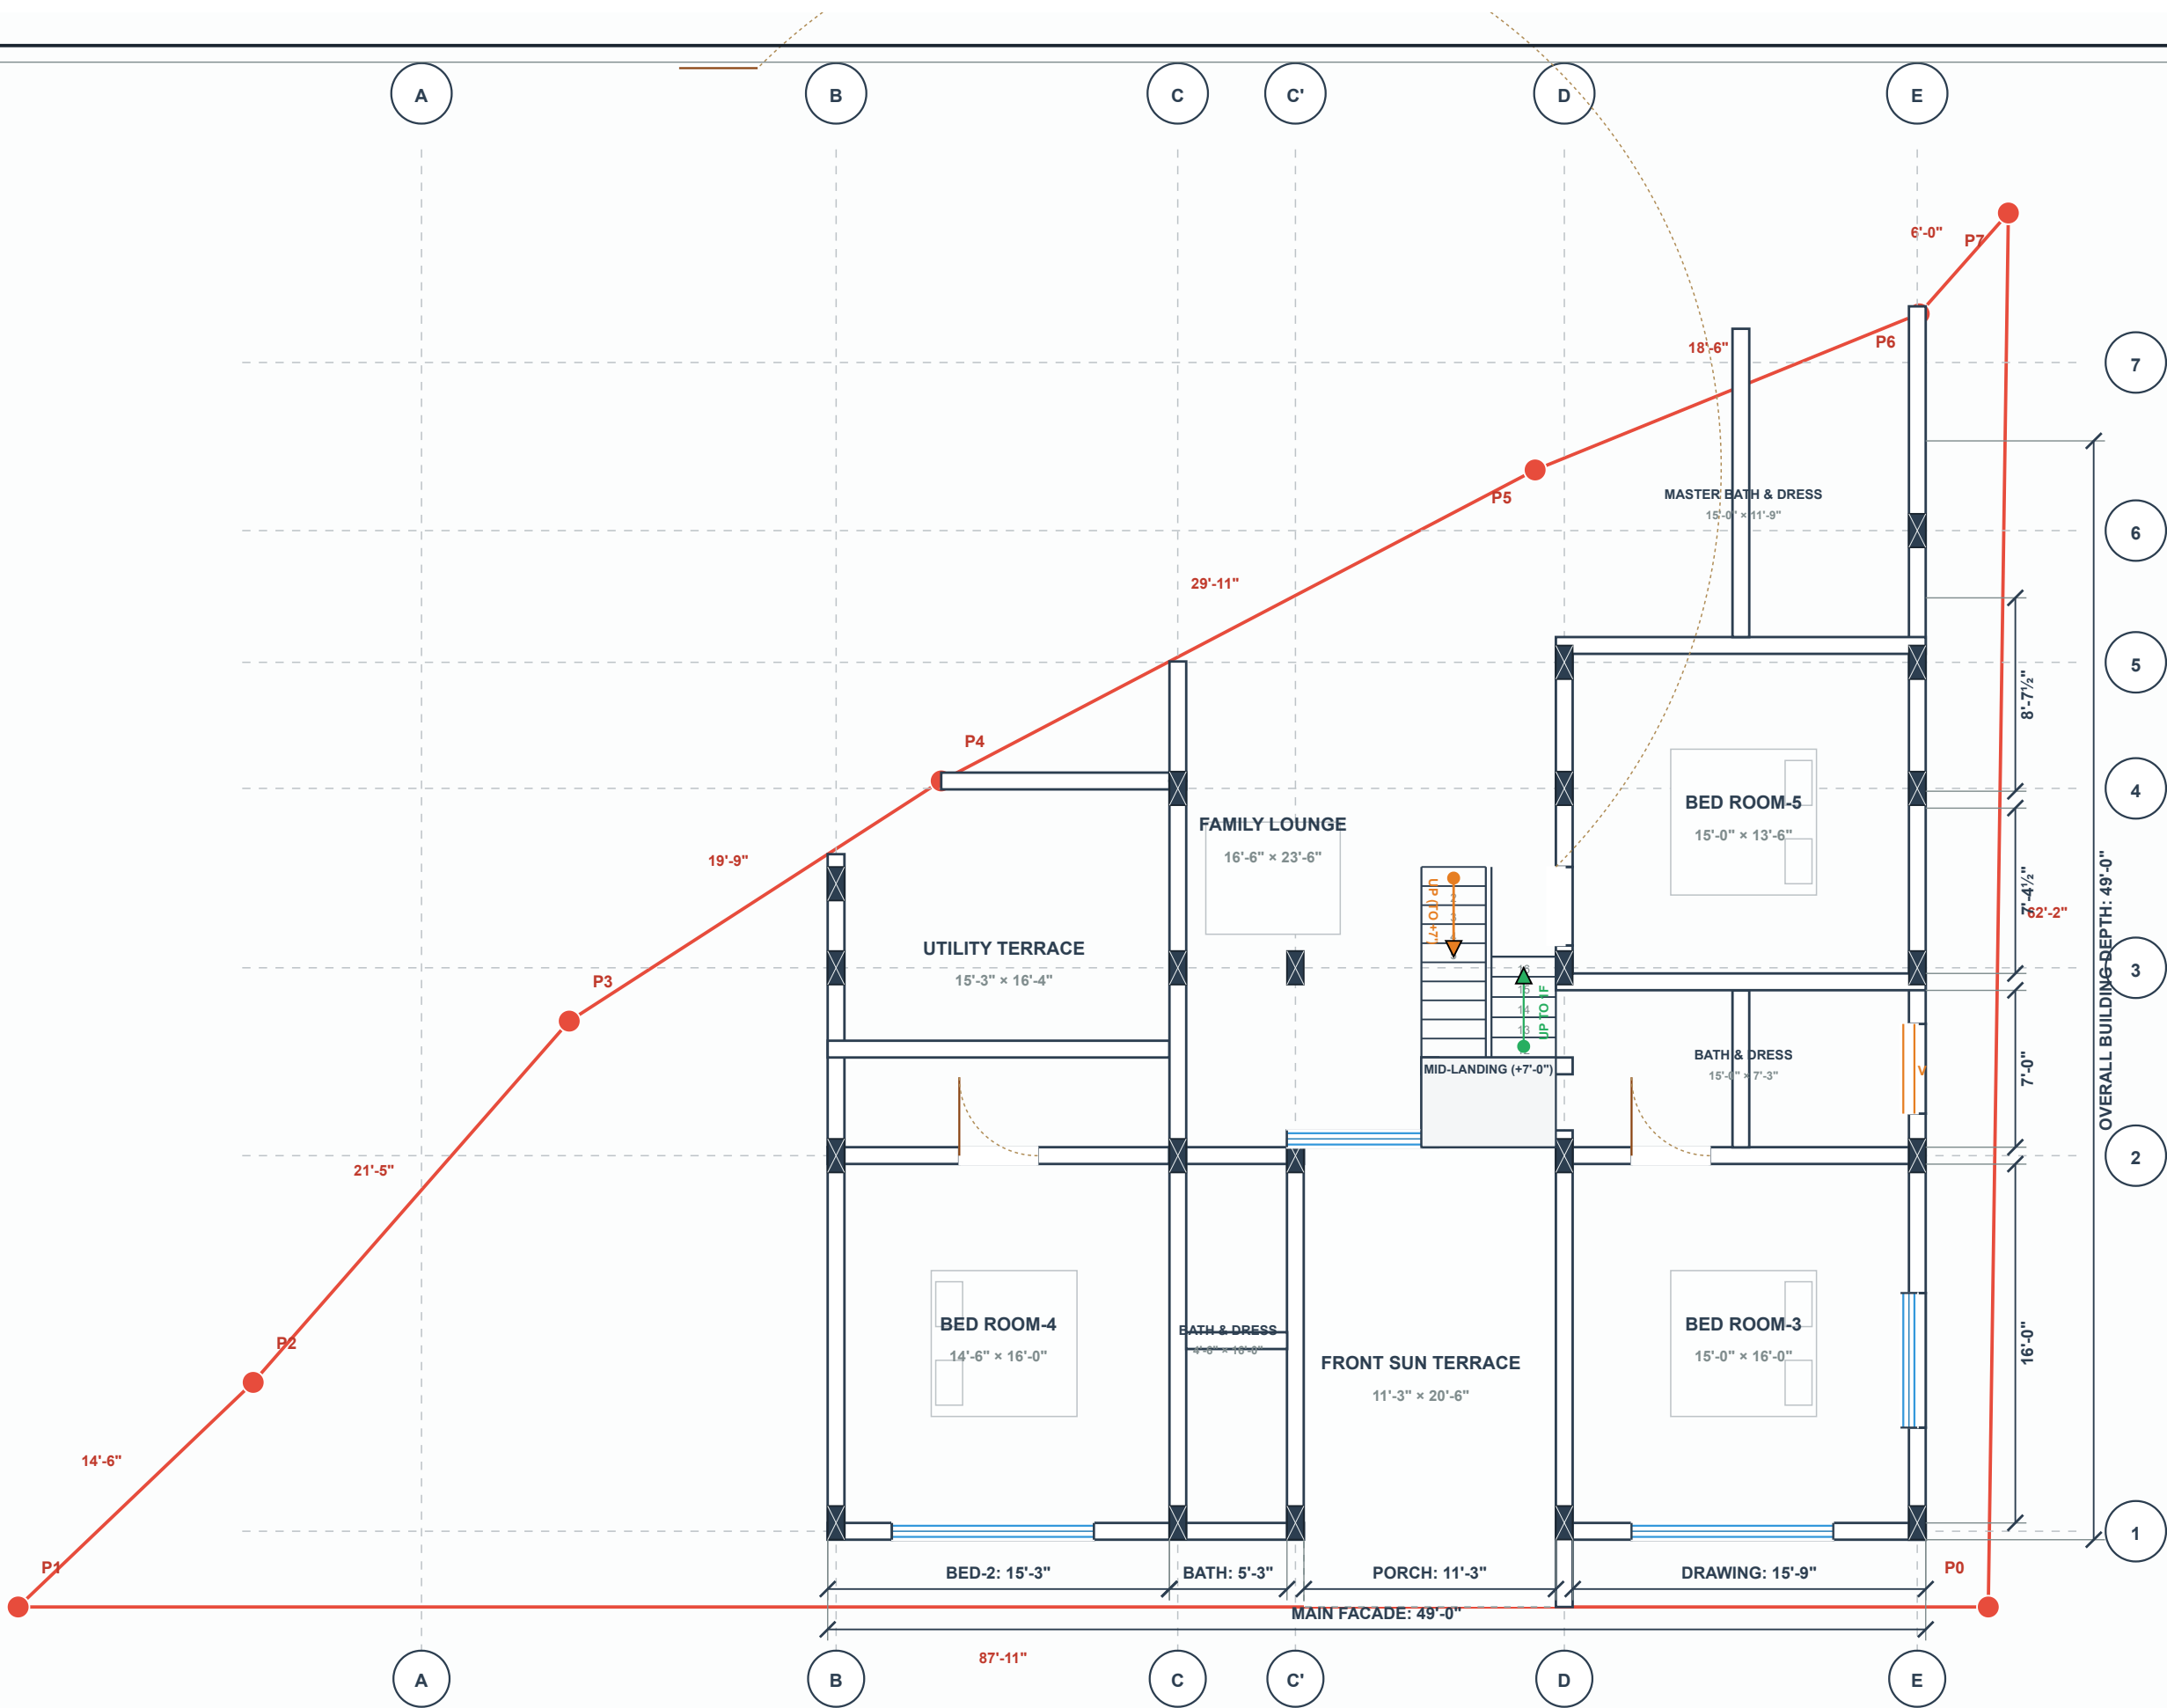

|                                                |  |                      |  |
|------------------------------------------------|--|----------------------|--|
| DAATA HAMLET RESIDENCE                         |  | PLOT: 3,129.1 SQ.FT. |  |
| DRAWING: FIRST FLOOR ARCHITECTURAL PLAN        |  | SHEET: A-102         |  |
| SCALE: 1/8" = 1'-0"   STATUS: APPROVED FOR CAD |  | UNITS: FEET-INCHES   |  |

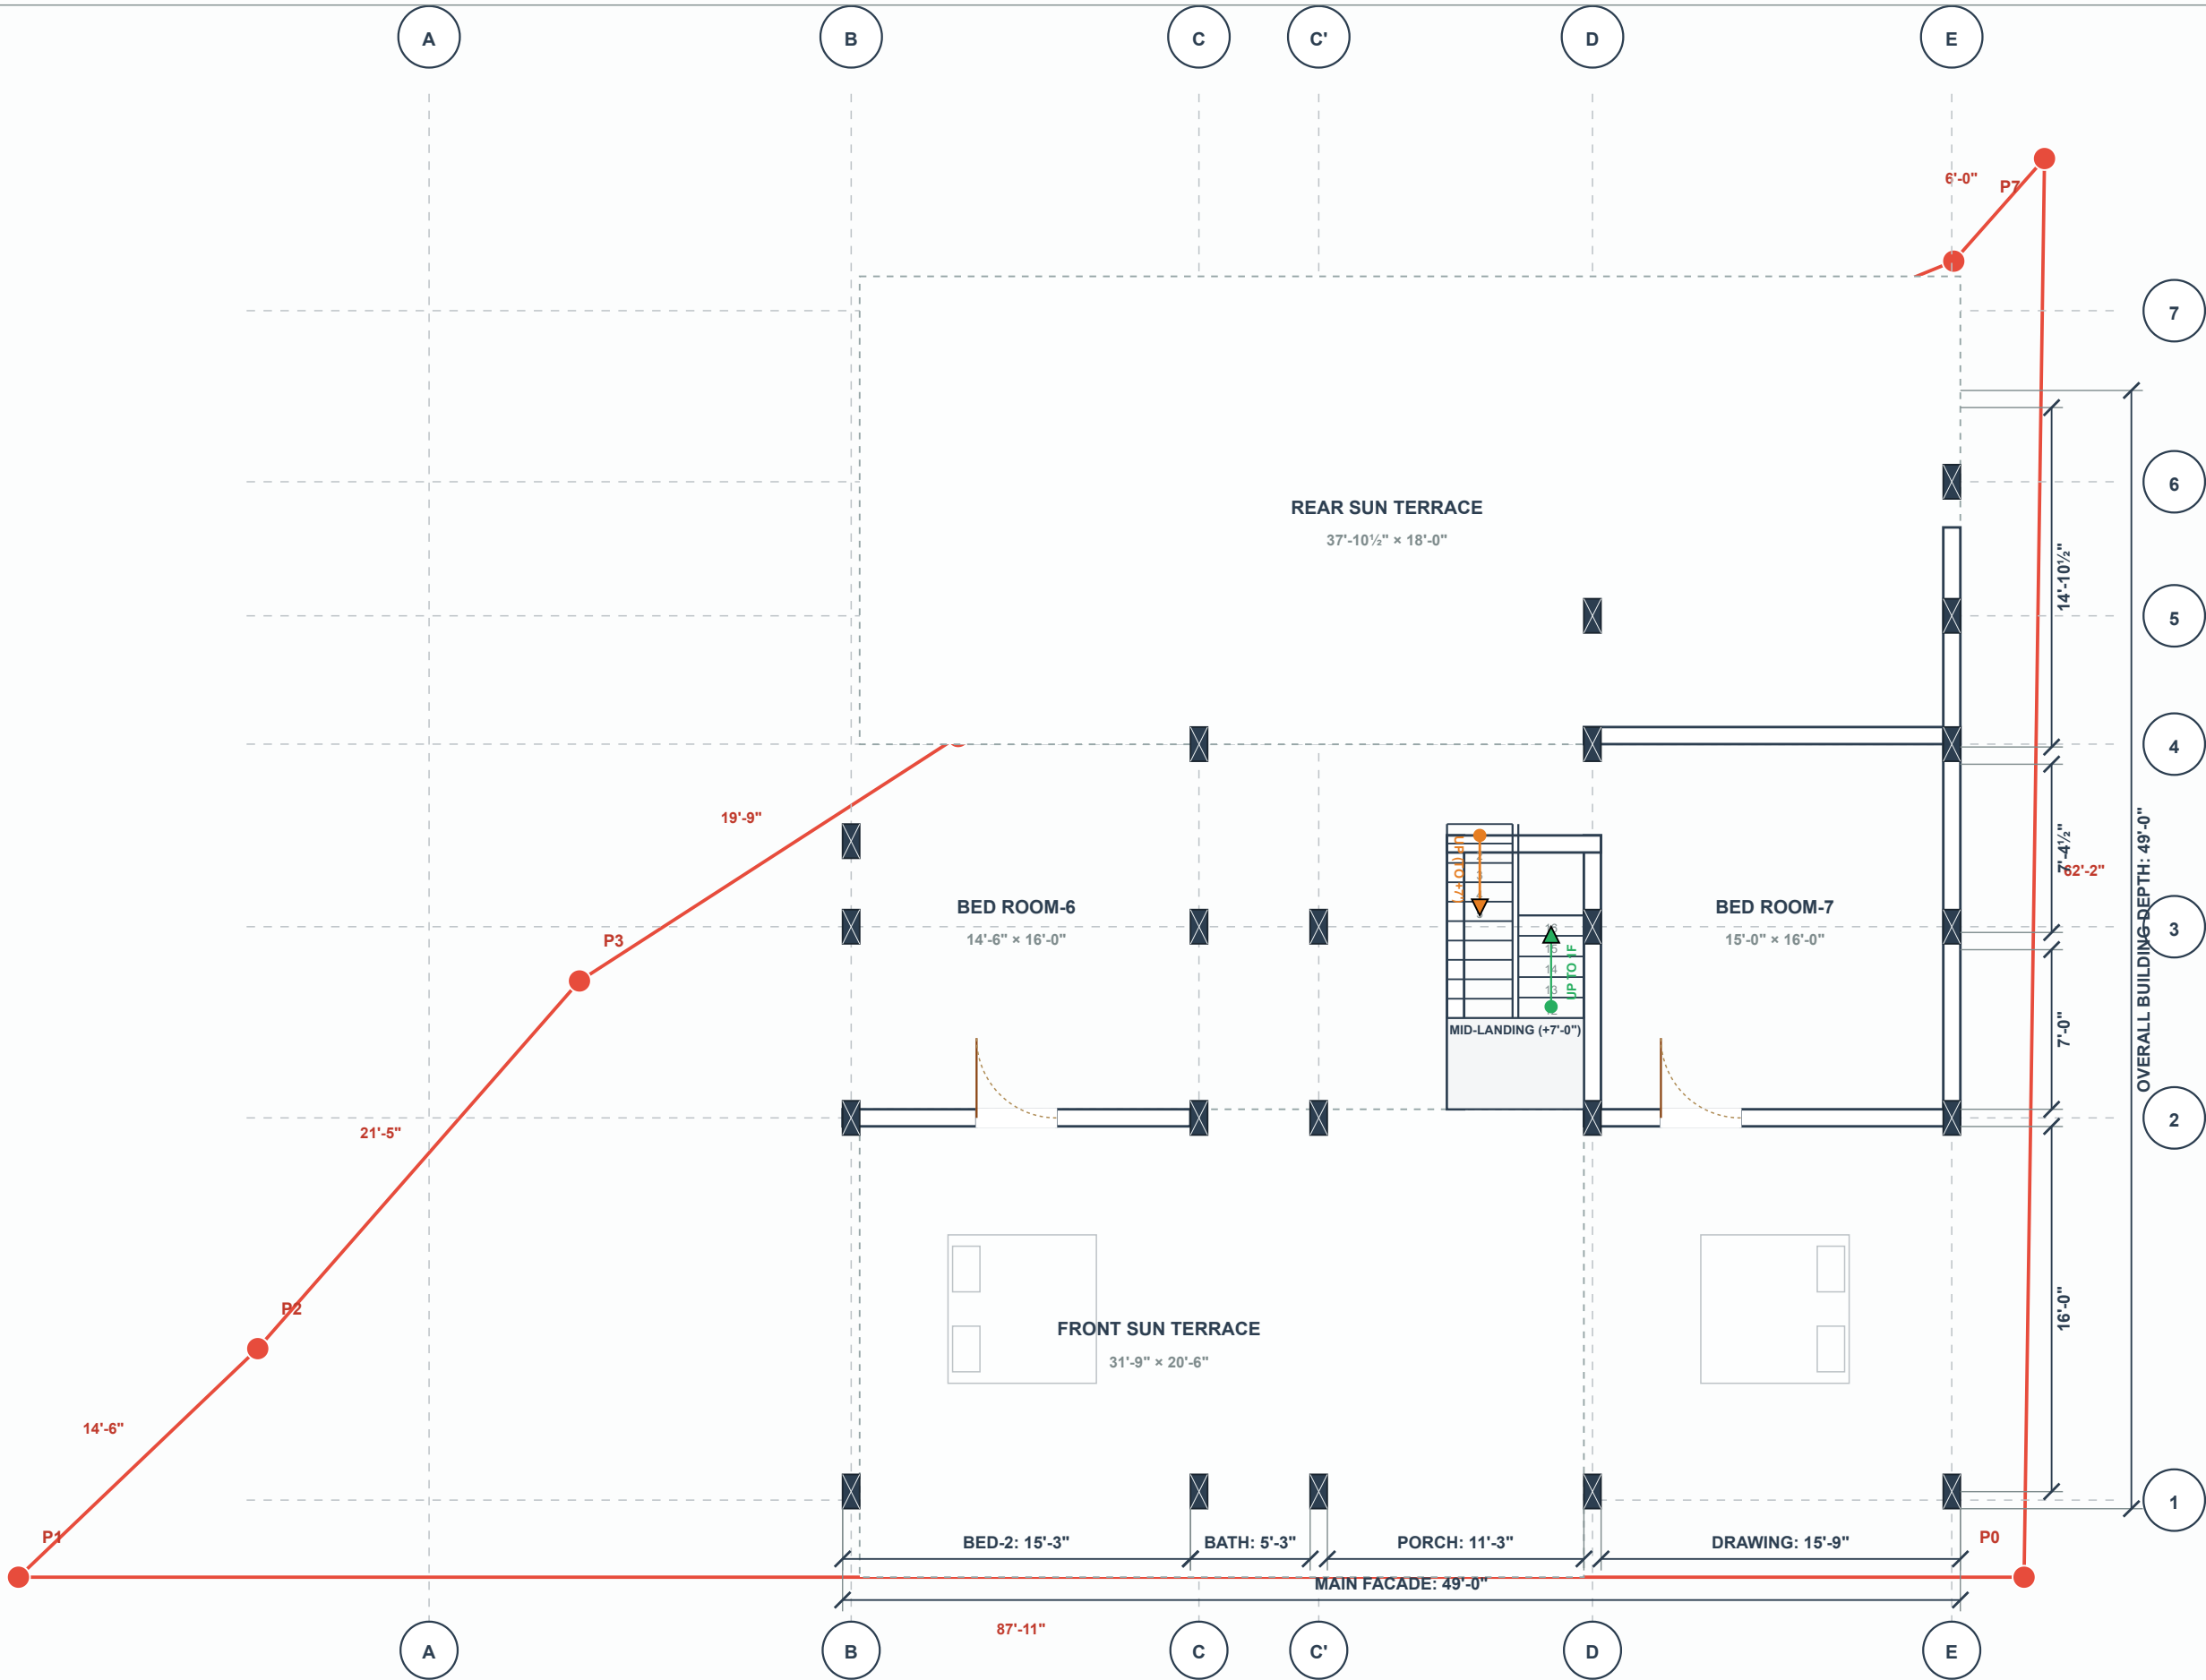


|                                                |  |                      |  |
|------------------------------------------------|--|----------------------|--|
| DAATA HAMLET RESIDENCE                         |  | PLOT: 3,129.1 SQ.FT. |  |
| DRAWING: SECOND FLOOR ARCHITECTURAL PLAN       |  | SHEET: A-103         |  |
| SCALE: 1/8" = 1'-0"   STATUS: APPROVED FOR CAD |  | UNITS: FEET-INCHES   |  |

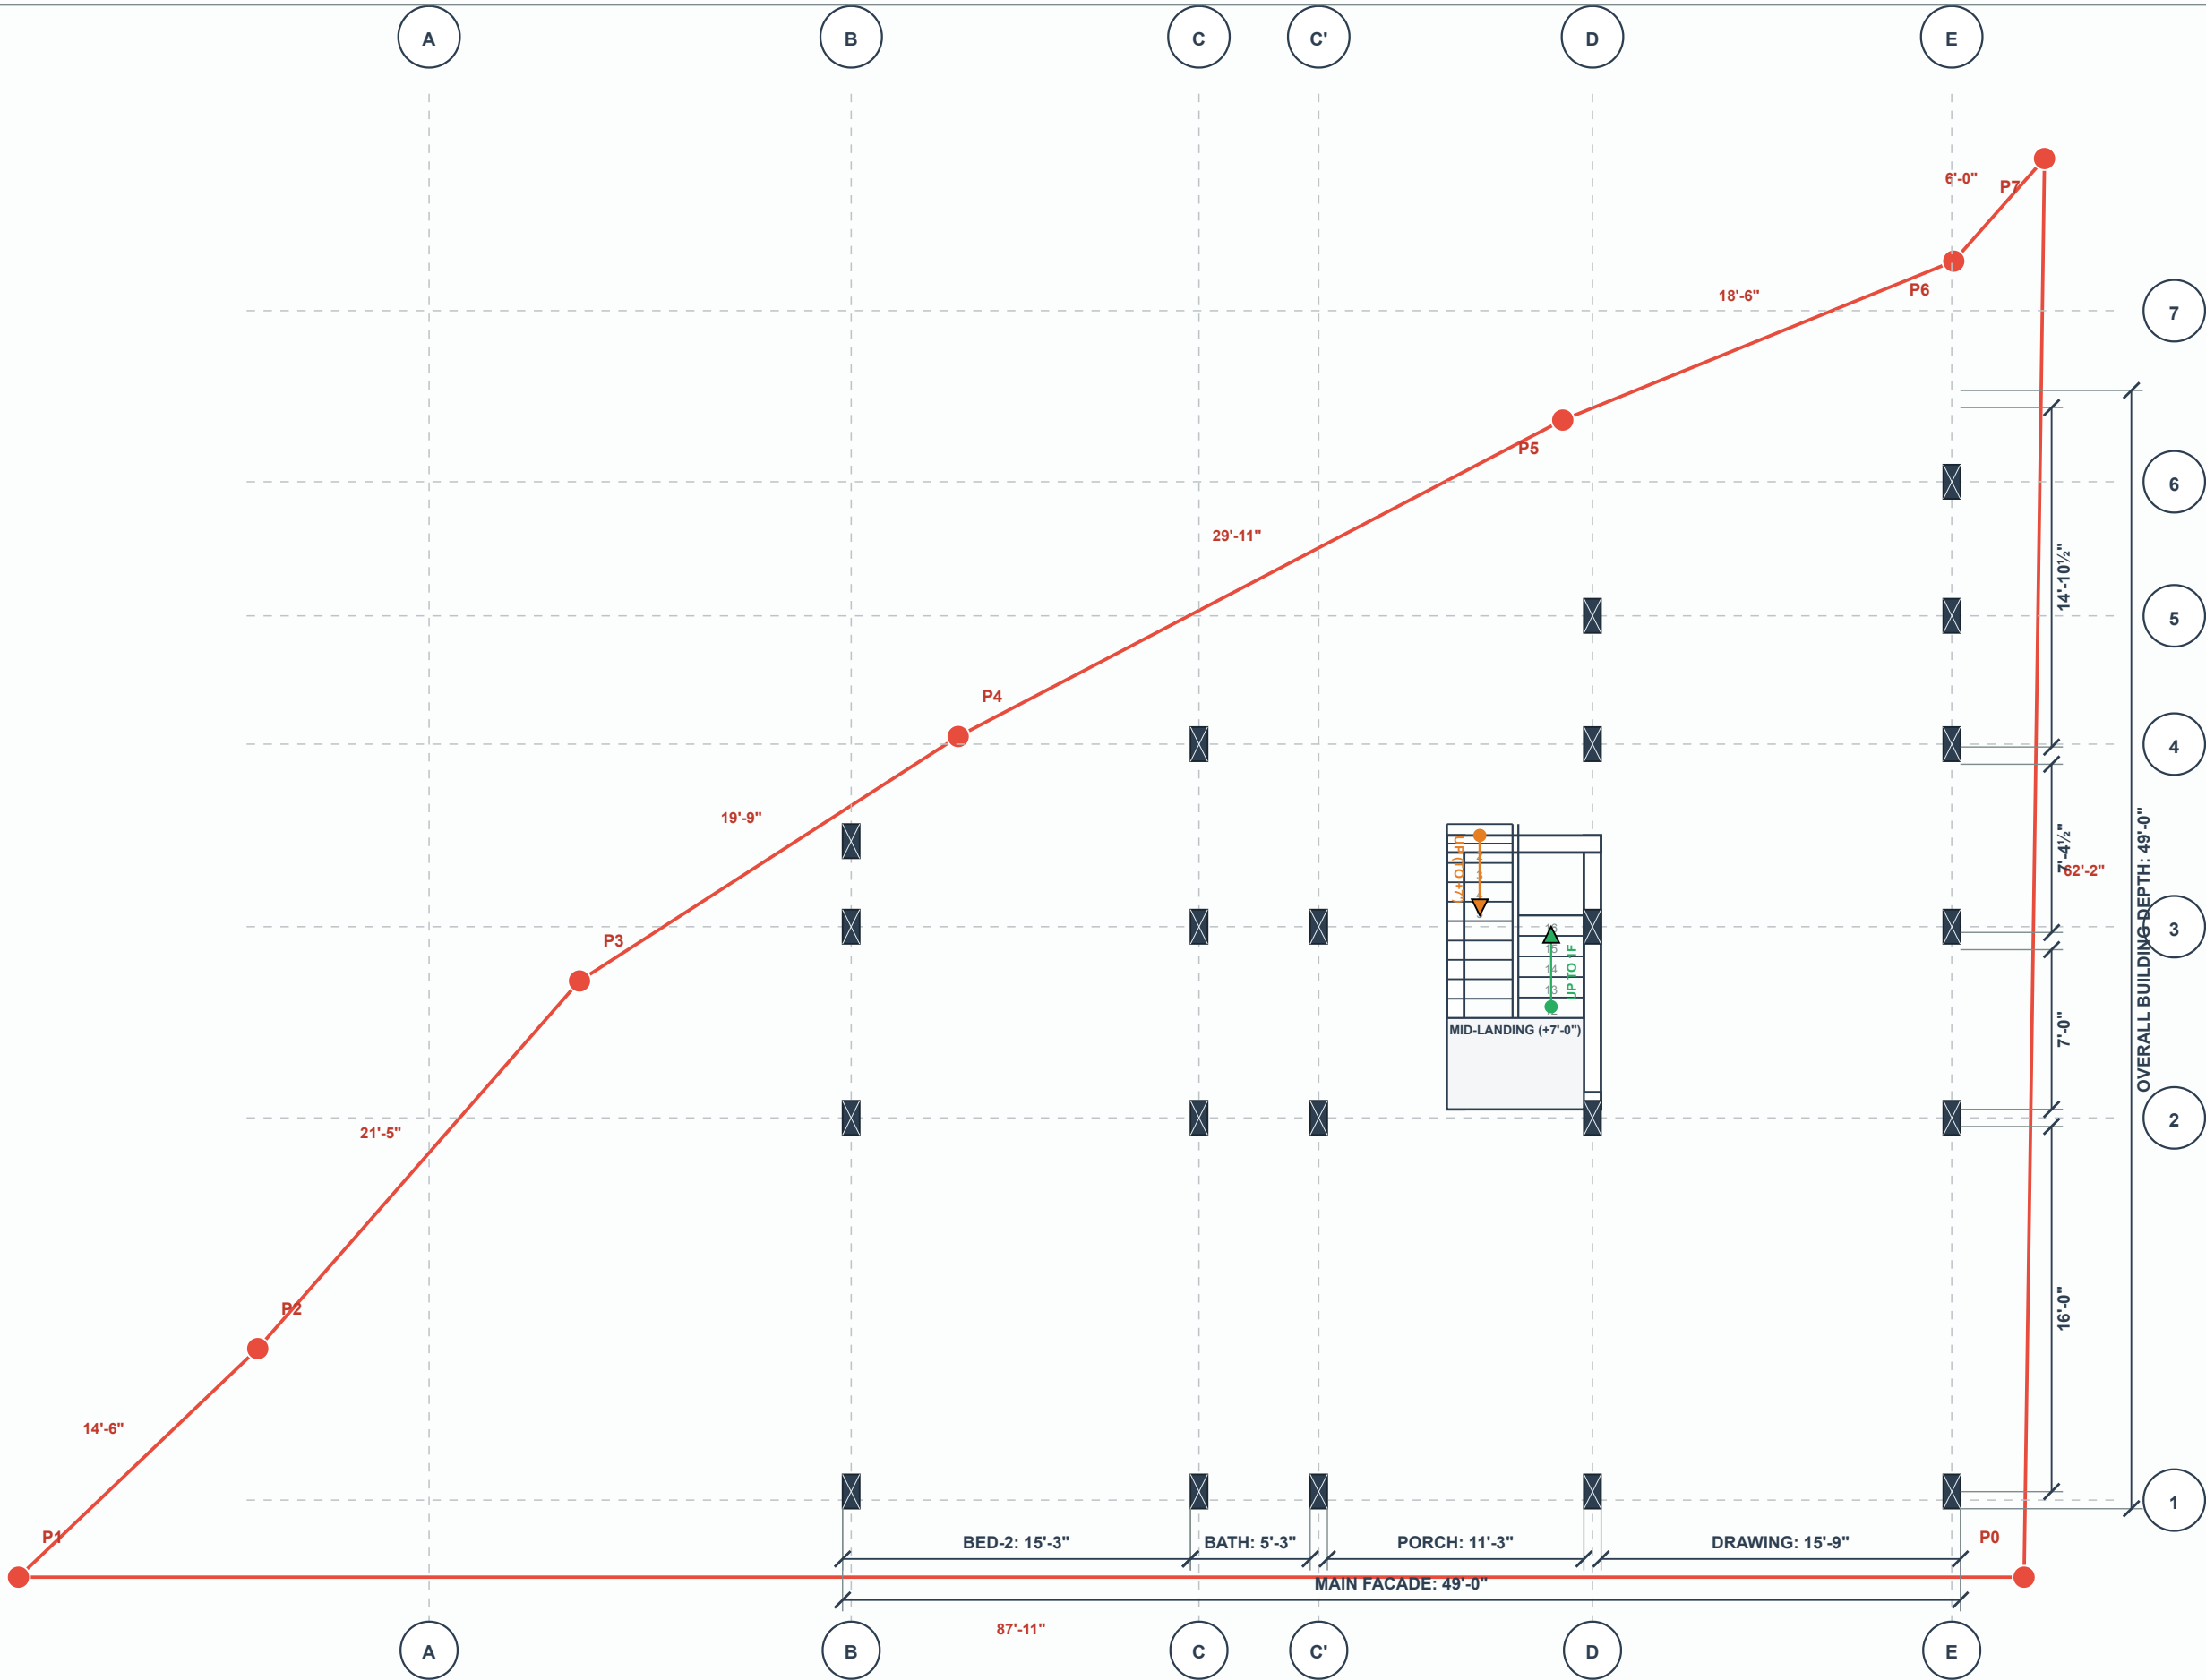

|                                                |  |                      |  |
|------------------------------------------------|--|----------------------|--|
| DAATA HAMLET RESIDENCE                         |  | PLOT: 3,129.1 SQ.FT. |  |
| DRAWING: ROOF & MUMTY PLAN                     |  | SHEET: A-104         |  |
| SCALE: 1/8" = 1'-0"   STATUS: APPROVED FOR CAD |  | UNITS: FEET-INCHES   |  |

| RCC COLUMN SCHEDULE (24 COLUMNS)   |               |               |            |
|---|---------------|---------------|------------|
| MARK   | SIZE (INCHES) | REBAR (MAIN)  | EXTENT     |
| C1 (A1-A2)   | 12" × 18"     | 8 × #6 (3/4") | GF → ROOF  |
| C2 (B, C, D, E)   | 12" × 18"     | 6 × #6 (3/4") | GF → ROOF  |
| C3 (MUMTY)   | 12" × 18"     | 6 × #6 (3/4") | GF → MUMTY |
| C4 (CHAMFER)   | 18"           | 6 × #6 (3/4") | GF → ROOF  |
| <div><div>• All 24 columns are parallel to each other.</div><div>• Concealed inside 9" walls without protrusions.</div><div>• Concrete: Class A (3,000 psi cylinder strength).</div><div>• Steel: Deformed Grade 60 (fy = 60,000 psi).</div></div> |               |               |            |

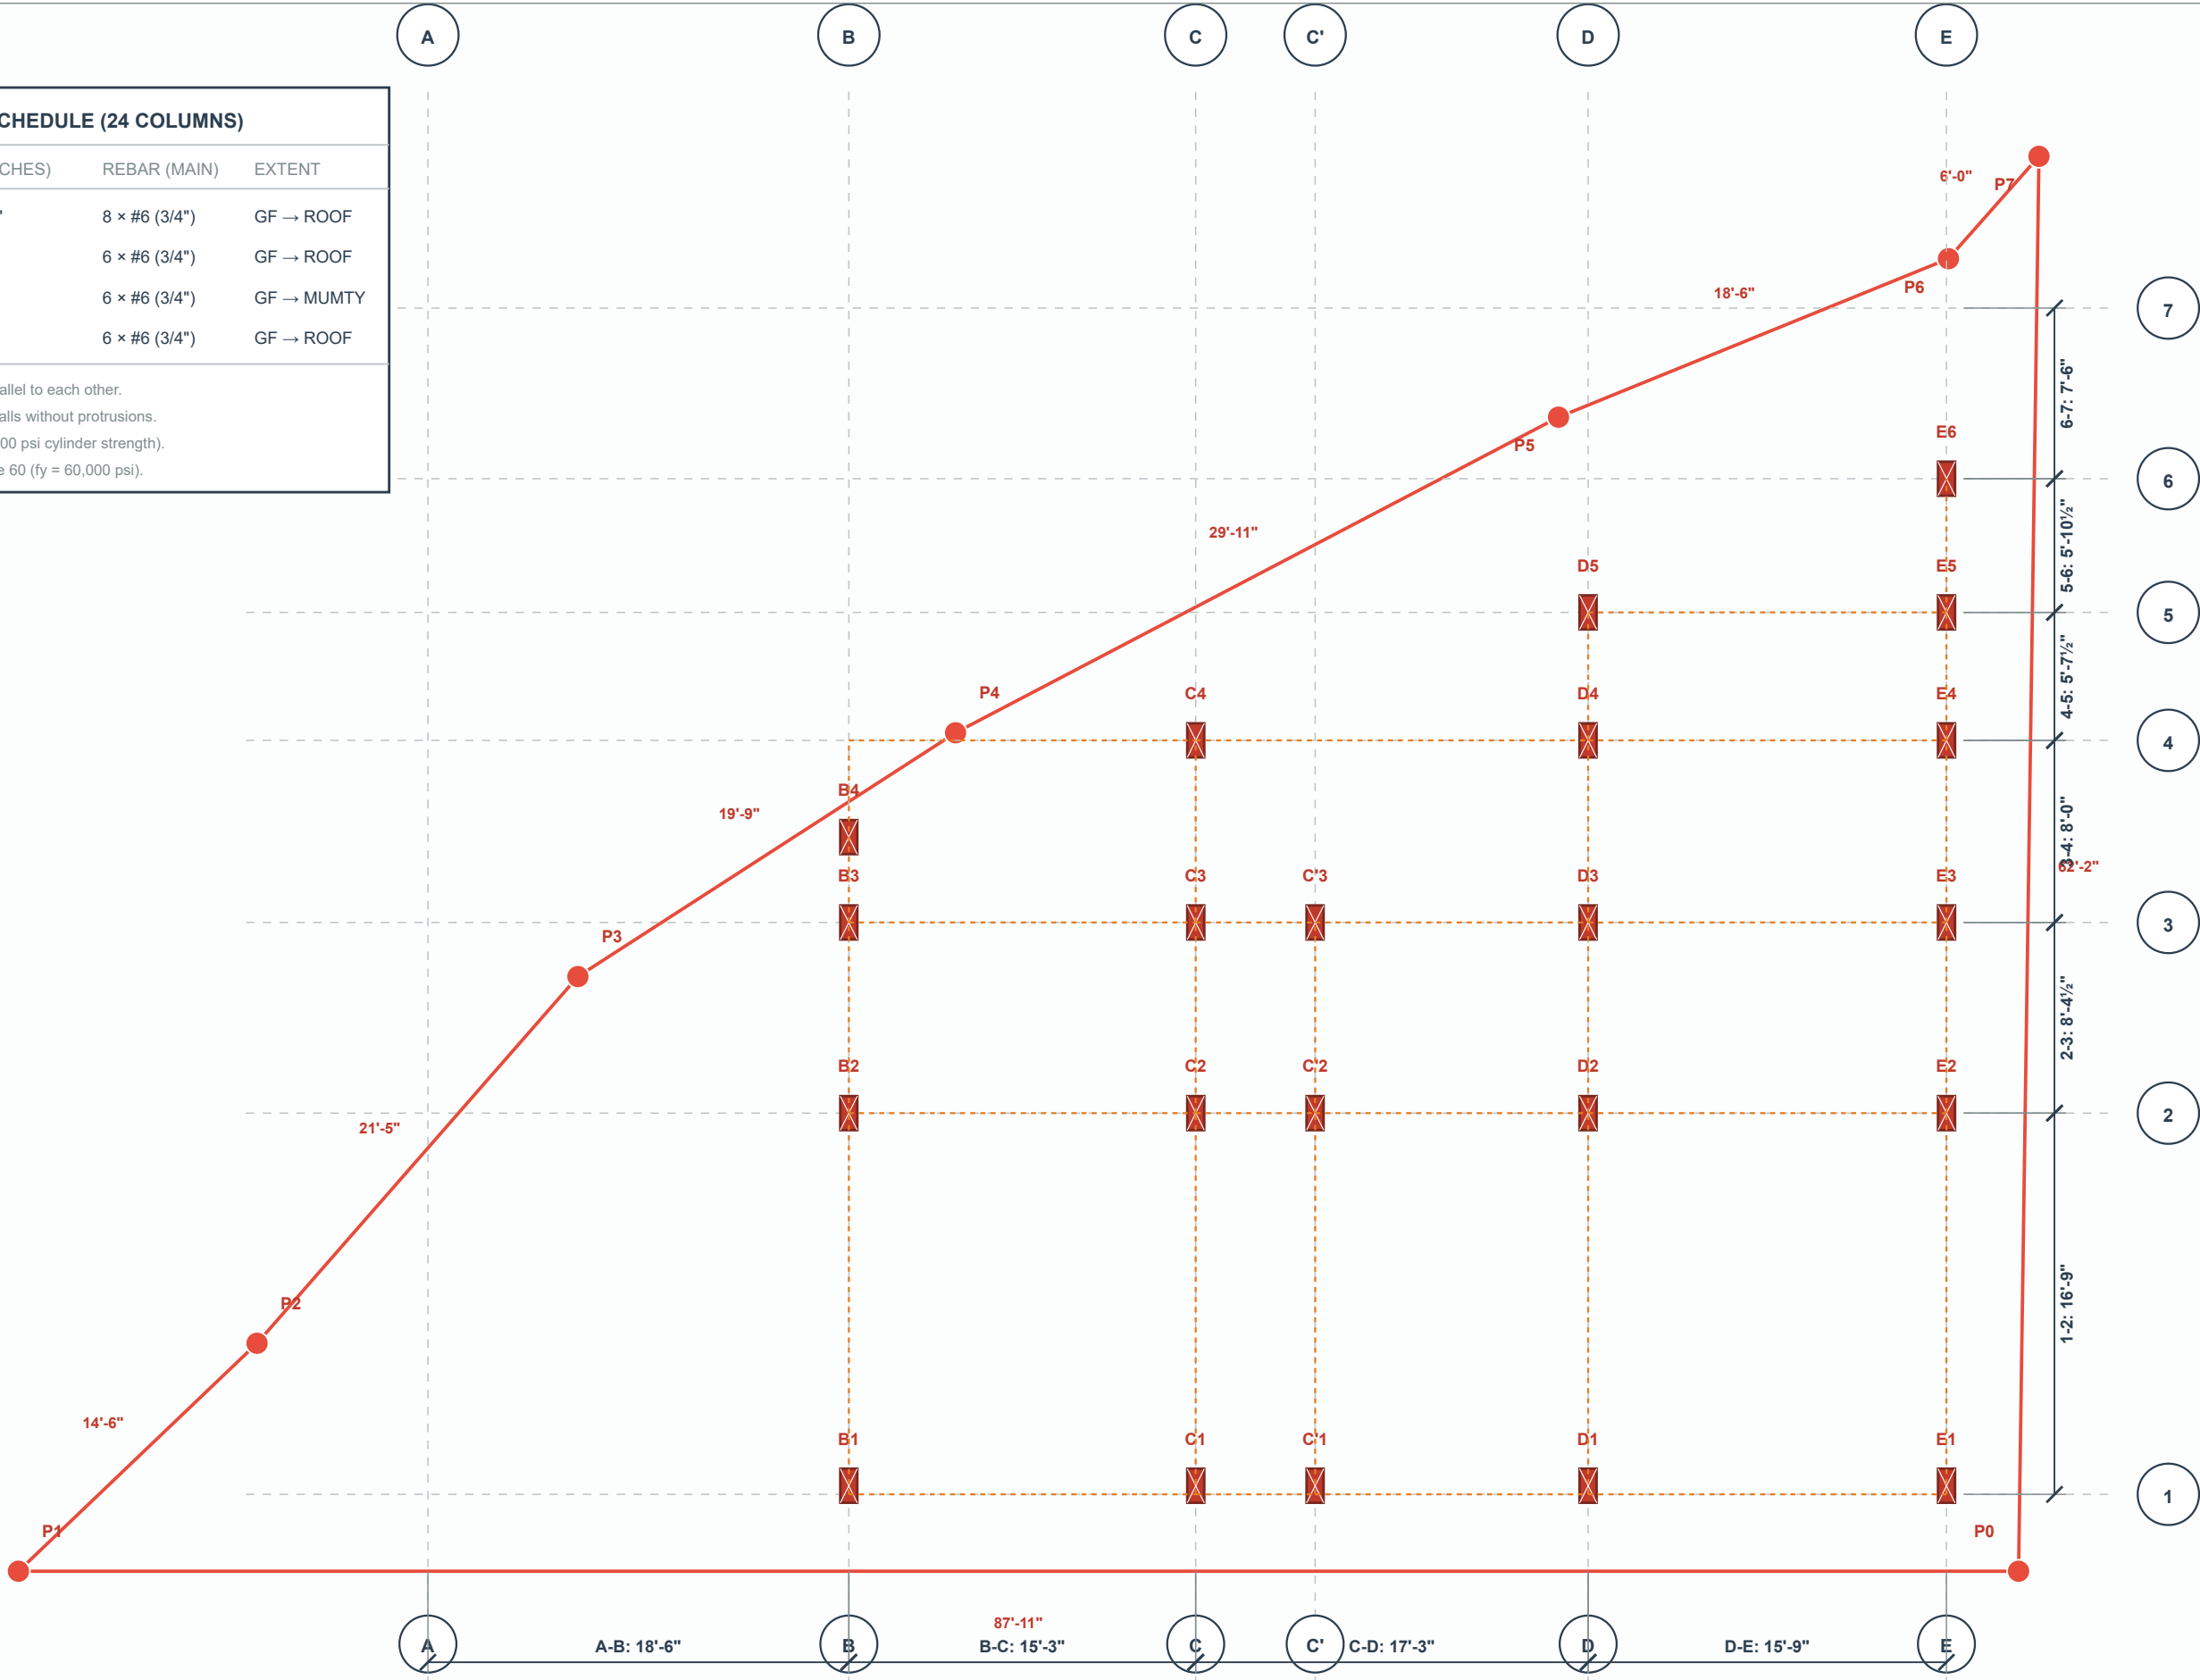

|                                                |  |                      |  |
|------------------------------------------------|--|----------------------|--|
| DAATA HAMLET RESIDENCE                         |  | PLOT: 3,129.1 SQ.FT. |  |
| DRAWING: STRUCTURAL COLUMN & GRID LAYOUT       |  | SHEET: S-101         |  |
| SCALE: 1/8" = 1'-0"   STATUS: APPROVED FOR CAD |  | UNITS: FEET-INCHES   |  |



B

C

C'

D

E

01. CENTRAL STAIRCASE MUMTY TOWER & WATER TANK (+42'-0") [GRID C'-D]

800-GAL TANK ENCLOSURE

TOP OF MUMTY CORE & TANK  
+42'-0"

2F ROOF CANOPY LEVEL  
+32'-6"

02. SECOND FLOOR WEST SUN TERRACE WITH 12mm TEMPERED GLASS RAILING

SECOND FLOOR FFL  
+22'-2"

03. FIRST FLOOR OPEN FRONT SUN TERRACE / BALCONY OVER CAR PORCH

04. 14" ANODIZED CHARCOAL BRONZE PORCH CANOPY WITH WARM LED LIGHTING

FIRST FLOOR FFL  
+11'-10"

05. BEDROOM 2 SLIDING GLASS DOOR TO MAIN LAWN (8'-6" x 7'-0")

MAIN LAWN (~500 SQ.FT OPEN GARDEN)

PLINTH FINISHED LEVEL  
+1'-6"

FINISHED GROUND LEVEL  
±0'-0"

08. MAIN LAWN FRONTAGE (~500 SQ.FT OPEN LANDSCAPED GARDEN)

PLINTH BEAM (+1'-6" FFL)

06. CENTRAL CAR PORCH (10'-3" x 20'-6") WITH 6'-0" DOUBLE MAIN ENTRANCE DOOR

07. FORMAL DRAWING ROOM SQUARE WINDOW W2 (9'-0" x 6'-6")

09. EAST PERIMETER PASSAGE REVEAL (2'-1" CLEAR) WITH SL

OVERALL PLOT FRONTAGE = 87'-11" (26.80)

MAIN LAWN: 36'-1 1/2"

BEDROOM 2: 15'-3"

BATH: 5'-3"

CAR PORCH: 12'-0"

DRAWING: 15'-9"

PASSAGE: 2'-1"

RESIDENCE FOR MR. DAATA HAMLET

WITH BOUNDARY WALL

**SOUTH FRONT ELEVATION — WITH BOUNDARY WALL (BACKGROUND)**

ARCHITECTURAL TENDER DRAWING | MASTER 3-STOREY CANOPY RESIDENCE | SCALE 1:50

SHEET NO: A-201A

SCALE: 1/4" = 1'-0" (1:50)

PLOT AREA: 3,129.1 SQ.FT (12.8 MARLA)

PROJECT: CANOPY VILLA (GF + 1F + 2F + MUMTY)

STATUS: ISSUED FOR CONSTRUCTION



B

C

C'

D

E

01. CENTRAL STAIRCASE MUMTY TOWER & WATER TANK (+42'-0") [GRID C'-D]

800-GAL TANK ENCLOSURE

TOP OF MUMTY CORE & TANK  
+42'-0"

2F ROOF CANOPY LEVEL  
+32'-6"

02. SECOND FLOOR WEST SUN TERRACE WITH 12mm TEMPERED GLASS RAILING

SECOND FLOOR FFL  
+22'-2"

03. FIRST FLOOR OPEN FRONT SUN TERRACE / BALCONY OVER CAR PORCH

04. 14" ANODIZED CHARCOAL BRONZE PORCH CANOPY WITH WARM LED LIGHTING

FIRST FLOOR FFL  
+11'-10"

05. BEDROOM 2 SLIDING GLASS DOOR TO MAIN LAWN (8'-6" x 7'-0")

PLINTH FINISHED LEVEL  
+1'-6"

FINISHED GROUND LEVEL  
±0'-0"

MAIN LAWN (1,000 SQ.FT OPEN GARDEN)

08. MAIN LAWN FRONTAGE (~500 SQ.FT OPEN LANDSCAPED GARDEN)

PLINTH BEAM (+1'-6" FFL)

06. CENTRAL CAR PORCH (10'-3" x 20'-6") WITH 6'-0" DOUBLE MAIN ENTRANCE DOOR

07. FORMAL DRAWING ROOM SQUARE FEATURE WINDOW W2 (9'-0" x 6'-6")

09. EAST PERIMETER PASSAGE REVEAL (2'-1" CLEAR) WITH SL

OVERALL PLOT FRONTAGE = 87'-11" (26.80)

MAIN LAWN: 36'-1 1/2"

BEDROOM 2: 15'-3"

BATH: 5'-3"

CAR PORCH: 12'-0"

DRAWING: 15'-9"

PASSAGE: 2'-1"

RESIDENCE FOR MR. DAATA HAMLET

WITHOUT BOUNDARY WALL

**SOUTH FRONT ELEVATION — PURE ARCHITECTURE (WITHOUT BOUNDARY WALL)**

ARCHITECTURAL TENDER DRAWING | MASTER 3-STORY CANOPY RESIDENCE | SCALE 1:50

SHEET NO: **A-201B**

SCALE: **1/4" = 1'-0" (1:50)**

PLOT AREA: **3,129.1 SQ.FT (12.8 MARLA)**

PROJECT: **CANOPY VILLA (GF + 1F + 2F + MUMTY)**

STATUS: **ISSUED FOR CONSTRUCTION**