

DAATA HAMLET
RESIDENCE

Contemporary 3-storey villa | Pakistan

PLOT	3,129.1 sq ft (290.7 m2)
	13.9 marla @225 / 11.5 @272.25
STAGE	GROUND FLOOR - DESIGN v2
UNITS	Feet-inches; origin = peg P1
LEVELS	Plot/lawn +/-0 (=road P1), FFL +0'-6"
FLOOR HT	11'-0" floor-to-floor

GENERAL NOTES

- All dimensions in feet-inches. Do not scale; follow written dimensions. Survey pegs per C-101.
- External / structural walls 9", partitions 4.5".
- RCC columns 9"x18" (21 nos) - size, steel and footing to be confirmed by structural engineer.
- Zero construction west of Line B (X=36'-1 1/2").
- Front setback 3'-0"; east service passage 2'-9 1/2" at road widening to 3'-7" at rear.
- Every bath, powder and kitchen vents directly to open air (road side, porch, OTS or passage).
- Authority bylaws (setbacks, coverage) to be verified before submission for approval.

LEGEND

- solid black = RCC column 9"x18"
- dark grey = wall (9" / 4.5")
- blue triple = window, double = ventilator
- dashed treads = stair above 4'-0" cut plane
- D# / W# / V# = door / window / vent tags
- (see schedule sheet A-103)

SHEET TITLE

GROUND FLOOR PLAN
(FURNISHED, DIMENSIONED)

SCALE

1/8" = 1'-0" (1:96)

DATE 05 OCT 2026

SHEET NO.

A-101

GROUND FLOOR PLAN

GF FFL +0'-6" | PLOT & LAWN +/-0'-0" = ROAD AT P1 (HIGHEST) | CLEAR CEILING 10'-6" | FLOOR-TO-FLOOR 11'-0"



DAATA HAMLET RESIDENCE

Contemporary 3-storey villa | Pakistan

PLOT	3,129.1 sq ft (290.7 m2)
	13.9 marla @225 / 11.5 @272.25
STAGE	GROUND FLOOR - DESIGN v2
UNITS	Feet-inches; origin = peg P1
LEVELS	Plot/lawn +/-0 (=road P1), FFL +0'-6"
FLOOR HT	11'-0" floor-to-floor


FACADE & SITE NOTES (ROAD SIDE)

- Road falls 6'-0" from P1 to P0. Plot and lawn are filled level with the road at P1 (+/-0), so nothing sits below the road. GF FFL +0'-6".
- Stone retaining wall along the front (0 to 6'-0") with a 3'-6" MS railing on top.
- Car porch: one ramp (approx. 1:4.6, grooved concrete) from the gate (-4'-3 1/2") to a wheel-stop at -0'-9", then 2 full-width risers of 7 1/2" to a 2'-6" landing at the main door.
- 4'-0" main door centred under flight-2; drawing guest door D9 off the same landing.
- Pedestrian gate 3'-6" at the east end of the lawn: 4 steps up, stone path to side door D5.
- W1 & W3 centred, sill 2'-6", 1'-6" chajja.

STAIR (SECTION A-A)


- L-type stair, 3'-6" wide, 19 risers of 6.95".
- Flight-1: 13 risers climbs to the landing at +7'-6 1/2" (sits on the powder room).
- Flight-2: 6 risers climbs the last 3'-5 1/2" to the first floor (+11'-0").
- Powder clear height under landing 7'-1 1/2" → standard 6'-9" door fits.

SOUTH (ROAD-SIDE) ELEVATION - GROUND FLOOR

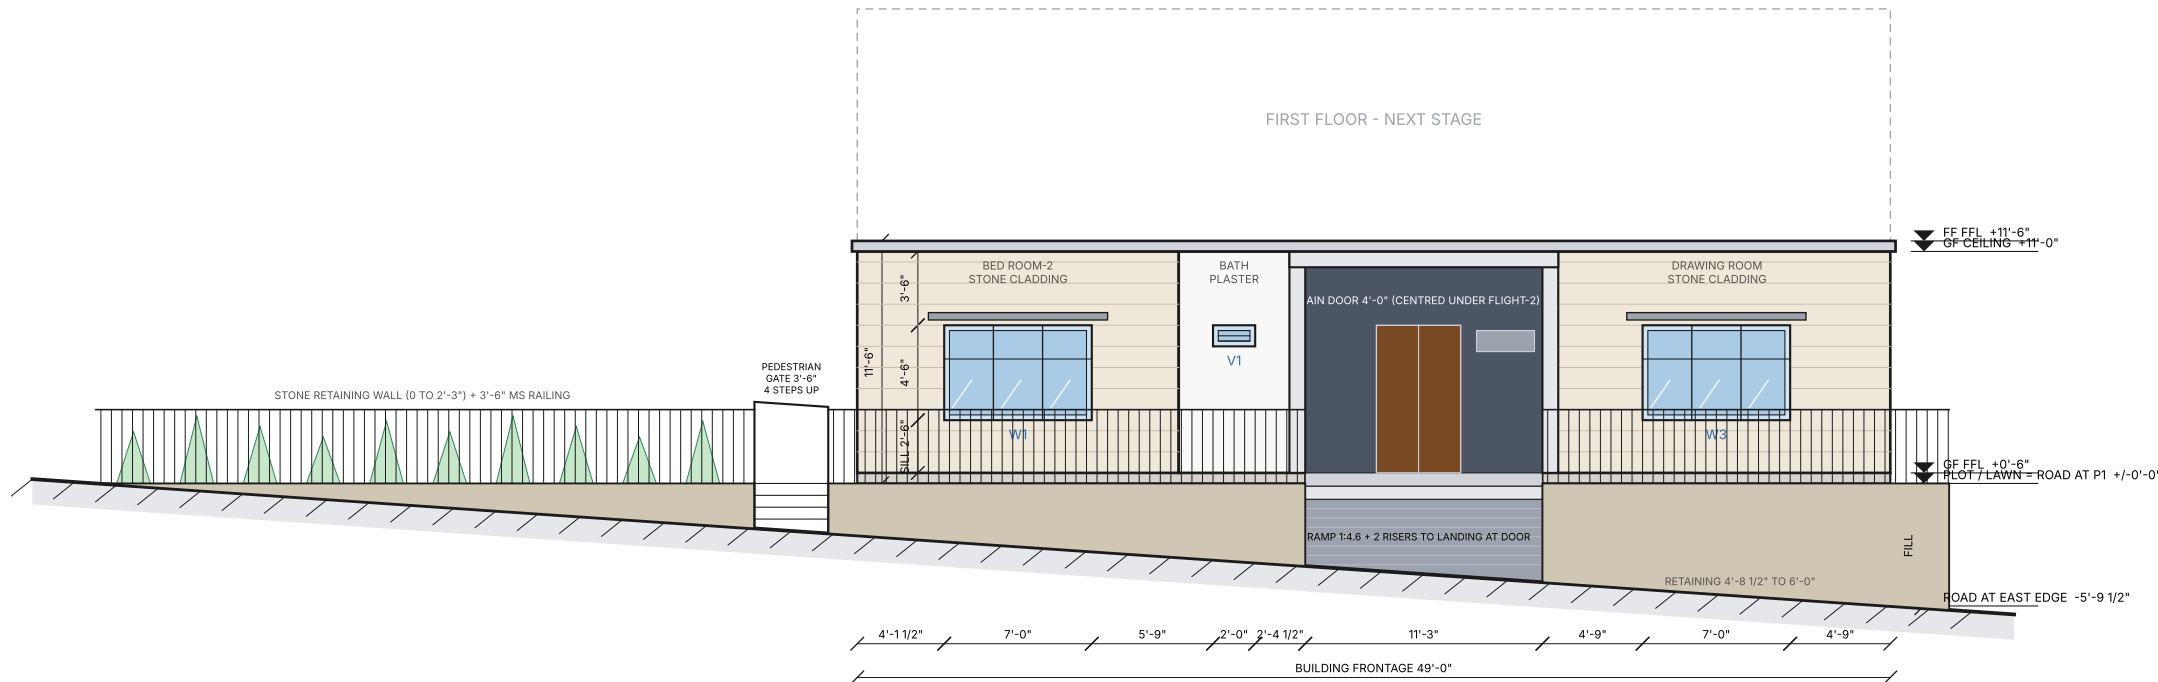

SECTION A-A : STAIR + POWDER

19 RISERS @ 6.95" | TREAD 10" | WIDTH 3'-6" | 2R+T = 23.9"

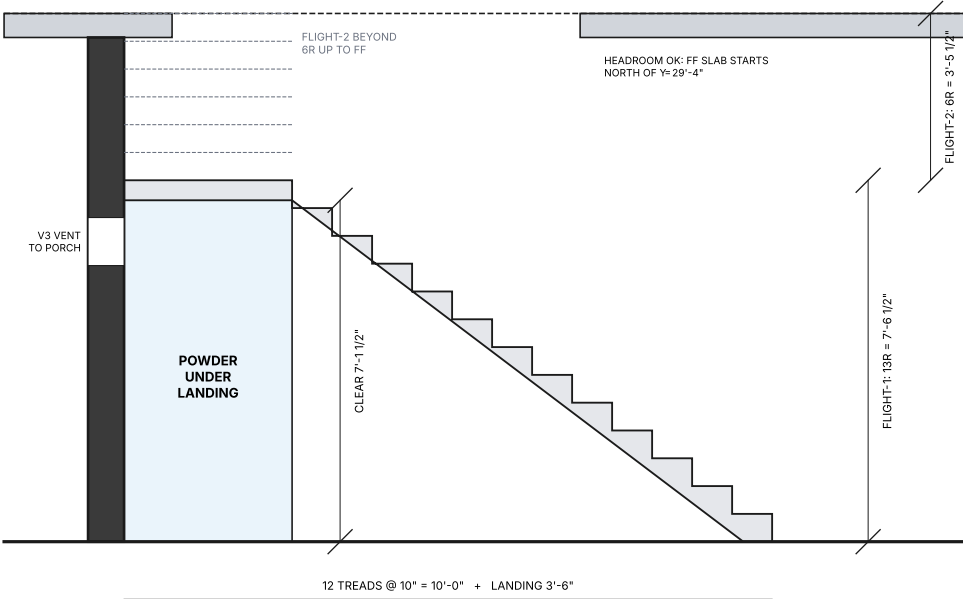

SHEET TITLE

**SOUTH ELEVATION (GF)
+ STAIR SECTION A-A**

SCALE
ELEV 1/8"=1'-0"
SECTION 1/4"=1'-0"

DATE 05 OCT 2026

SHEET NO.

A-102

ROOM AREA SCHEDULE - GROUND FLOOR

SPACE	CLEAR SIZE	NET SQ.FT
DRAWING ROOM	15'-0" x 16'-0"	240.0
BED ROOM-2	13'-9" x 16'-0"	220.0
BATH (BED-2)	5'-3" x 7'-0"	36.8
DRESS (BED-2)	5'-3" x 8'-7 1/2"	45.3
FAMILY LOUNGE + DINING	irregular (fits boundary)	336.3
KITCHEN	14'-6" x 8'-1 1/2"	117.8
DIRTY KITCHEN	14'-2" x 7'-11 1/2"	58.9
PASSAGE 4'-0" WIDE	15'-3" x 4'-0"	61.0
POWDER	irregular (fits boundary)	37.8
DRESS (DRAWING)	5'-3" x 7'-7 1/2"	40.0
BATH (DRAWING)	6'-0" x 7'-7 1/2"	45.8
BED-1	15'-0" x 15'-0"	225.0
DRESSING (BED-1)	7'-1 1/2" x 9'-2 1/2"	55.4
WASHROOM (BED-1)	7'-6" x 12'-5"	81.7
CAR PORCH	11'-3" x 19'-9"	222.2
OTS (OPEN TO SKY)	irregular (fits boundary)	55.8
TOTAL NET ENCLOSED (carpet)		1601.6
TOTAL COVERED GF (incl. walls, porch)		2081.0
GROUND COVERAGE of plot		66.5 %
MAIN LAWN (open)		651.5

DOOR SCHEDULE

TAG	SIZE (W x H)	CONNECTS (swings into 2nd)	TYPE
D1	4'-0" x 7'-0"	Car Porch → Family Lounge + Dining	Double, teak
D2	2'-6" x 7'-0"	Passage 4'-0" Wide → Bed Room-2	Flush
D4	2'-3" x 7'-0"	Bed Room-2 → Dress	Flush
D3	2'-3" x 7'-0"	Dress → Bath	Flush
D5	3'-0" x 7'-0"	Passage 4'-0" Wide → Lawn	Flush, external
D6	2'-6" x 7'-0"	Passage 4'-0" Wide → Kitchen	Flush
D7	2'-6" x 7'-0"	Kitchen → Dirty Kitchen	Flush
D8	2'-6" x 6'-9"	Family Lounge + Dining → Powder	Flush
D9	2'-4 1/2" x 7'-0"	Car Porch → Drawing Room	Flush, external
D10	2'-6" x 7'-0"	Drawing Room → Dress	Flush
D11	2'-3" x 7'-0"	Dress → Bath	Flush
D12	3'-0" x 7'-0"	Family Lounge + Dining → Bed-1	Flush
D13	2'-6" x 7'-0"	Bed-1 → Dressing	Flush
D14	2'-3" x 7'-0"	Washroom → Dressing	Flush

WINDOW & VENTILATOR SCHEDULE

TAG	SIZE	SILL	ROOM	OPENS TO	TYPE
SL1	8'-0" x 7'-0"	0'-0"	Bed Room-2	open air	sliding
W1	7'-0" x 4'-6"	2'-6"	Bed Room-2	open air	window
V1	2'-0" x 1'-0"	6'-0"	Bath	open air	vent
W2	5'-0" x 3'-6"	3'-6"	Kitchen	open air	window
V2	1'-6" x 1'-6"	5'-0"	Dirty Kitchen	OTS	vent
V3	2'-9" x 1'-0"	5'-9"	Powder	car porch	vent
W3	7'-0" x 4'-6"	2'-6"	Drawing Room	open air	window
W4	5'-0" x 4'-0"	3'-0"	Drawing Room	open air	window
V4	2'-0" x 1'-0"	6'-0"	Bath	open air	vent
W5	5'-6" x 4'-0"	3'-0"	Bed-1	open air	window
W6	3'-0" x 2'-0"	5'-0"	Washroom	open air	vent
W7	4'-6" x 4'-0"	3'-0"	Family Lounge + Dining	OTS	window
W8	3'-4 1/2" x 4'-0"	3'-0"	Family Lounge + Dining	OTS	window

AUTOMATED DESIGN CHECKS (37/37 PASS)

	CHECK	RESULT
PASS	Everything built is inside the surveyed plot	0.0000 sf outside
PASS	Zero construction west of Line B (X=36'-1 1/2")	0.0000 sf
PASS	Front setback 3'-0" kept (no wall south of Y= 3.0)	min Y of walls = 3.000
PASS	East service passage clear >= 2'-9 1/2" over full depth	width at road 2'-9 1/2", at rear 3'-7"
PASS	No two rooms overlap	[]
PASS	Walls form one continuous structure	1 piece(s)
PASS	All 21 columns sit within walls (no column inside a room)	[]
PASS	Furniture & fixtures inside rooms, clear of walls/stair (fligh	[]
PASS	Door swings clear of walls, furniture, fixtures, stair, car &	[]
PASS	Circulation routes clear (min 3'-0")	[]
PASS	Direct ventilation: BATH (BED-2)	V1→outside
PASS	Direct ventilation: KITCHEN	W2→outside
PASS	Direct ventilation: DIRTY KITCHEN	V2→ots
PASS	Direct ventilation: POWDER	V3→porch
PASS	Direct ventilation: BATH (DRAWING)	V4→outside
PASS	Direct ventilation: WASHROOM (BED-1)	W6→outside
PASS	Daylight: BED-1	W5→outside
PASS	Daylight: BED ROOM-2	SL1→outside, W1→outside
PASS	Daylight: DRAWING ROOM	W3→outside, W4→outside
PASS	Daylight: FAMILY LOUNGE + DINING	W7→ots, W8→ots
PASS	Daylight: KITCHEN	W2→outside
PASS	Every door connects two spaces	D1a: LNG↔PORCH; D1b: PORCH↔LNG; D2: BED2
PASS	19 equal risers = 11'-0" floor-to-floor	riser 6.95"
PASS	Comfort rule 2R+T between 23" and 25"	2R+T = 23.9"
PASS	Stair width >= 3'-0" (provided 3'-6")	
PASS	Powder door (6'-9" high) fits under landing soffit	landing +7'-6 1/2", 5" slab → soffit 7'-1 1
PASS	Headroom >= 6'-8" everywhere on flight-1 (FF slab void from Y=	FF slab may resume north of Y=29.32
PASS	Walk-through under flight-2 to powder: >= 6'-8" for X <= 64.5	underside 7'-6 1/2" at X=64.5, 9'-3 1/2" at
PASS	Everything (plot, lawn, house) at or above road level	plot 0'-0", FFL +0'-6", road max +/-0 at P1
PASS	Car ramp: one slope from gate, max 1:4.5	1:4.58 from gate -4'-3 1/2" to -0'-9" at whe
PASS	Only 2 risers (7 1/2") in the porch, full width	2 × 7.5" → landing at FFL +0'-6"
PASS	Entrance landing >= 2'-6" in front of main door & D9	2'-6" deep
PASS	SUV fits on the ramp (wheel-stop before the step)	car Y 0.25-16.0, side gaps 2'-0" / 3'-0"
PASS	Pedestrian gate: 4 equal risers up into the lawn	4 × 6.76" from road -2'-3" to lawn 0'-0"
PASS	Main door centred under flight-2	door centre X=62.75, flight-2 centre X=63.04
PASS	Main door head (7'-0") below flight-2 soffit	soffit at door jamb 7'-4 1/2"
PASS	Bed-2 en-suite is dress-through (bed → dress → bath)	D4 bed→dress, D3 dress→bath

DAATA HAMLET RESIDENCE

Contemporary 3-storey villa | Pakistan

PLOT	3,129.1 sq ft (290.7 m2) 13.9 marla @225 / 11.5 @272.25
STAGE	GROUND FLOOR - DESIGN v2
UNITS	Feet-inches; origin = peg P1
LEVELS	Plot/lawn +/-0 (=road P1), FFL +0'-6"
FLOOR HT	11'-0" floor-to-floor

WHAT CHANGED vs. THE OLD BRIEF

- Stair re-planned as an L: landing sits on the powder (half in the lounge), 13R + 6R = 11'-0". Old brief had 16 risers (only 10'-2").
- Kitchen kept fully inside the plot (old one crossed the boundary by ~7 sq ft).
- Dirty kitchen fills the P4 corner (59 sq ft).
- Bed-1 rebalanced to 15'x15'; dressing and washroom run right up to the north boundary
 - no leftover strip along the hypotenuse.
- Main door centred under flight-2. Porch is one ramp + 2 risers (plinth reduced to 6" so that plot & lawn stay at/above road level).
- Pedestrian gate + stone path in the lawn.
- Bed-2 suite is dress-through: bed → dress (5'-3"x8'-7 1/2") → bath (5'-3"x7'-0").
- U-shaped kitchen: 4'-1" work aisle (an island would have left only 1'-6").
- Lawn is 652 sq ft (old brief said 588.9).

SHEET TITLE

SCHEDULES + DESIGN VERIFICATION

SCALE

N.T.S.

DATE 05 OCT 2026

SHEET NO.

A-103