


DOOR SCHEDULE

TAG	TYPE	SIZE W x H	FROM → TO	LEAF OPENS
D1	DT-0 5'-0" DOUBLE	5'-0" x 7'-0"	Car porch landing ↔ Lounge	both leaves out to landing
D2	DT-1 3'-6"	3'-6" x 7'-0"	Passage 4'-0" Wide → Bed Room-2	into Bed Room-2
D4	DT-2P 2'-6" POCKET	2'-6" x 7'-0"	Dress ↔ Bed Room-2	slides into wall
D3	DT-3 2'-0"	2'-0" x 7'-0"	Dress → Bath	into Bath
D5	DT-1 3'-6"	3'-6" x 7'-0"	Lawn → Passage 4'-0" Wide	into Passage 4'-0" Wide
D6	DT-1 3'-6"	3'-6" x 7'-0"	Passage 4'-0" Wide → Kitchen	into Kitchen
D7	DT-1 3'-6"	3'-6" x 7'-0"	Kitchen → Dirty Kitchen	into Dirty Kitchen
D8	DT-3 2'-0"	2'-0" x 6'-9"	Lounge → Powder	into Powder
D9	DT-1 3'-6"	3'-6" x 7'-0"	Car porch landing → Drawing Room	into Drawing Room
D10	DT-2P 2'-6" POCKET	2'-6" x 7'-0"	Drawing Room ↔ Dress	slides into wall
D11	DT-3 2'-0"	2'-0" x 7'-0"	Dress → Bath	into Bath
D12	DT-1 3'-6"	3'-6" x 7'-0"	Bed-1 → Lounge	into Lounge
D13	DT-2S 2'-6" SLIDING	2'-6" x 7'-0"	Bed-1 ↔ Dressing	slides on bed-room face
D14	DT-3 2'-0"	2'-0" x 7'-0"	Washroom → Dressing	into Dressing


WINDOW & VENTILATOR SCHEDULE

TAG	SIZE W x H	SILL	HEAD	ROOM	OPENS TO	TYPE
W9	1'-6" x 6'-0"	1'-0"	7'-0"	Lounge	car porch	window
SL1	8'-0" x 7'-0"	0'-0"	7'-0"	Bed Room-2	open air	sliding
W1	7'-0" x 4'-6"	2'-6"	7'-0"	Bed Room-2	open air	window
V1	2'-0" x 1'-0"	6'-0"	7'-0"	Bath	open air	vent
W2	5'-0" x 3'-6"	3'-6"	7'-0"	Kitchen	open air	window
V2	1'-6" x 1'-6"	5'-0"	6'-6"	Dirty Kitchen	OTS	vent
V3	2'-9" x 1'-0"	5'-9"	6'-9"	Powder	car porch	vent
W3	7'-0" x 4'-6"	2'-6"	7'-0"	Drawing Room	open air	window
W4	5'-0" x 4'-0"	3'-0"	7'-0"	Drawing Room	open air	window
V4	2'-0" x 1'-0"	6'-0"	7'-0"	Bath	open air	vent
W5	5'-6" x 4'-0"	3'-0"	7'-0"	Bed-1	open air	window
W6	3'-0" x 2'-0"	5'-0"	7'-0"	Washroom	open air	vent
W7	4'-6" x 4'-0"	3'-0"	7'-0"	Lounge	OTS	window
W8	3'-4 1/2" x 4'-0"	3'-0"	7'-0"	Lounge	OTS	window

DOOR TYPES

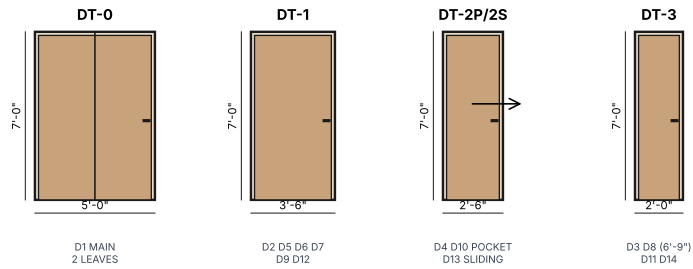

WINDOW & VENT TYPES (HEIGHTS FROM FFL)

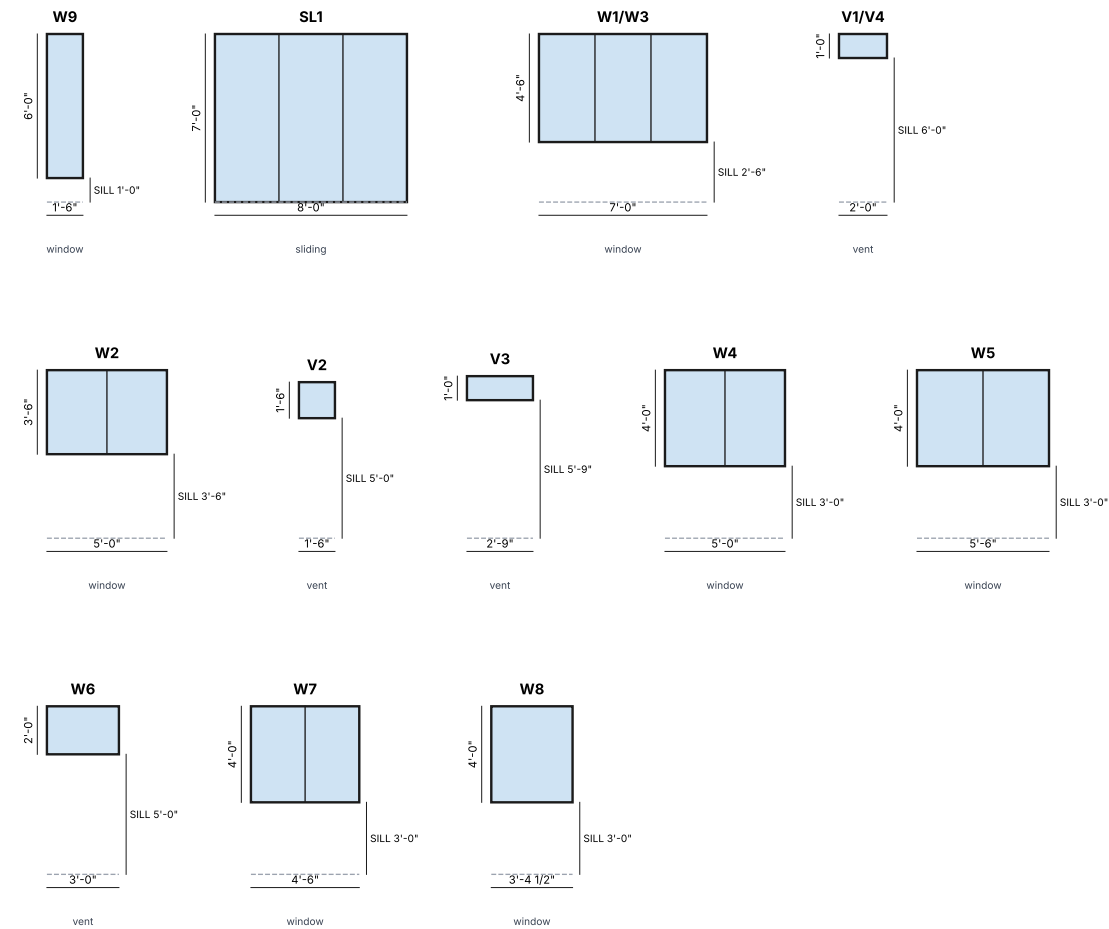

DAATA HAMLET RESIDENCE

Ground floor | Pakistan

PLOT	3,129.1 sq ft (290.7 m2)
MARLA	13.9 @ 225 sf 11.5 @ 272.25 sf
LEVELS	Datum +/-0 = road at P1 (highest) Plot & lawn +/-0, GF FFL +0'-6"
FLOOR HT	11'-0" floor to floor, 10'-6" clear
UNITS	Feet-inches; origin = peg P1
REVISION	REV-03 05 OCT 2026

DOOR & WINDOW NOTES

- Door heights 7'-0" (powder 6'-9" under the stair landing). Frames: 2"x5" seasoned wood.
- Main door D1: 5'-0" double teak, both leaves open out onto the 3'-6" covered landing.
- Room doors 3'-6" solid-core flush; baths & powder 2'-0" WPC (water-proof).
- Dressing doors 2'-6" SLIDING: D4 & D10 run into a pocket in the 9" wall, D13 on a top track on the Bed-1 face. All wardrobes have sliding shutters.
- Lawn door D5 opens INWARD into the passage.
- Swing leaves hinge on the corner side and park flat against the adjoining wall.
- Windows: aluminium, 5mm tinted glass, MS safety grill inside. Vents: frosted louvres.
- W9 is a fixed glazed sidelight to the door.
- Sill / head heights are above the GF FFL.

SHEET TITLE

DOOR & WINDOW SCHEDULE + TYPES


SCALE

1/8" = 1'-0" (TYPES)

SHEET NO.


D-101

ENLARGED PLAN : STAIR, POWDER & ENTRANCE (1/4"=1'-0")

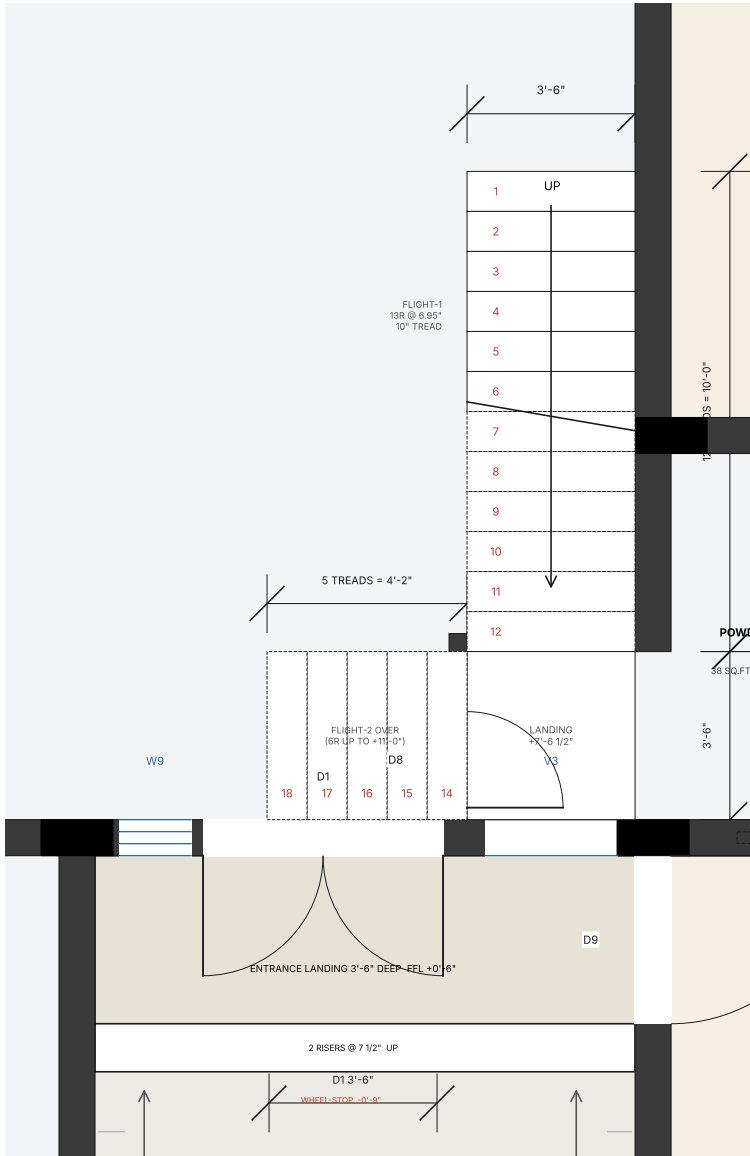


SECTION A-A : STAIR + POWDER

19 RISERS @ 6.95" | TREAD 10" | WIDTH 3'-6" | 2R+T = 23.9"

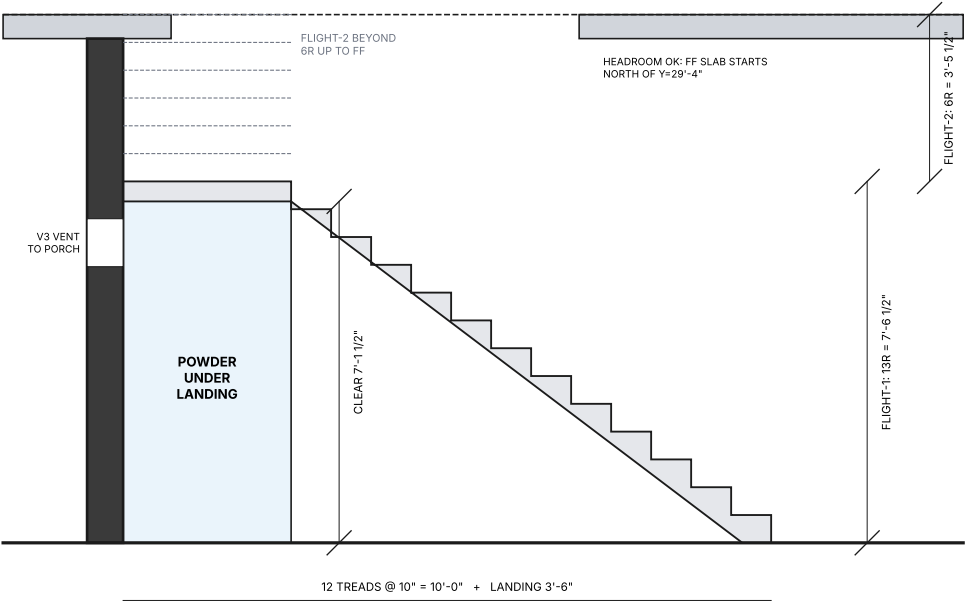

SECTION B-B : CAR PORCH RAMP & ENTRANCE

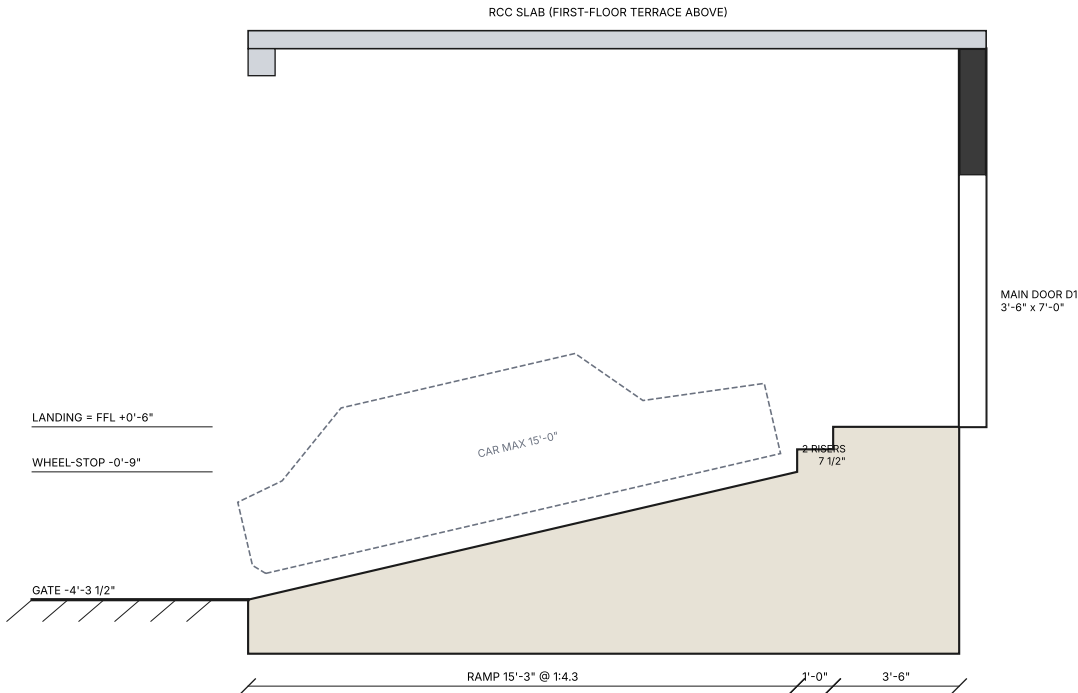

DAATA HAMLET
RESIDENCE

Ground floor | Pakistan

PLOT	3,129.1 sq ft (290.7 m2)
MARLA	13.9 @ 225 sf 11.5 @ 272.25 sf
LEVELS	Datum +/-0 = road at P1 (highest) Plot & lawn +/-0, GF FFL +0'-6"
FLOOR HT	11'-0" floor to floor, 10'-6" clear
UNITS	Feet-inches; origin = peg P1
REVISION	REV-03 05 OCT 2026

STAIR & ENTRANCE NOTES

1. Stair: RCC waist slab 5", treads 10" + 1" nosing, risers 6.95", width 3'-6".
2. Riser count: flight-1 = 13 (to landing +7'-6 1/2"), flight-2 = 6 (to FF +11'-0").
3. Landing slab forms the powder ceiling at +7'-1 1/2" clear. Powder door 2'-0" x 6'-9".
4. Glass balustrade 3'-0" high on open side.
5. Flight-2 passes over the entrance foyer; soffit is 7'-1 1/2" at the powder wall and rises to 10'-6" - main door head 7'-0".
6. Porch ramp: broom-finished grooved RCC, drain channel with grating across the gate.
7. Wheel-stop (6" kerb) at the top of the ramp; max car length 15'-0".

SHEET TITLE

STAIR & ENTRANCE
DETAILS

SCALE

PLAN & A-A 1/4"=1'-0"
B-B 3/16"=1'-0"

SHEET NO.

D-102

Ground floor | Pakistan

OTS (OPEN-TO-SKY LIGHT WELL)

1. Clear width 3'-0" measured square to the north boundary, between the 9" lounge wall and the 9" boundary wall.
2. Length on lounge side 18'-7 1/2", on boundary side 18'-7".
3. End widths (N-S): 3'-4 1/2" at grid C, 3'-4" at grid D. Area 58.4 sq ft.
4. Floor: 4" gravel over brick-on-edge with a 4" floor drain; lounge glazing W7 & W8.
5. Dirty kitchen vent V2 opens into the OTS.
6. Kept open through every floor up to the roof.

**OTS DETAIL
(PLAN + SECTION)**

SHEET NO.

D-103

Architectural floor plan of a building section. The plan features a light blue area labeled "OTS (OPEN TO SKY)" with a dimension of 58 SQ.FT. and a dark grey area labeled "FAMILY LOUNGE + DINING" with a dimension of 349 SQ.FT. (NET). The plan includes various dimensions, room labels (V2, W7, W8), and a red circle labeled "P5". A north arrow is present in the bottom right corner.

Key features and dimensions:

- OTS (OPEN TO SKY):** 58 SQ.FT. (Light blue area)
- FAMILY LOUNGE + DINING:** 349 SQ.FT. (NET) (Dark grey area)
- Dimensions:**
 - 17'-11"
 - 3'-0"
 - 3'-0"
 - 3'-4 1/2"
 - 18'-7 1/2"
 - W7 4'-6"
 - W8 3'-4 1/2"
 - 3'-4"
- Room Labels:** V2, W7, W8
- Other Labels:** P5, D12, D13
- North Arrow:** UP

ROOM SCHEDULE - GROUND FLOOR

SPACE	CLEAR SIZE	SQ.FT	FLOOR
DRAWING ROOM	15'-0" x 16'-0"	240.0	WOOD
BED ROOM-2	13'-9" x 16'-0"	220.0	WOOD
DRESS (BED-2)	5'-3" x 8'-7 1/2"	45.3	TILE
BATH (BED-2)	5'-3" x 7'-0"	36.8	WET
LOUNGE + DINING	irregular	348.9	TILE
KITCHEN	13'-9" x 8'-1 1/2"	111.7	WET
DIRTY KITCHEN	13'-5" x 7'-6 1/2"	53.0	WET
PASSAGE 4'-0" WIDE	14'-6" x 4'-0"	58.0	TILE
POWDER	irregular	37.8	WET
DRESS (DRAWING)	5'-3" x 7'-7 1/2"	40.0	TILE
BATH (DRAWING)	6'-0" x 7'-7 1/2"	45.8	WET
BED-1	15'-0" x 15'-0"	225.0	WOOD
DRESSING (BED-1)	7'-1 1/2" x 9'-2 1/2"	55.4	TILE
WASHROOM (BED-1)	7'-6" x 12'-5"	81.7	WET
CAR PORCH	11'-3" x 19'-9"	222.2	PAVER
OTS (OPEN TO SKY)	irregular	58.4	GRAVEL
TOTAL NET CARPET AREA		1599.3	
TOTAL COVERED AREA (WITH WALLS, PORCH)		2078.4	
GROUND COVERAGE		66.4 %	
MAIN LAWN		651.5	GRASS

COLUMN SCHEDULE

MARK	GRID / LOCATION	SIZE	18" ALONG	CENTRE X,Y (FT)
C1	B / 1	9" x 18"	E-W	(36.88, 3.38)
C2	C / 1	9" x 18"	E-W	(51.00, 3.38)
C3	C' / 1	9" x 18"	N-S	(57.00, 3.75)
C4	D / 1	9" x 18"	N-S	(69.00, 3.75)
C5	E / 1	9" x 18"	E-W	(84.38, 3.38)
C6	B / 2	9" x 18"	E-W	(36.88, 20.12)
C7	C / 2	9" x 18"	E-W	(51.00, 20.12)
C8	C' / 2	9" x 18"	E-W	(57.00, 20.12)
C9	D / 2	9" x 18"	E-W	(69.00, 20.12)
C10	E / 2	9" x 18"	E-W	(84.38, 20.12)
C11	D / 3	9" x 18"	E-W	(69.38, 28.50)
C12	D / 5	9" x 18"	N-S	(69.00, 44.06)
C13	E / 3	9" x 18"	E-W	(84.38, 28.50)
C14	E / 5	9" x 18"	N-S	(84.75, 44.06)
C15	B / 4	9" x 18"	N-S	(36.50, 32.81)
C16	C / 4	9" x 18"	N-S	(51.00, 33.19)
C17	C / boundary wall	9" x 18"	E-W	(51.00, 41.54)
C18	C' / 5	9" x 18"	E-W	(57.00, 44.68)
C19	D / boundary wall	9" x 18"	E-W	(69.00, 50.82)
C20	E / boundary wall	9" x 18"	E-W	(84.29, 57.04)
C21	C' / boundary wall	9" x 18"	E-W	(57.00, 40.45)
C22	B+4'-9 1/2" / boundary wall	9" x 18"	E-W	(41.29, 36.49)

DAATA HAMLET
RESIDENCE

Ground floor | Pakistan

PLOT	3,129.1 sq ft (290.7 m2)
MARLA	13.9 @ 225 sf 11.5 @ 272.25 sf
LEVELS	Datum +/-0 = road at P1 (highest) Plot & lawn +/-0, GF FFL +0'-6"
FLOOR HT	11'-0" floor to floor, 10'-6" clear
UNITS	Feet-inches; origin = peg P1
REVISION	REV-03 05 OCT 2026

FINISH KEY

- WOOD = engineered wood / laminate
- TILE = 24"x24" porcelain
- WET = anti-skid ceramic + waterproofing
- PAVER = grooved RCC / exterior pavers

CEILINGS

- 10'-6" clear unless noted. Powder west
- half 7'-1 1/2" (under stair landing).

SHEET TITLE

ROOM & COLUMN
SCHEDULES

SCALE

N.T.S.

SHEET NO.

D-104