


DOOR SCHEDULE

TAG	TYPE	SIZE W x H	FROM → TO	LEAF OPENS
D1	DT-0 6'-0" DOUBLE	6'-0" x 7'-0"	Car porch landing ↔ Foyer	both leaves out to landing
D2	DT-1 3'-6"	3'-6" x 7'-0"	Passage 4'-0" Wide → Bed Room-2	into Bed Room-2
D4	DT-2P 2'-6" POCKET	2'-6" x 7'-0"	Dress ↔ Bed Room-2	slides into wall
D3	DT-3 2'-0"	2'-0" x 7'-0"	Dress → Bath	into Bath
D5	DT-1 3'-6"	3'-6" x 7'-0"	Lawn → Passage 4'-0" Wide	into Passage 4'-0" Wide
D6	DT-1 3'-6"	3'-6" x 7'-0"	Passage 4'-0" Wide → Kitchen	into Kitchen
D7	DT-1 3'-6"	3'-6" x 7'-0"	Kitchen → Dirty Kitchen	into Dirty Kitchen
D8	DT-1 3'-6"	3'-6" x 7'-0"	Guest Lobby → Lounge	into Lounge
D9	DT-2P 2'-6" POCKET	3'-6" x 7'-0"	Car Porch ↔ Drawing Room	slides into wall
D10	DT-2P 2'-6" POCKET	3'-6" x 7'-0"	Drawing Room ↔ Guest Lobby	slides into wall
D11	DT-3 2'-0"	2'-0" x 7'-0"	Guest Lobby → Guest Washroom	into Guest Washroom
D12	DT-2P 2'-6" POCKET	2'-6" x 7'-0"	Guest Lobby ↔ Guest Store	slides into wall
D13	DT-1 3'-6"	3'-6" x 7'-0"	Bed-1 → Lounge	into Lounge
D14	DT-2S 2'-6" SLIDING	2'-6" x 7'-0"	Bed-1 ↔ Dressing	slides on room face
D15	DT-3 2'-0"	2'-0" x 7'-0"	Washroom → Dressing	into Dressing


WINDOW & VENTILATOR SCHEDULE

TAG	SIZE W x H	SILL	HEAD	ROOM	OPENS TO	TYPE
W9	1'-6" x 6'-0"	1'-0"	7'-0"	Lounge	car porch	window
W10	1'-6" x 6'-0"	1'-0"	7'-0"	Lounge	car porch	window
SL1	8'-0" x 7'-0"	0'-0"	7'-0"	Bed Room-2	open air	sliding
W1	7'-0" x 4'-6"	2'-6"	7'-0"	Bed Room-2	open air	window
V1	2'-0" x 1'-0"	6'-0"	7'-0"	Bath	open air	vent
W2	5'-0" x 3'-6"	3'-6"	7'-0"	Kitchen	open air	window
V2	1'-6" x 1'-6"	5'-0"	6'-6"	Dirty Kitchen	OTS	vent
W3	7'-0" x 4'-6"	2'-6"	7'-0"	Drawing Room	open air	window
W4	5'-0" x 4'-0"	3'-0"	7'-0"	Drawing Room	open air	window
V4	2'-0" x 1'-0"	6'-0"	7'-0"	Guest Washroom	open air	vent
W5	5'-6" x 4'-0"	3'-0"	7'-0"	Bed-1	open air	window
W6	3'-0" x 2'-0"	5'-0"	7'-0"	Washroom	open air	vent
W7	4'-6" x 4'-0"	3'-0"	7'-0"	Lounge	OTS	window
W8	3'-4 1/2" x 4'-0"	3'-0"	7'-0"	Lounge	OTS	window

DOOR TYPES

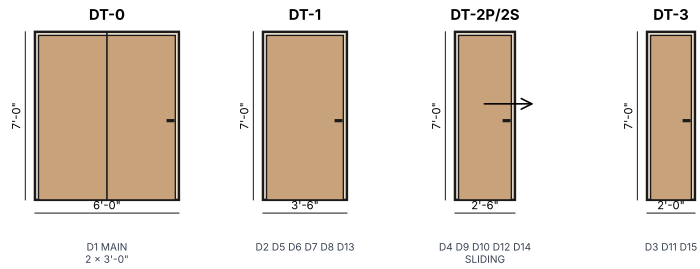

WINDOW & VENT TYPES (HEIGHTS FROM FFL)

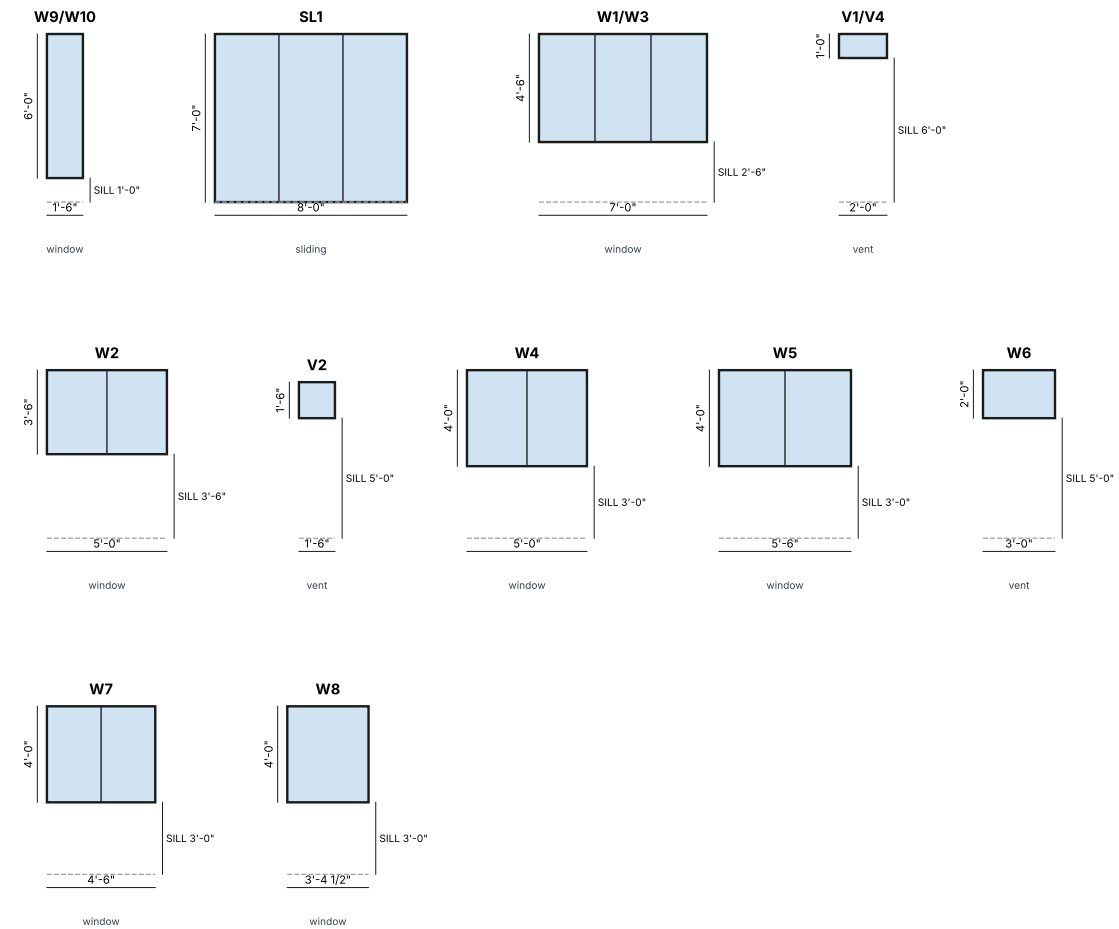

DAATA HAMLET RESIDENCE

Ground floor | Pakistan

PLOT	3,129.1 sq ft (290.7 m2)
MARLA	13.9 @ 225 sf 11.5 @ 272.25 sf
LEVELS	Datum +/-0 = road at P1 (highest) Plot & lawn +/-0, GF FFL +0'-6"
FLOOR HT	11'-0" floor to floor, 10'-6" clear
UNITS	Feet-inches; origin = peg P1
REVISION	REV-04 05 OCT 2026
OPTION	L-TYPE STAIR (OPTION 1)

DOOR & WINDOW NOTES

- Door heights 7'-0". Frames 2"x5" seasoned wood.
- Main door D1: 6'-0" double teak (2 × 3'-0"), centred on the porch, opens out to the landing.
- Room doors 3'-6" solid-core flush; baths 2'-0" WPC (water-proof).
- Pocket sliding doors in 9" walls: D4 (dress), D9 & D10 (drawing room, 3'-6"), D12 (store). D14 (Bed-1 dressing) on a top track. All wardrobes have sliding shutters.
- Lawn door D5 opens INWARD into the passage.
- Swing leaves hinge on the corner side and park flat against the adjoining wall.
- Windows: aluminium, 5mm tinted glass, MS safety grill inside. Vents: frosted louvres.
- W9 is a fixed glazed sidelight to the door.
- Sill / head heights are above the GF FFL.

SHEET TITLE

DOOR & WINDOW SCHEDULE + TYPES


SCALE

1/8" = 1'-0" (TYPES)

SHEET NO.


D-101

ENLARGED PLAN : L-TYPE STAIR (OPTION 1), LOBBY & ENTRANCE (1/4"=1'-0")

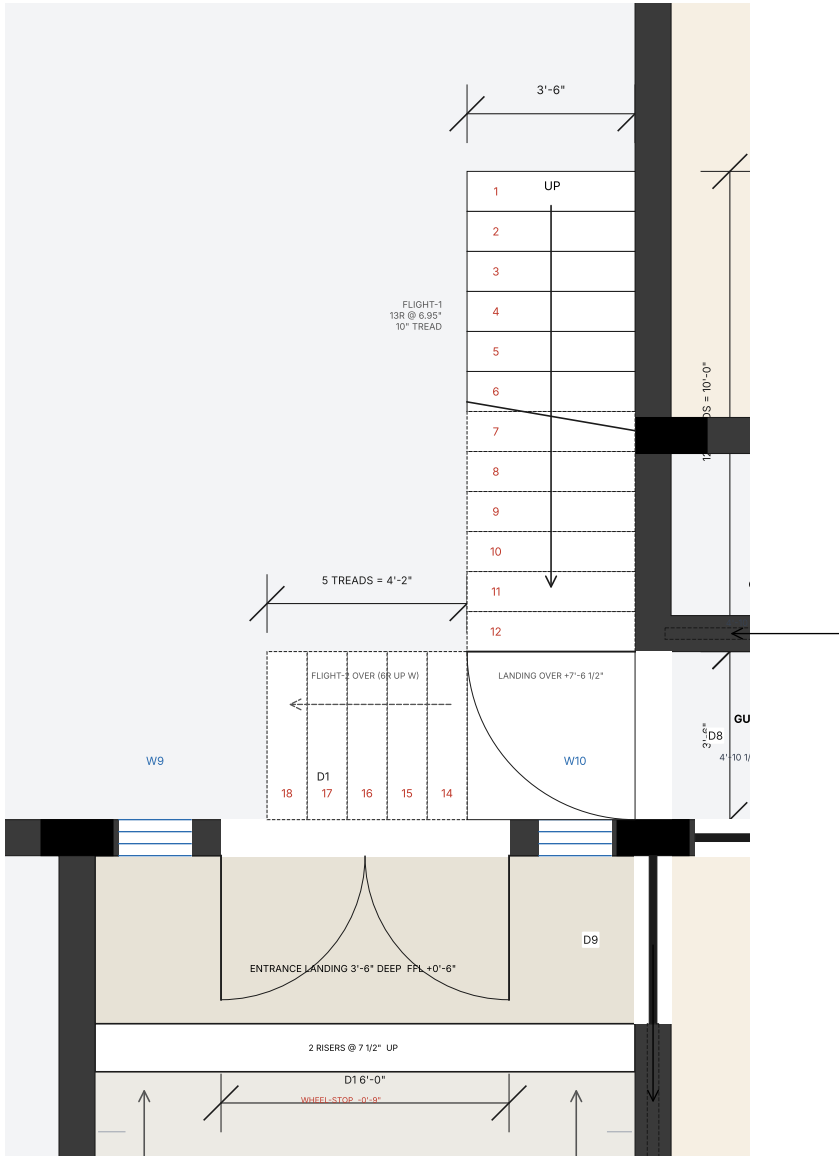


SECTION A-A : STAIR (L-TYPE) + GUEST LOBBY - LOOKING EAST

NORTH (LOUNGE) ← → SOUTH (ENTRANCE) | 19 RISERS @ 6.95" TREAD 10" WIDTH 3'-6"

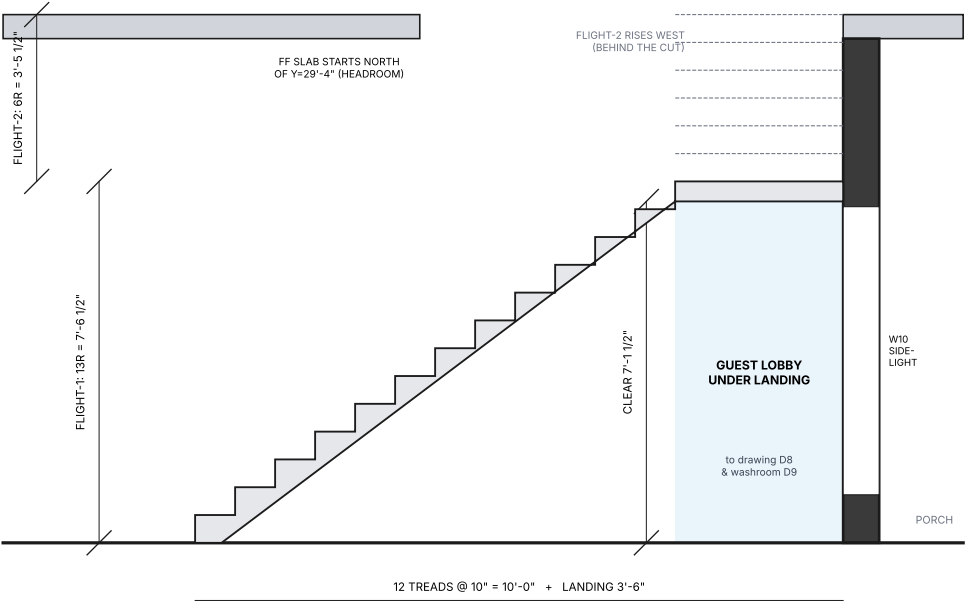

SECTION B-B : CAR PORCH RAMP & ENTRANCE

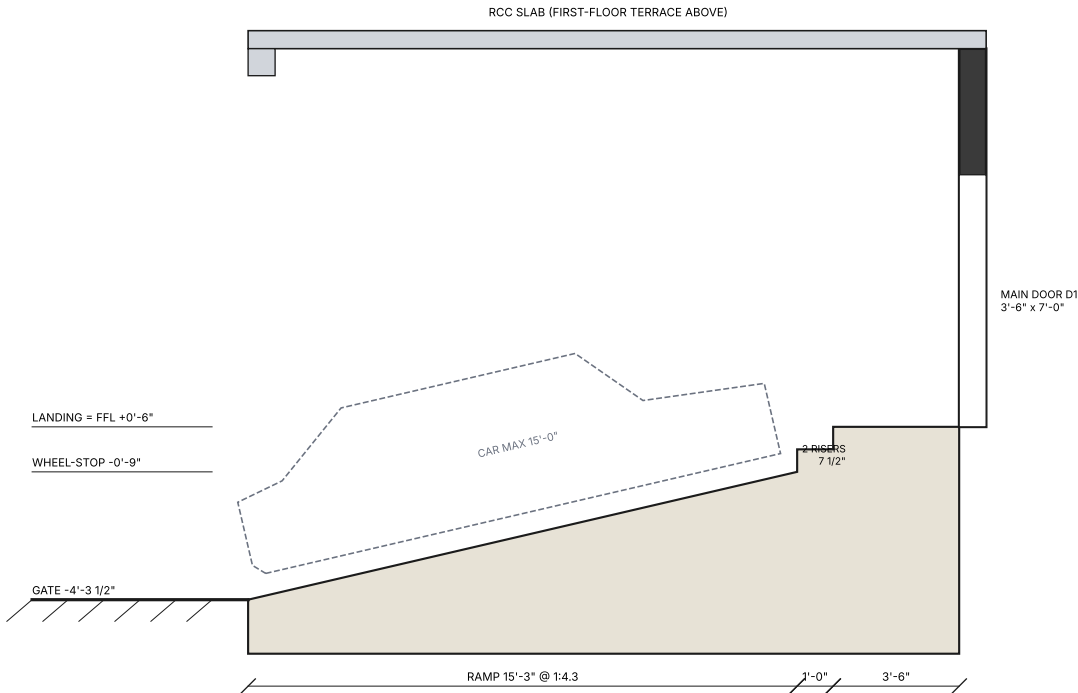

DAATA HAMLET
RESIDENCE

Ground floor | Pakistan

PLOT	3,129.1 sq ft (290.7 m2)
MARLA	13.9 @ 225 sf 11.5 @ 272.25 sf
LEVELS	Datum +/-0 = road at P1 (highest) Plot & lawn +/-0, GF FFL +0'-6"
FLOOR HT	11'-0" floor to floor, 10'-6" clear
UNITS	Feet-inches; origin = peg P1
REVISION	REV-04 05 OCT 2026
OPTION	L-TYPE STAIR (OPTION 1)

STAIR & ENTRANCE NOTES

1. Stair: RCC waist slab 5", treads 10" + 1" nosing, risers 6.95", width 3'-6".
2. Riser count: flight-1 = 13 (to landing +7'-6 1/2"), flight-2 = 6 (to FF +11'-0").
3. Under the landing (7'-1 1/2" clear) is the foyer; door D8 (3'-6") on grid D closes the guest lobby → drawing room D10, washroom D11, store D12. Drawing guest door D9 off the porch.
4. Glass balustrade 3'-0" high on open sides.
5. Flight-2 runs west over the foyer; soffit 7'-1 1/2" rising to 10'-6".
Main door head 7'-0" clears the soffit.
6. Porch ramp: broom-finished grooved RCC, drain channel with grating across the gate.
7. Wheel-stop (6" kerb) at the top of the ramp; max car length 15'-0".

SHEET TITLE

STAIR & ENTRANCE
DETAILS

SCALE

PLAN & A-A 1/4"=1'-0"
B-B 3/16"=1'-0"

SHEET NO.

D-102

DAATA HAMLET
RESIDENCE

Ground floor | Pakistan

PLOT	3,129.1 sq ft (290.7 m2)
MARLA	13.9 @ 225 sf 11.5 @ 272.25 sf
LEVELS	Datum +/-0 = road at P1 (highest) Plot & lawn +/-0, GF FFL +0'-6"
FLOOR HT	11'-0" floor to floor, 10'-6" clear
UNITS	Feet-inches; origin = peg P1
REVISION	REV-04 05 OCT 2026
OPTION	L-TYPE STAIR (OPTION 1)

INTERIOR ELEVATIONS (TRUE VIEW)

- B-B is what you see standing in the foyer
facing the entrance (south): the drawing
room & lobby are on your LEFT, the passage
on your RIGHT.
- C-C is the view from the foyer into the
guest lobby (east): drawing room door on the
right-hand wall, guest washroom ahead.
- The foyer under the landing is 7'-1 1/2" high;
the closed guest lobby behind D8 is 10'-6".
- Doors: D1 6'-0" (2 x 3'-0"), D8 lobby 3'-6",
D10 drawing 3'-6" pocket, D11 washroom 2'-0",
D12 store 2'-6" pocket.

SHEET TITLE

INTERIOR ELEVATIONS
ENTRANCE & LOBBY

SCALE


1/4" = 1'-0"

SHEET NO.

D-102B


INTERIOR ELEVATION B-B (L-STAIR) : FROM THE FOYER LOOKING SOUTH

TRUE VIEW - EAST (DRAWING / LOBBY) ON YOUR LEFT, WEST (PASSAGE) ON YOUR RIGHT

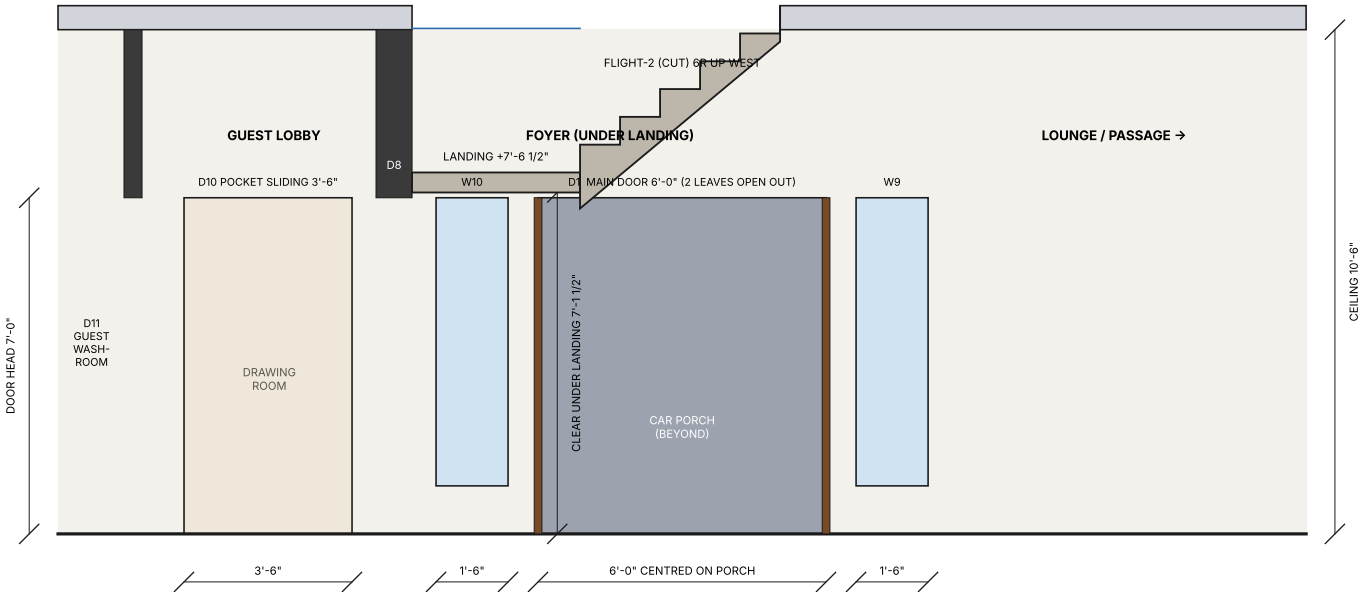

INTERIOR ELEVATION C-C (L-STAIR) : FROM THE FOYER LOOKING EAST INTO THE GUEST LOBBY

NORTH (LOUNGE) ON YOUR LEFT, SOUTH (ENTRANCE) ON YOUR RIGHT

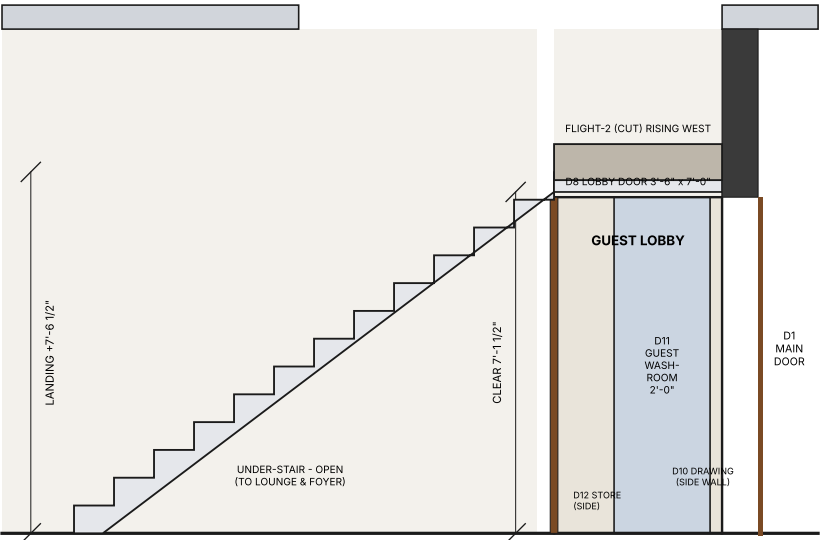

DAATA HAMLET
RESIDENCE

Ground floor | Pakistan


PLOT	3,129.1 sq ft (290.7 m2)
MARLA	13.9 @ 225 sf 11.5 @ 272.25 sf
LEVELS	Datum +/-0 = road at P1 (highest) Plot & lawn +/-0, GF FFL +0'-6"
FLOOR HT	11'-0" floor to floor, 10'-6" clear
UNITS	Feet-inches; origin = peg P1
REVISION	REV-04 05 OCT 2026
OPTION	L-TYPE STAIR (OPTION 1)

3D VIEWS


L-TYPE STAIR (OPTION 1)

Rendered from the 3D model built from the same dimensions as these drawings. Walls are cut at ceiling height so the stair, landing and the space beneath are fully visible.


FROM THE LOUNGE LOOKING SOUTH - stair, landing and the entrance beneath

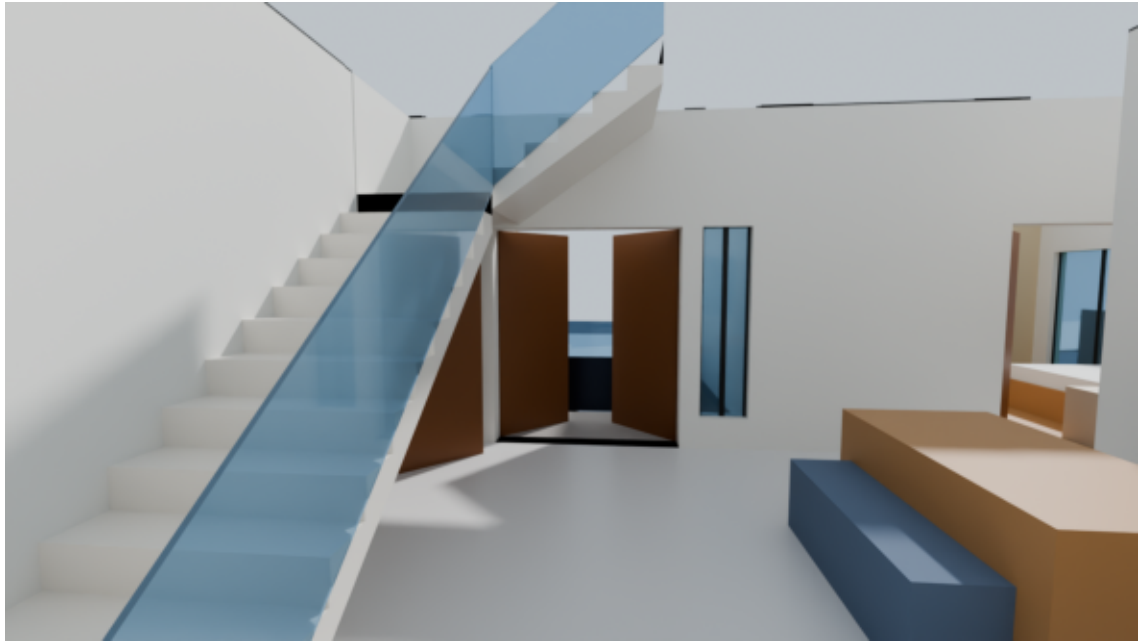


FROM THE FOYER LOOKING EAST - lobby door D8 (open), drawing door & washroom beyond

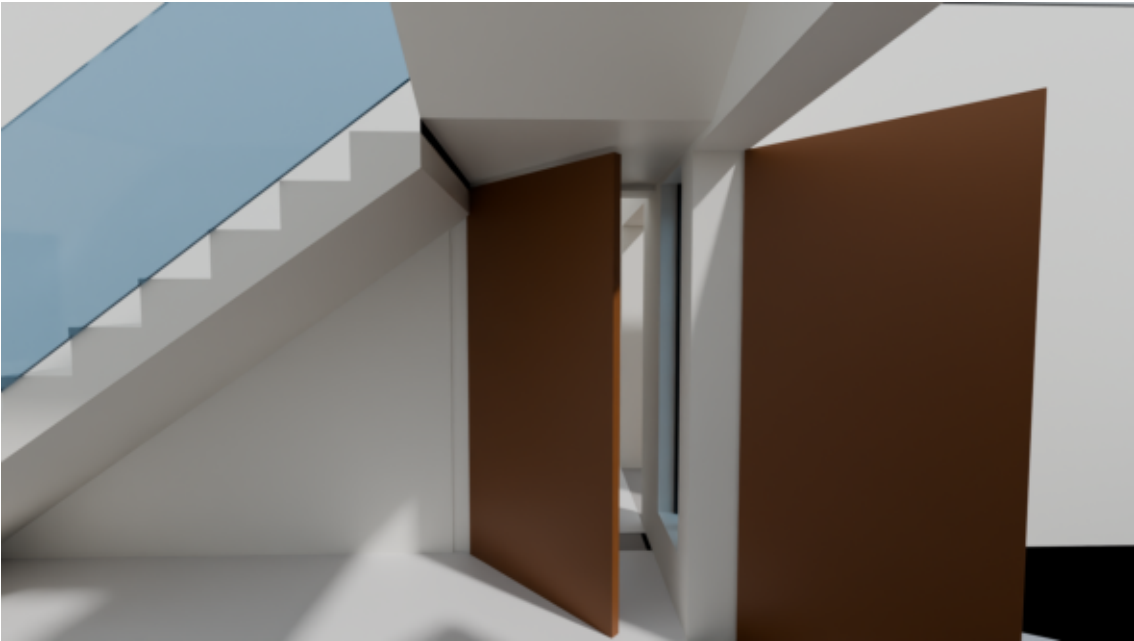

FROM THE DINING AREA - stair profile and open space under the flights

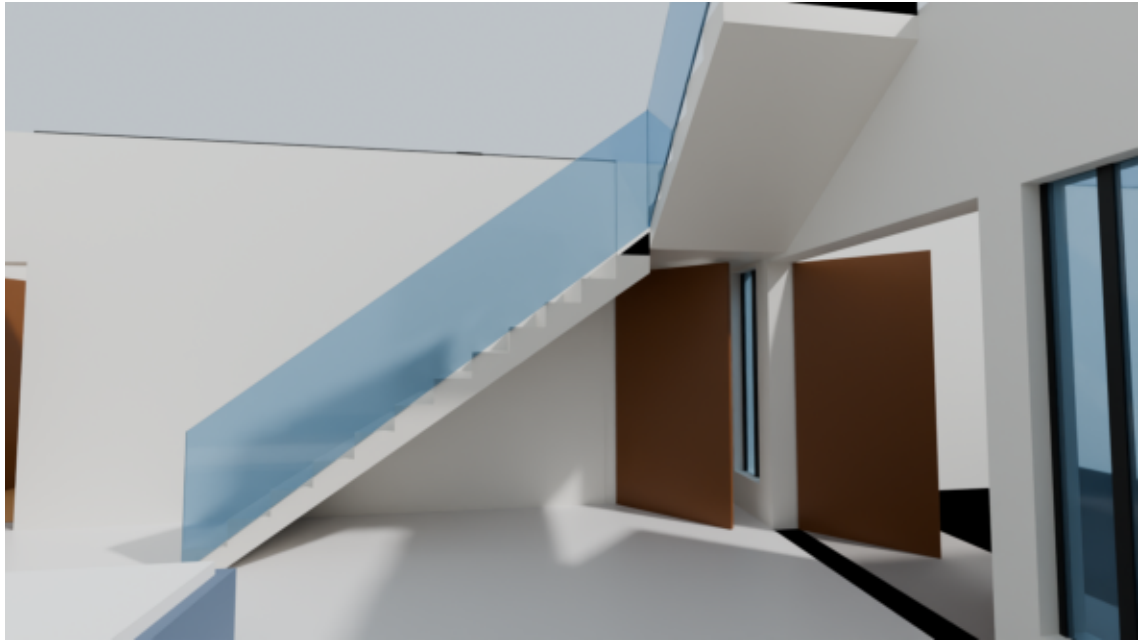

FROM THE CAR PORCH - 6'-0" main door centred, sidelights W9 / W10

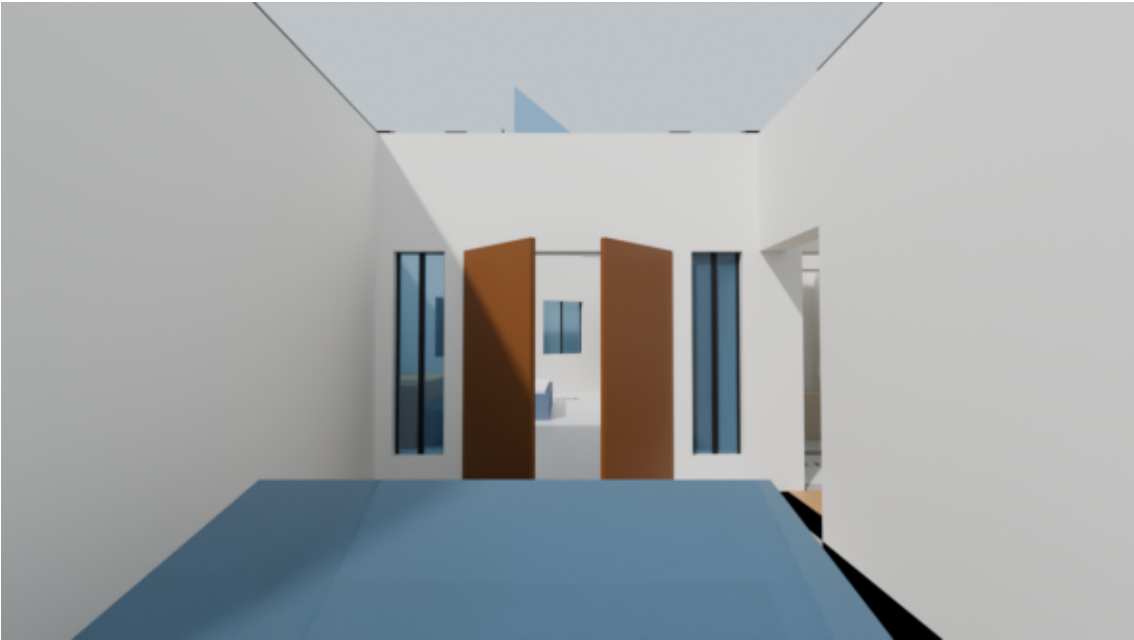

SHEET TITLE

3D VIEWS
STAIR & ENTRANCE

SCALE

N.T.S.

SHEET NO.

D-105


DAATA HAMLET
RESIDENCE

Ground floor | Pakistan


PLOT	3,129.1 sq ft (290.7 m2)
MARLA	13.9 @ 225 sf 11.5 @ 272.25 sf
LEVELS	Datum +/-0 = road at P1 (highest) Plot & lawn +/-0, GF FFL +0'-6"
FLOOR HT	11'-0" floor to floor, 10'-6" clear
UNITS	Feet-inches; origin = peg P1
REVISION	REV-04 05 OCT 2026
OPTION	L-TYPE STAIR (OPTION 1)

- OTS (OPEN-TO-SKY LIGHT WELL)**
- Clear width 3'-0" measured square to the north boundary, between the 9" lounge wall and the 9" boundary wall.
 - Length on lounge side 18'-7 1/2", on boundary side 18'-7".
 - End widths (N-S): 3'-4 1/2" at grid C, 3'-4" at grid D. Area 58.4 sq ft.
 - Floor: 4" gravel over brick-on-edge with a 4" floor drain; lounge glazing W7 & W8.
 - Dirty kitchen vent V2 opens into the OTS.
 - Kept open through every floor up to the roof.

SECTION C-C : OTS (LIGHT WELL)

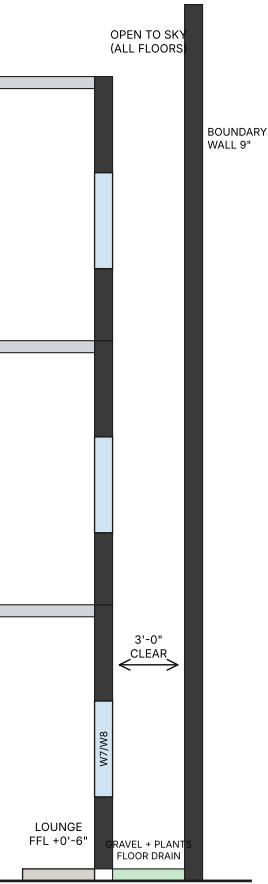

ENLARGED PLAN : OTS (3/8"=1'-0")

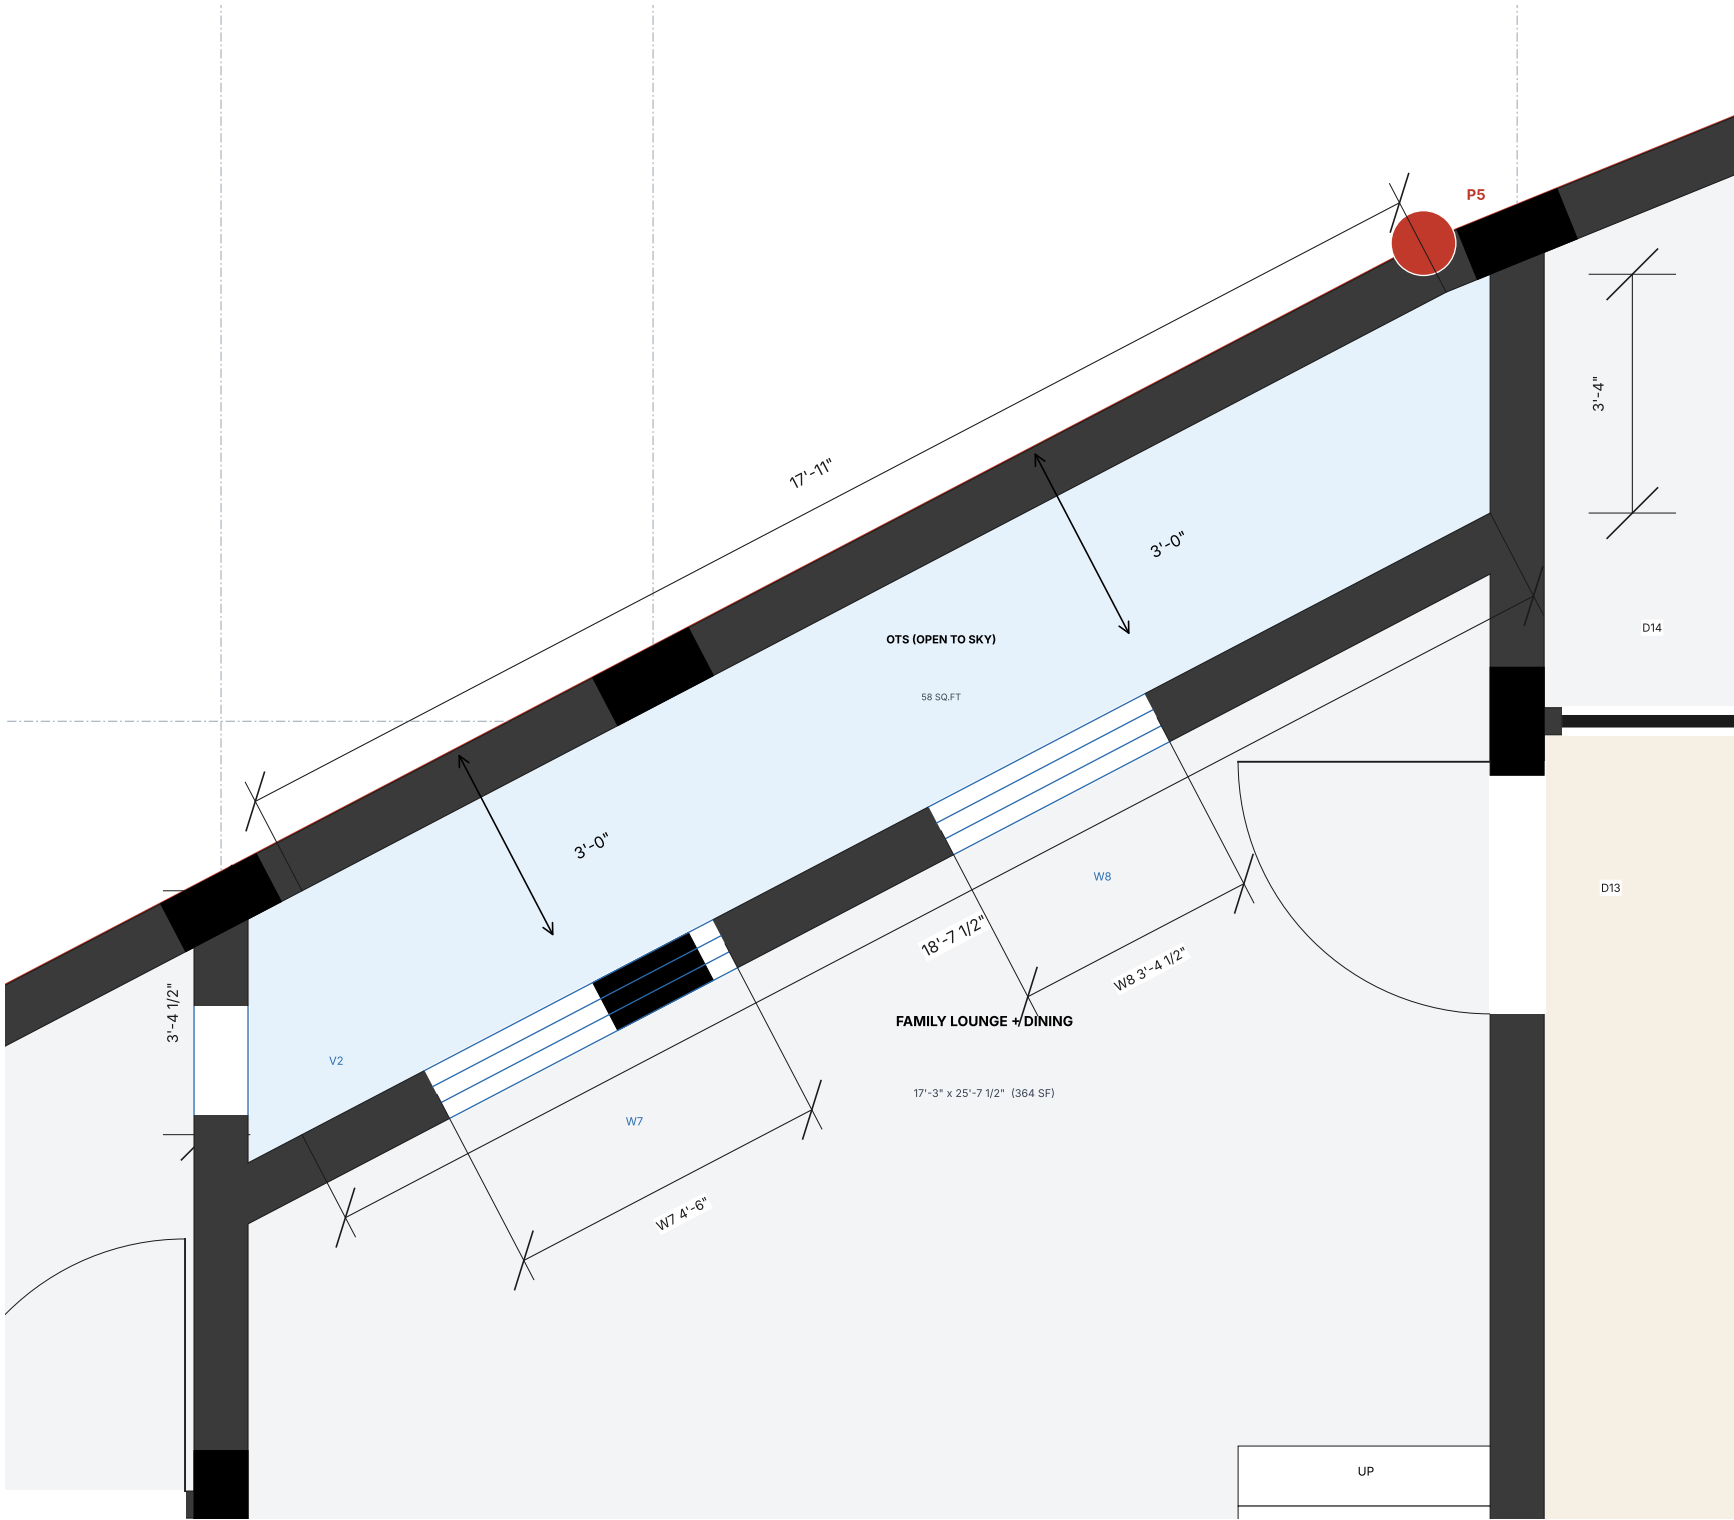

SHEET TITLE

OTS DETAIL
(PLAN + SECTION)

SCALE

PLAN 3/8"=1'-0"
SECTION 1/8"=1'-0"

SHEET NO.

D-103

ROOM SCHEDULE - GROUND FLOOR

SPACE	CLEAR SIZE	SQ.FT	FLOOR
DRAWING ROOM	15'-0" x 16'-0"	240.0	WOOD
BED ROOM-2	13'-9" x 16'-0"	220.0	WOOD
DRESS (BED-2)	5'-3" x 8'-7 1/2"	45.3	TILE
BATH (BED-2)	5'-3" x 7'-0"	36.8	WET
LOUNGE + DINING	17'-3" x 25'-7 1/2"	363.9	TILE
KITCHEN	13'-9" x 8'-1 1/2"	111.7	WET
DIRTY KITCHEN	13'-5" x 7'-6 1/2"	53.0	WET
PASSAGE 4'-0" WIDE	14'-6" x 4'-0"	58.0	TILE
GUEST LOBBY	4'-10 1/2" x 3'-6"	17.1	TILE
GUEST STORE	4'-10 1/2" x 3'-4 1/2"	16.5	TILE
GUEST WASHROOM	9'-9" x 7'-7 1/2"	74.3	WET
BED-1	15'-0" x 15'-0"	225.0	WOOD
DRESSING (BED-1)	7'-1 1/2" x 9'-2 1/2"	55.4	TILE
WASHROOM (BED-1)	7'-6" x 12'-5"	81.7	WET
CAR PORCH	11'-3" x 19'-9"	222.2	PAVER
OTS (OPEN TO SKY)	irregular	58.4	GRAVEL
TOTAL NET CARPET AREA		1598.6	
TOTAL COVERED AREA (WITH WALLS, PORCH)		2078.4	
GROUND COVERAGE		66.4 %	
MAIN LAWN		651.5	GRASS

COLUMN SCHEDULE

MARK	GRID / LOCATION	SIZE	18" ALONG	CENTRE X,Y (FT)
C1	B / 1	9" x 18"	E-W	(36.88, 3.38)
C2	C / 1	9" x 18"	E-W	(51.00, 3.38)
C3	C' / 1	9" x 18"	N-S	(57.00, 3.75)
C4	D / 1	9" x 18"	N-S	(69.00, 3.75)
C5	E / 1	9" x 18"	E-W	(84.38, 3.38)
C6	B / 2	9" x 18"	E-W	(36.88, 20.12)
C7	C / 2	9" x 18"	E-W	(51.00, 20.12)
C8	C' / 2	9" x 18"	E-W	(57.00, 20.12)
C9	D / 2	9" x 18"	E-W	(69.00, 20.12)
C10	E / 2	9" x 18"	E-W	(84.38, 20.12)
C11	D / 3	9" x 18"	E-W	(69.38, 28.50)
C12	D / 5	9" x 18"	N-S	(69.00, 44.06)
C13	E / 3	9" x 18"	E-W	(84.38, 28.50)
C14	E / 5	9" x 18"	N-S	(84.75, 44.06)
C15	B / 4	9" x 18"	N-S	(36.50, 32.81)
C16	C / 4	9" x 18"	N-S	(51.00, 33.19)
C17	C / boundary wall	9" x 18"	E-W	(51.00, 41.54)
C18	C' / 5	9" x 18"	E-W	(57.00, 44.68)
C19	D / boundary wall	9" x 18"	E-W	(69.00, 50.82)
C20	E / boundary wall	9" x 18"	E-W	(84.29, 57.04)
C21	C' / boundary wall	9" x 18"	E-W	(57.00, 40.45)
C22	B+4'-9 1/2" / boundary wall	9" x 18"	E-W	(41.29, 36.49)

DAATA HAMLET
RESIDENCE

Ground floor | Pakistan

PLOT	3,129.1 sq ft (290.7 m2)
MARLA	13.9 @ 225 sf 11.5 @ 272.25 sf
LEVELS	Datum +/-0 = road at P1 (highest) Plot & lawn +/-0, GF FFL +0'-6"
FLOOR HT	11'-0" floor to floor, 10'-6" clear
UNITS	Feet-inches; origin = peg P1
REVISION	REV-04 05 OCT 2026
OPTION	L-TYPE STAIR (OPTION 1)

FINISH KEY

- WOOD = engineered wood / laminate
- TILE = 24"x24" porcelain
- WET = anti-skid ceramic + waterproofing
- PAVER = grooved RCC / exterior pavers

CEILINGS

- 10'-6" clear unless noted. Powder west
- half 7'-1 1/2" (under stair landing).

SHEET TITLE

ROOM & COLUMN
SCHEDULES

SCALE

N.T.S.

SHEET NO.

D-104