



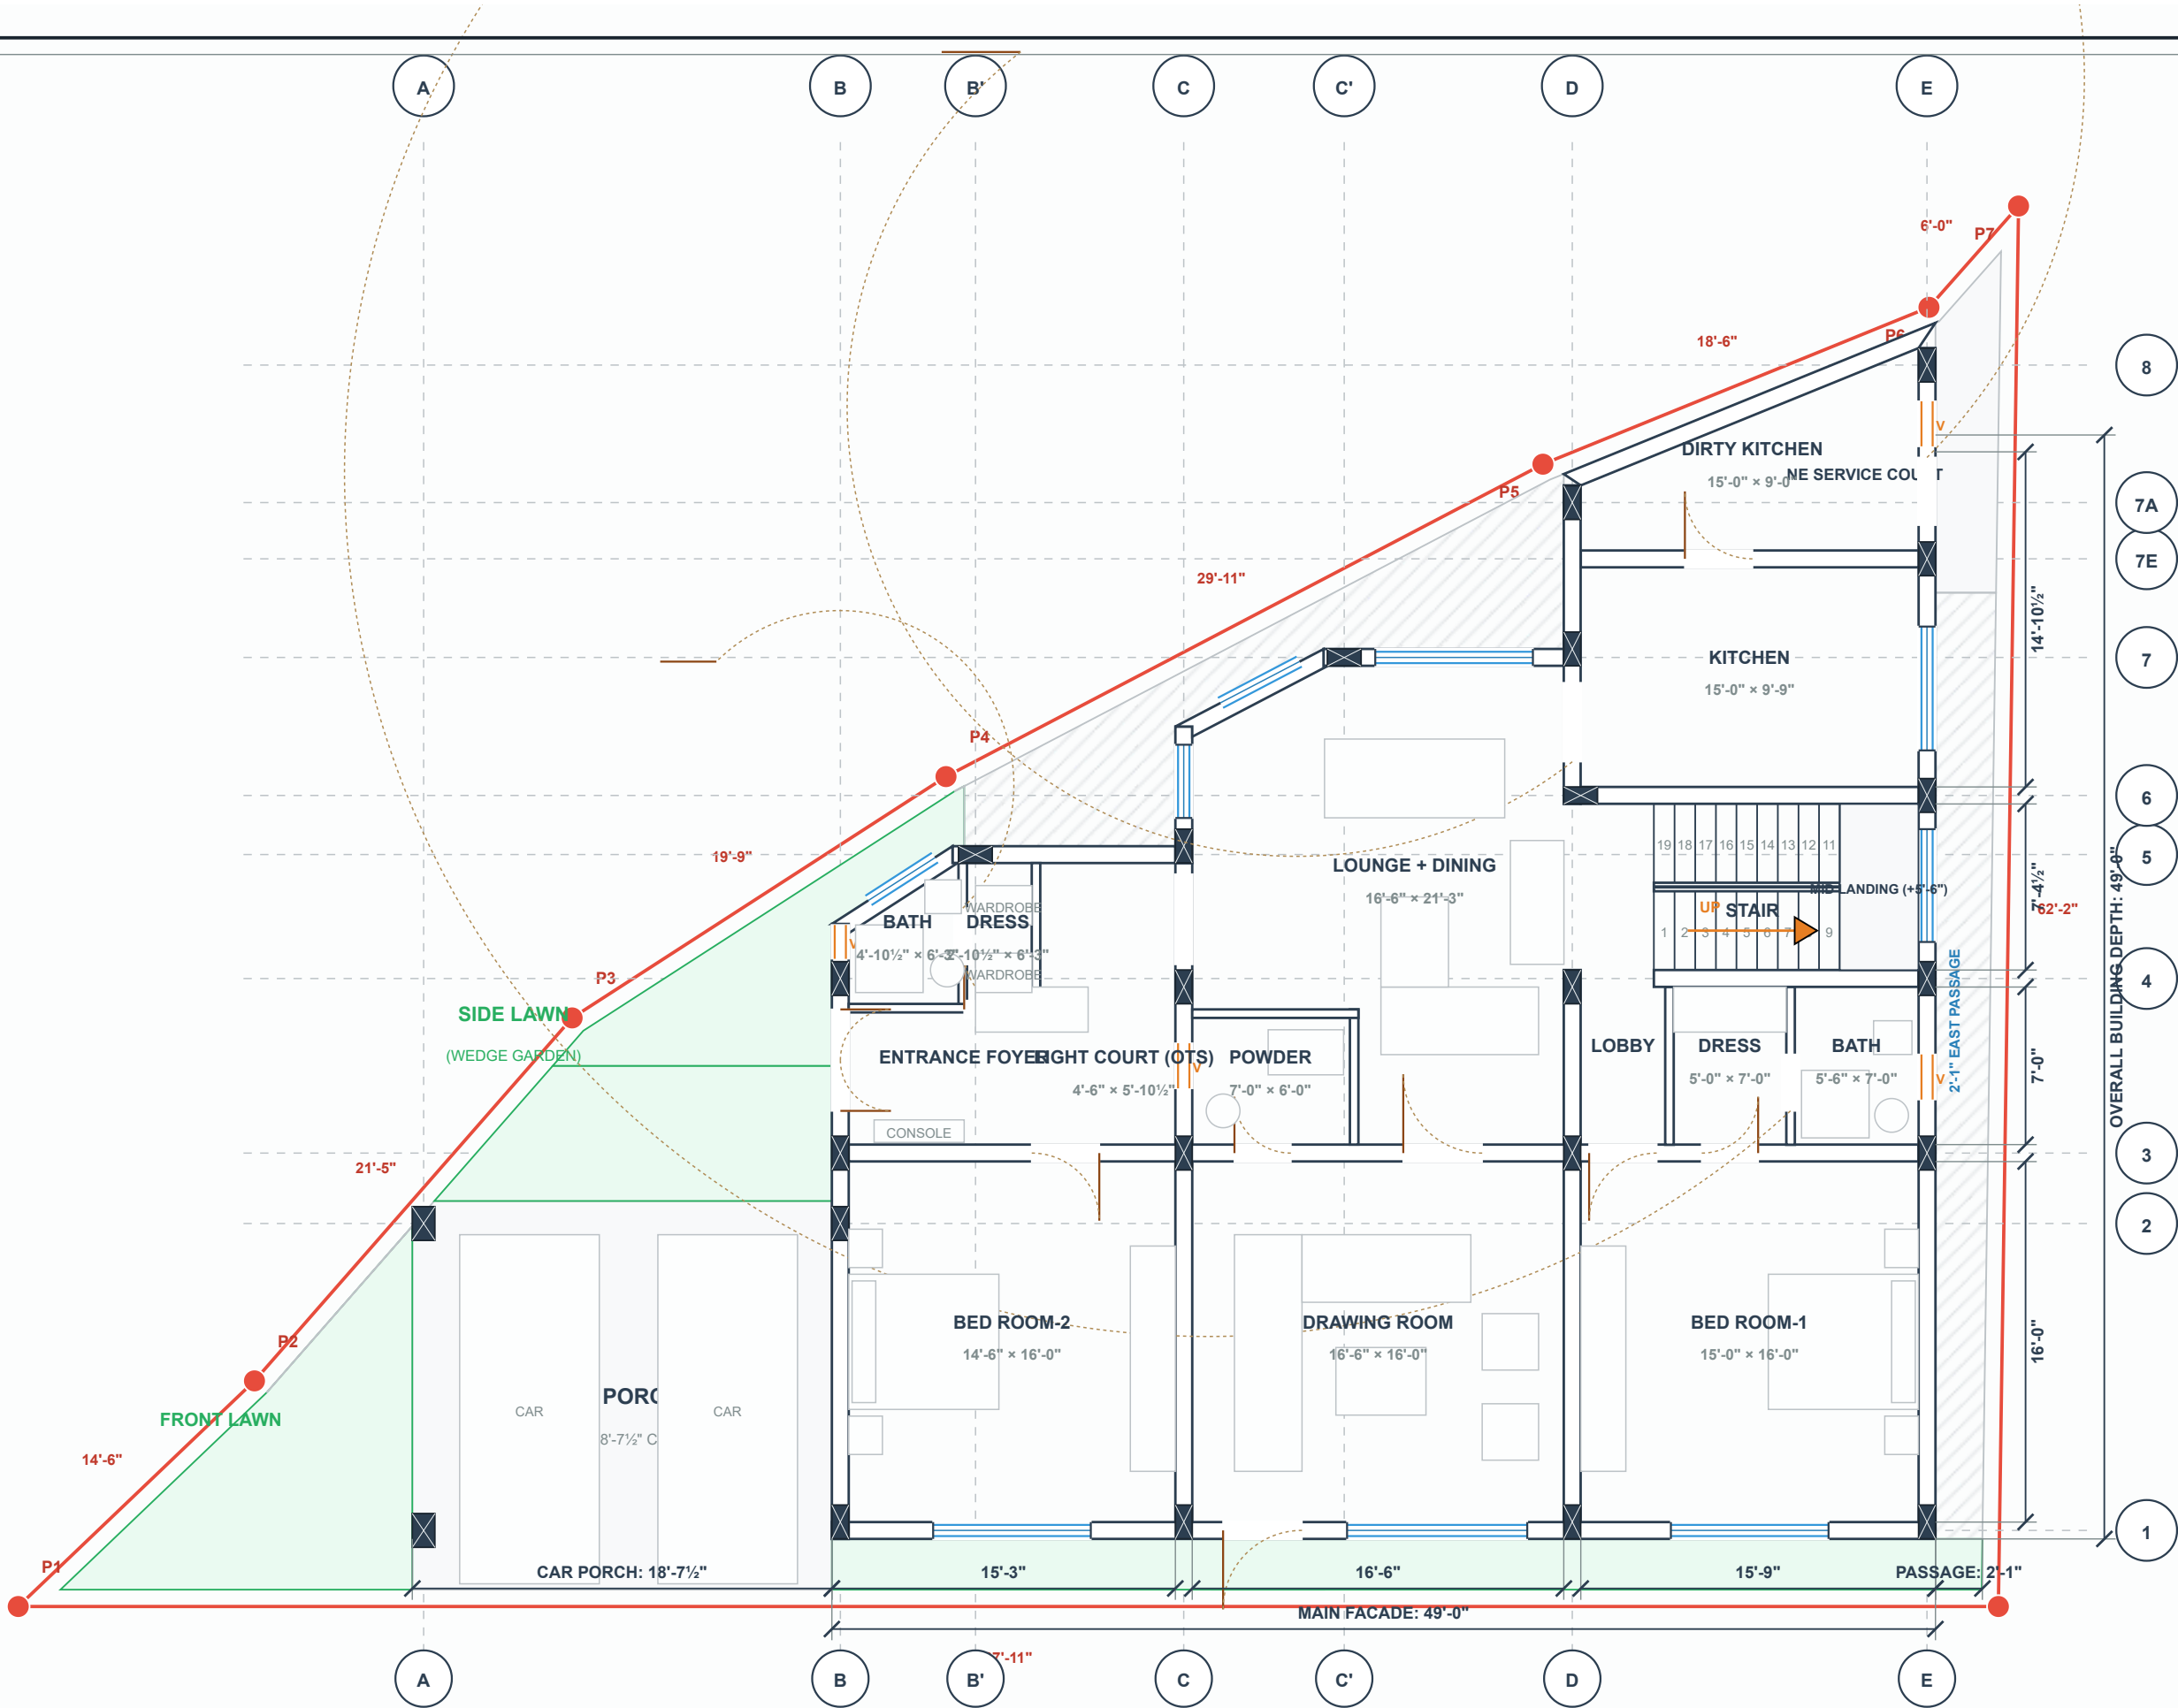


DAATA HAMLET RESIDENCE		PLOT: 3,129.1 SQ.FT.	
DRAWING: GROUND FLOOR ARCHITECTURAL PLAN		SHEET: A-101	
SCALE: 1/8" = 1'-0" STATUS: APPROVED FOR CAD		UNITS: FEET-INCHES	


PUBLIC ACCESS ROAD (87'-11" FRONTAGE)

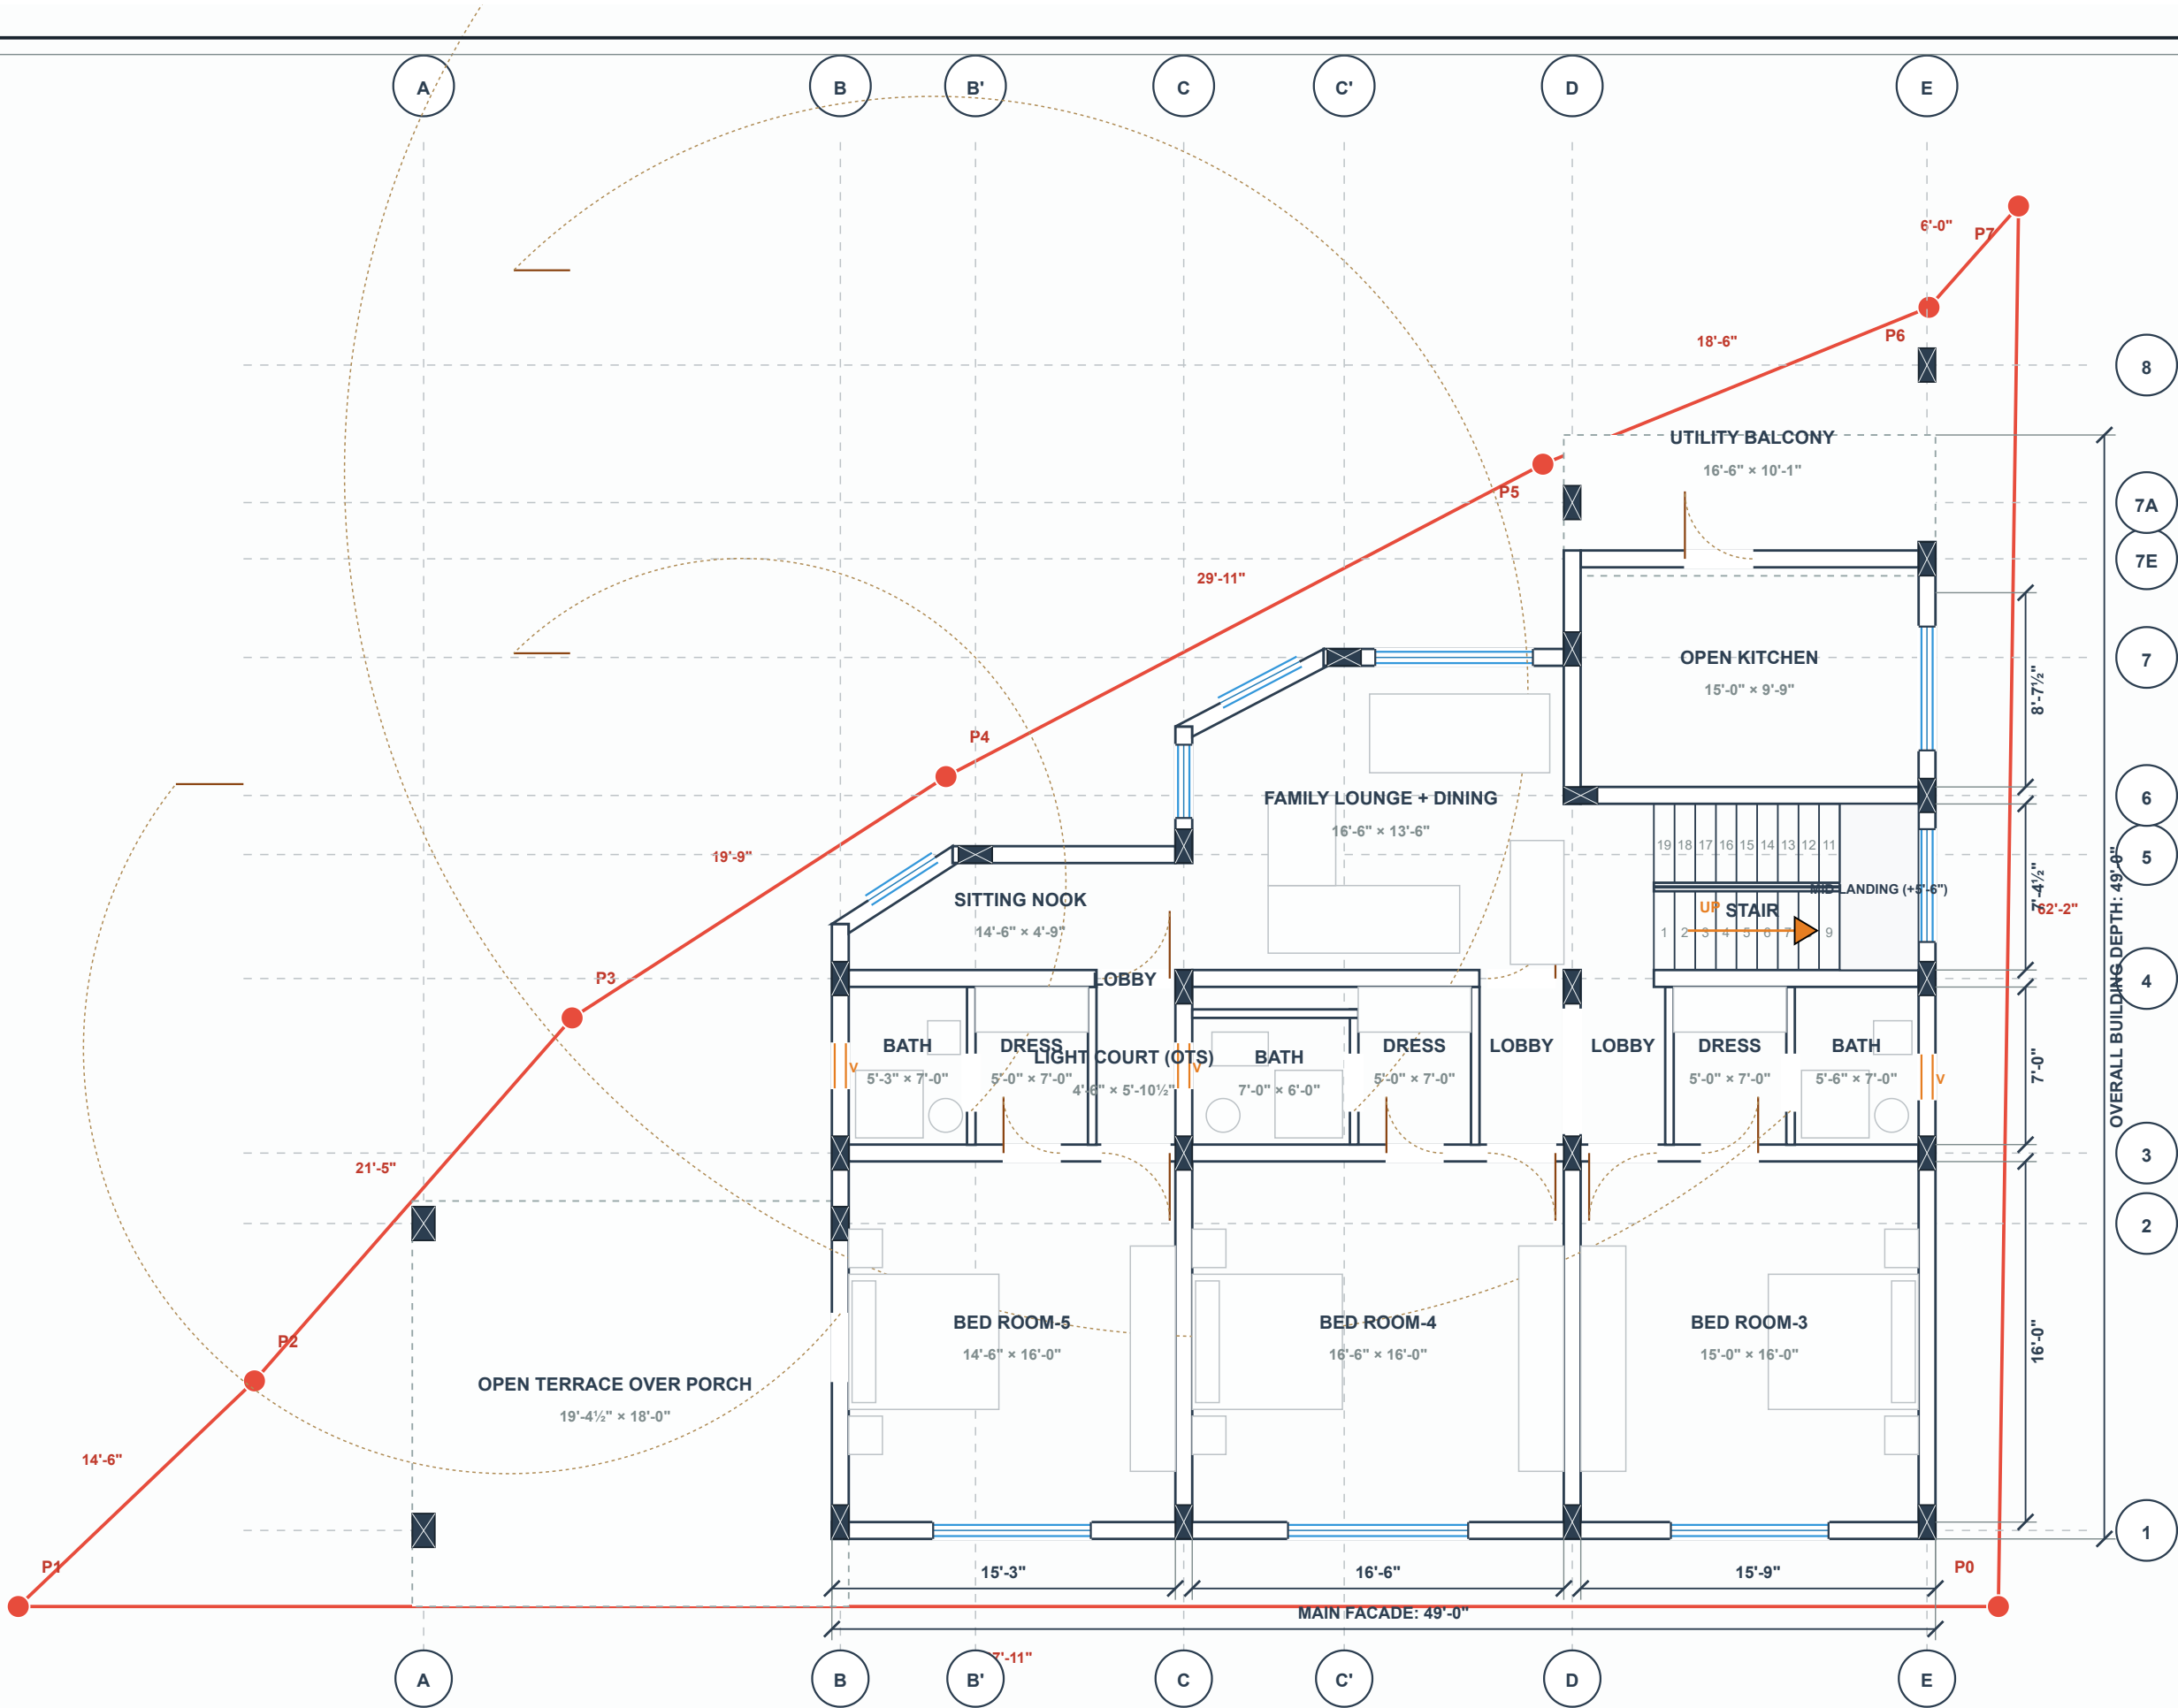

DAATA HAMLET RESIDENCE		PLOT: 3,129.1 SQ.FT.	
DRAWING: FIRST FLOOR ARCHITECTURAL PLAN		SHEET: A-102	
SCALE: 1/8" = 1'-0" STATUS: APPROVED FOR CAD		UNITS: FEET-INCHES	

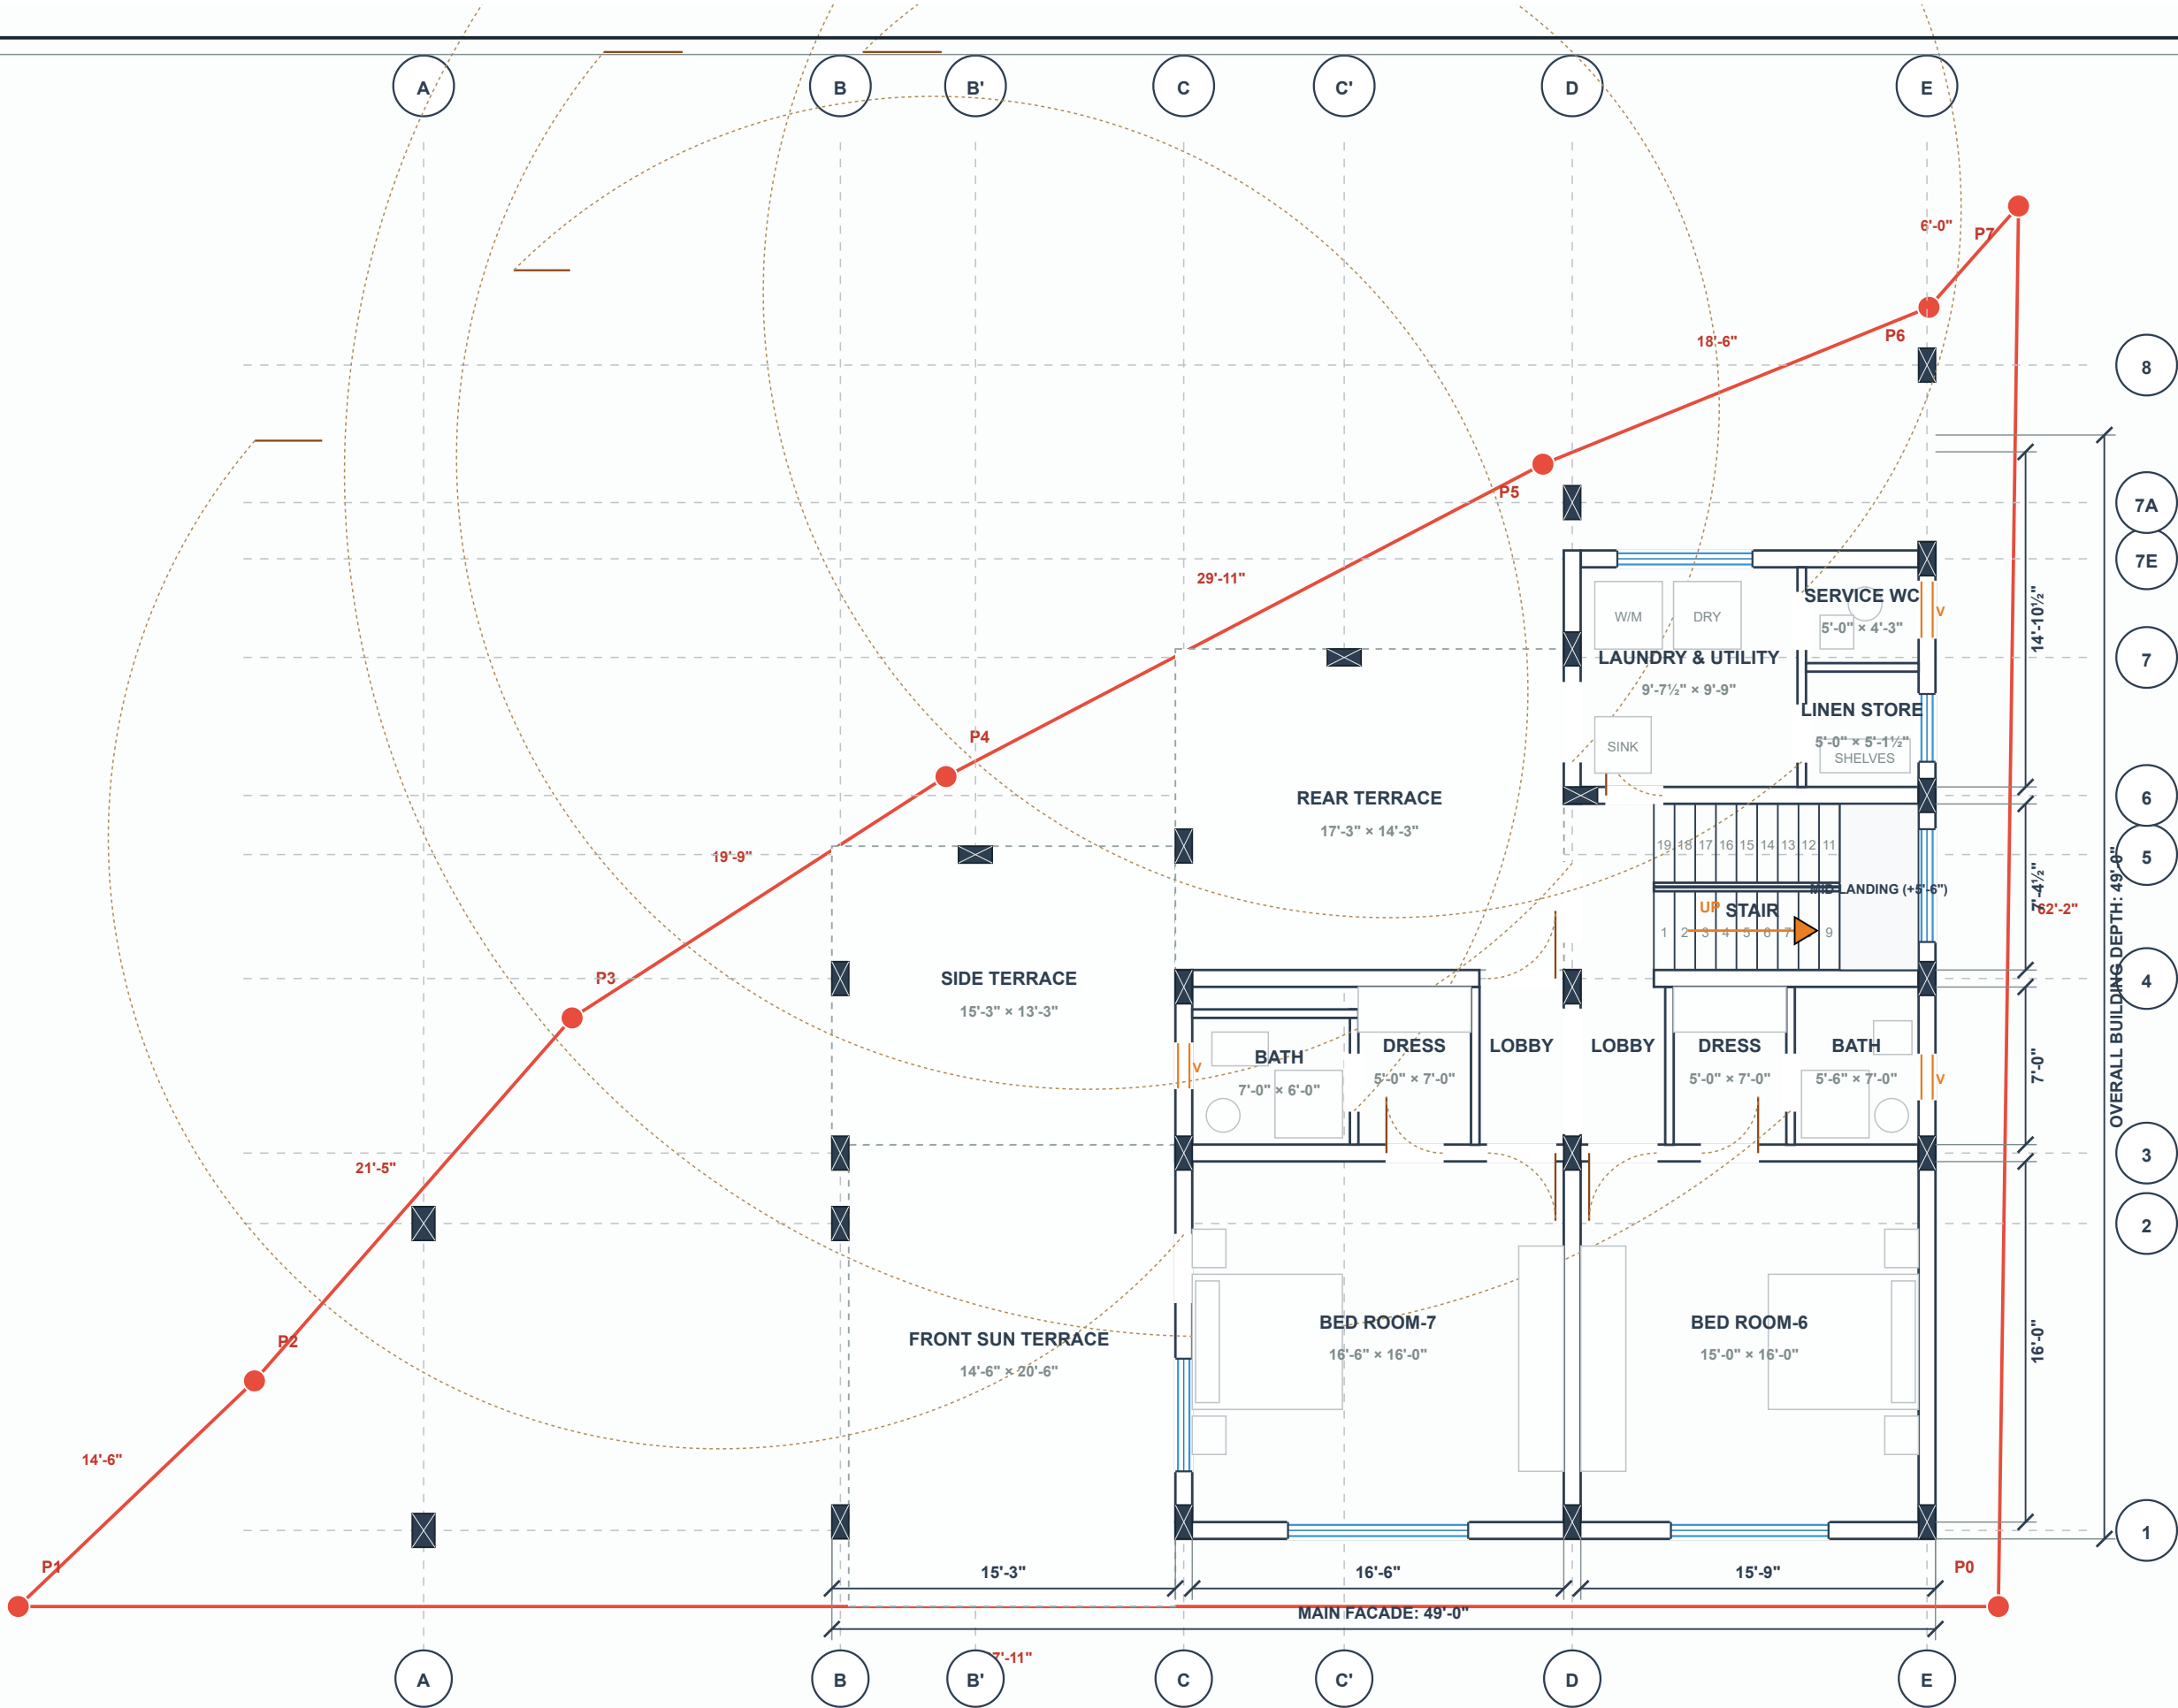


DAATA HAMLET RESIDENCE		PLOT: 3,129.1 SQ.FT.	
DRAWING: SECOND FLOOR ARCHITECTURAL PLAN		SHEET: A-103	
SCALE: 1/8" = 1'-0" STATUS: APPROVED FOR CAD		UNITS: FEET-INCHES	

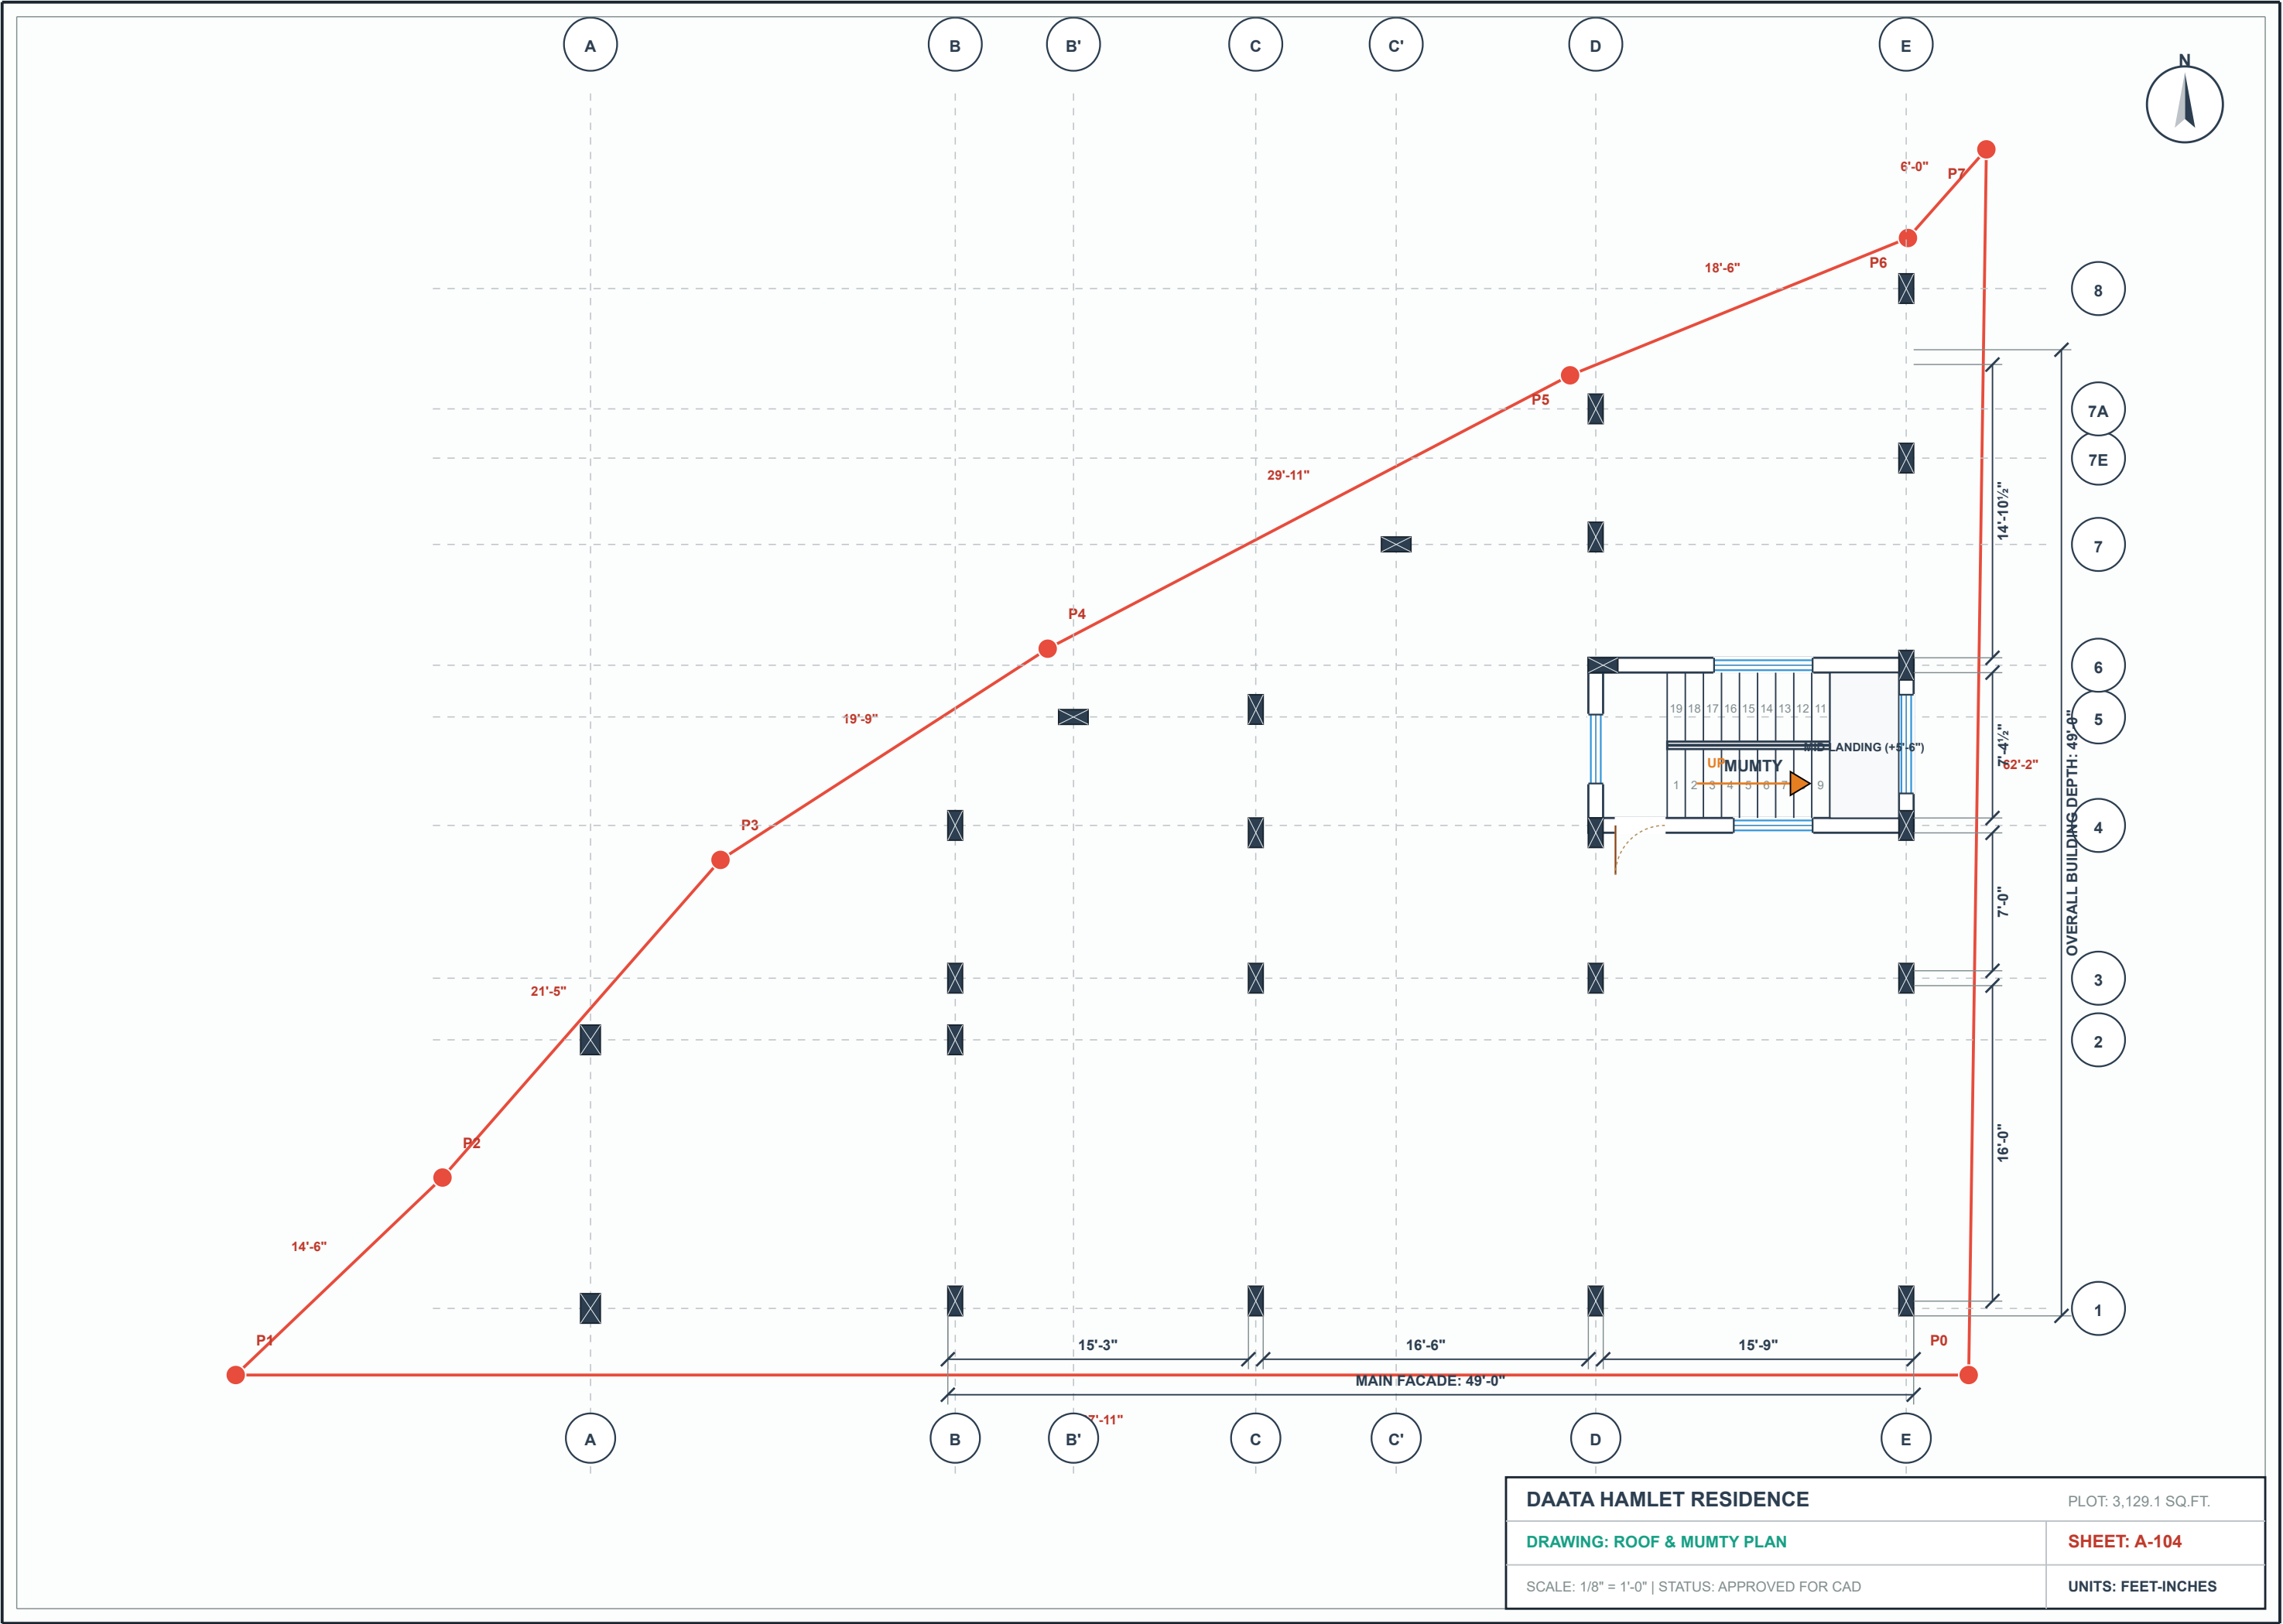

RCC COLUMN SCHEDULE (24 COLUMNS)			
MARK	SIZE (INCHES)	REBAR (MAIN)	EXTENT
C1 (A1-A2)	12" × 18"	8 × #6 (3/4")	GF → ROOF
C2 (B, C, D, E)	12" × 18"	6 × #6 (3/4")	GF → ROOF
C3 (MUMTY)	12" × 18"	6 × #6 (3/4")	GF → MUMTY
C4 (CHAMFER)	18"	6 × #6 (3/4")	GF → ROOF

- All 24 columns are parallel to each other.
- Concealed inside 9" walls without protrusions.
- Concrete: Class A (3,000 psi cylinder strength).
- Steel: Deformed Grade 60 (fy = 60,000 psi).

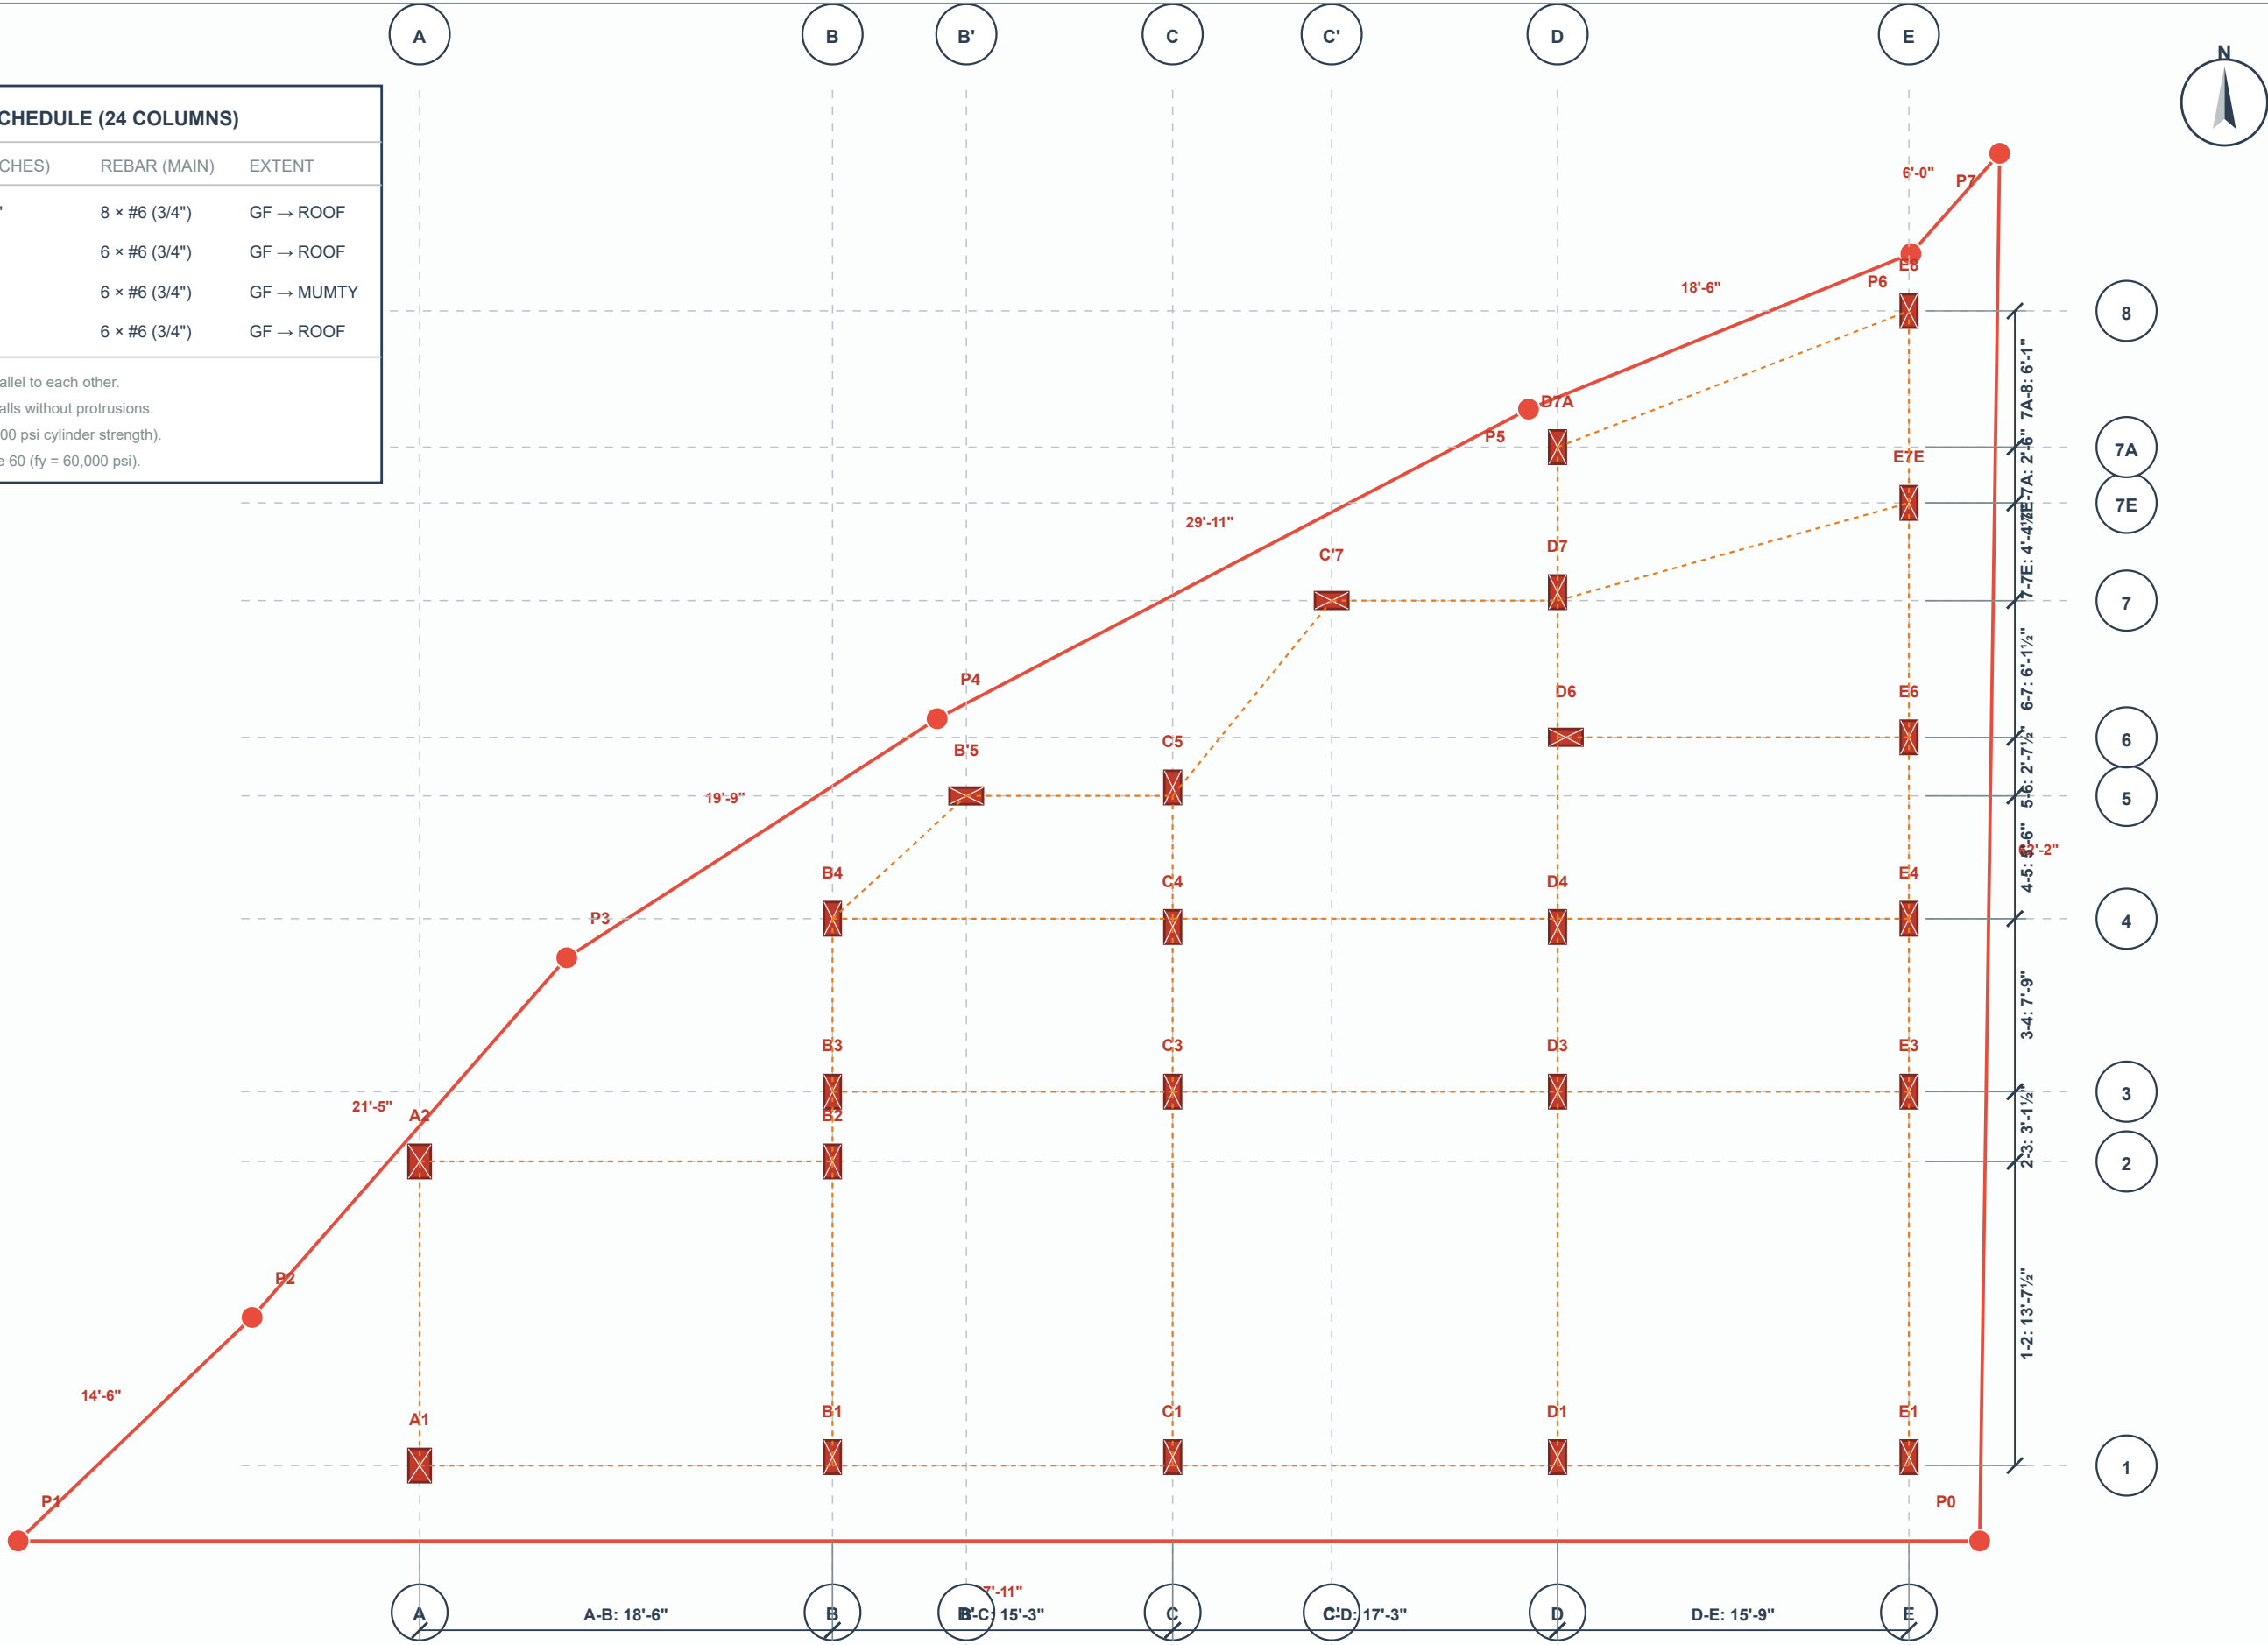

DAATA HAMLET RESIDENCE		PLOT: 3,129.1 SQ.FT.	
DRAWING: STRUCTURAL COLUMN & GRID LAYOUT		SHEET: S-101	
SCALE: 1/8" = 1'-0" STATUS: APPROVED FOR CAD		UNITS: FEET-INCHES	



