

DAATA HAMLET RESIDENCE

ARCHITECTURAL MASTER DRAWING SET • 3-STOREY CONTEMPORARY CANOPY VILLA

COVER • PROJECT SCHEDULE

SHEET S-001



PROJECT SCHEDULE & ARCHITECTURAL PARAMETERS

Client / Owner	Mr. Daata Hamlet
Project Location	Sector B, Phase 1, Daata Hamlet
Plot Frontage	87'-11" (26.80 m) Continuous Front Face
Plot Geometry	Trapezoidal: 87'-11" Front, Depth 62'-2" to 44'-8"
Total Plot Area	3,129.1 Sq.Ft (12.8 Marla / 290.7 Sq.M)
Total Covered Area	5,586.0 Sq.Ft (Across 3 Floors + Mumty Core)
Ground Floor Area	2,125.0 Sq.Ft (Drawing, 2 Beds, Lounge, 2 Kitchens)
First Floor Area	2,033.0 Sq.Ft (3 Master Suites, Lounge, Terrace)
Second Floor Area	1,282.0 Sq.Ft (2 Beds, Servant, Open Sun Terrace)
Mumty & Water Tank	146.0 Sq.Ft Landing (+42'-0" Height)
Structural Grid	22 Continuous Parallel RCC Columns (Flush in 9" Walls)
Ground Floor Living	Drawing Room (18'x16') • Bedrooms (15'x16')
Kitchen Strategy	Wide 15'x11' Main + 100 sft NE Apex Dirty Kitchen

MASTER DRAWING INDEX

Sheet	Drawing Title	Scale	Status
S-001	Cover • Project Parameters & Drawing Index	N.T.S.	Issued
A-101	Ground Floor Architectural Plan	1/4" = 1'-0"	Issued
A-102	First Floor Architectural Plan	1/4" = 1'-0"	Issued
A-103	Second Floor Architectural Plan	1/4" = 1'-0"	Issued
A-104	Roof & Mumty Architectural Plan	1/4" = 1'-0"	Issued
S-101	Structural Column Grid Layout (22 Continuous Columns)	1/4" = 1'-0"	Issued
A-201A	South Front Elevation (With Boundary Wall in Background)	1/4" = 1'-0"	Issued
A-201B	South Front Elevation (Pure Architecture / Open Setting)	1/4" = 1'-0"	Issued
A-301	Photorealistic 3D Perspectives & Visualizations	N.T.S.	Issued


Architectural Notes: All structural elements satisfy building bylaws. Continuous parallel 9"x18" reinforced concrete columns are concealed flush within 9" brick masonry walls. Finished floor levels: Plinth +1'-6", 1F +11'-10", 2F +22'-2", Roof +32'-6", Top of Mumty Core +42'-0".

DAATA HAMLET RESIDENCE

GROUND FLOOR ARCHITECTURAL PLAN • FFL +1'-6" • COVERED AREA: 2,125 SQ.FT

GROUND FLOOR PLAN

SHEET A-101

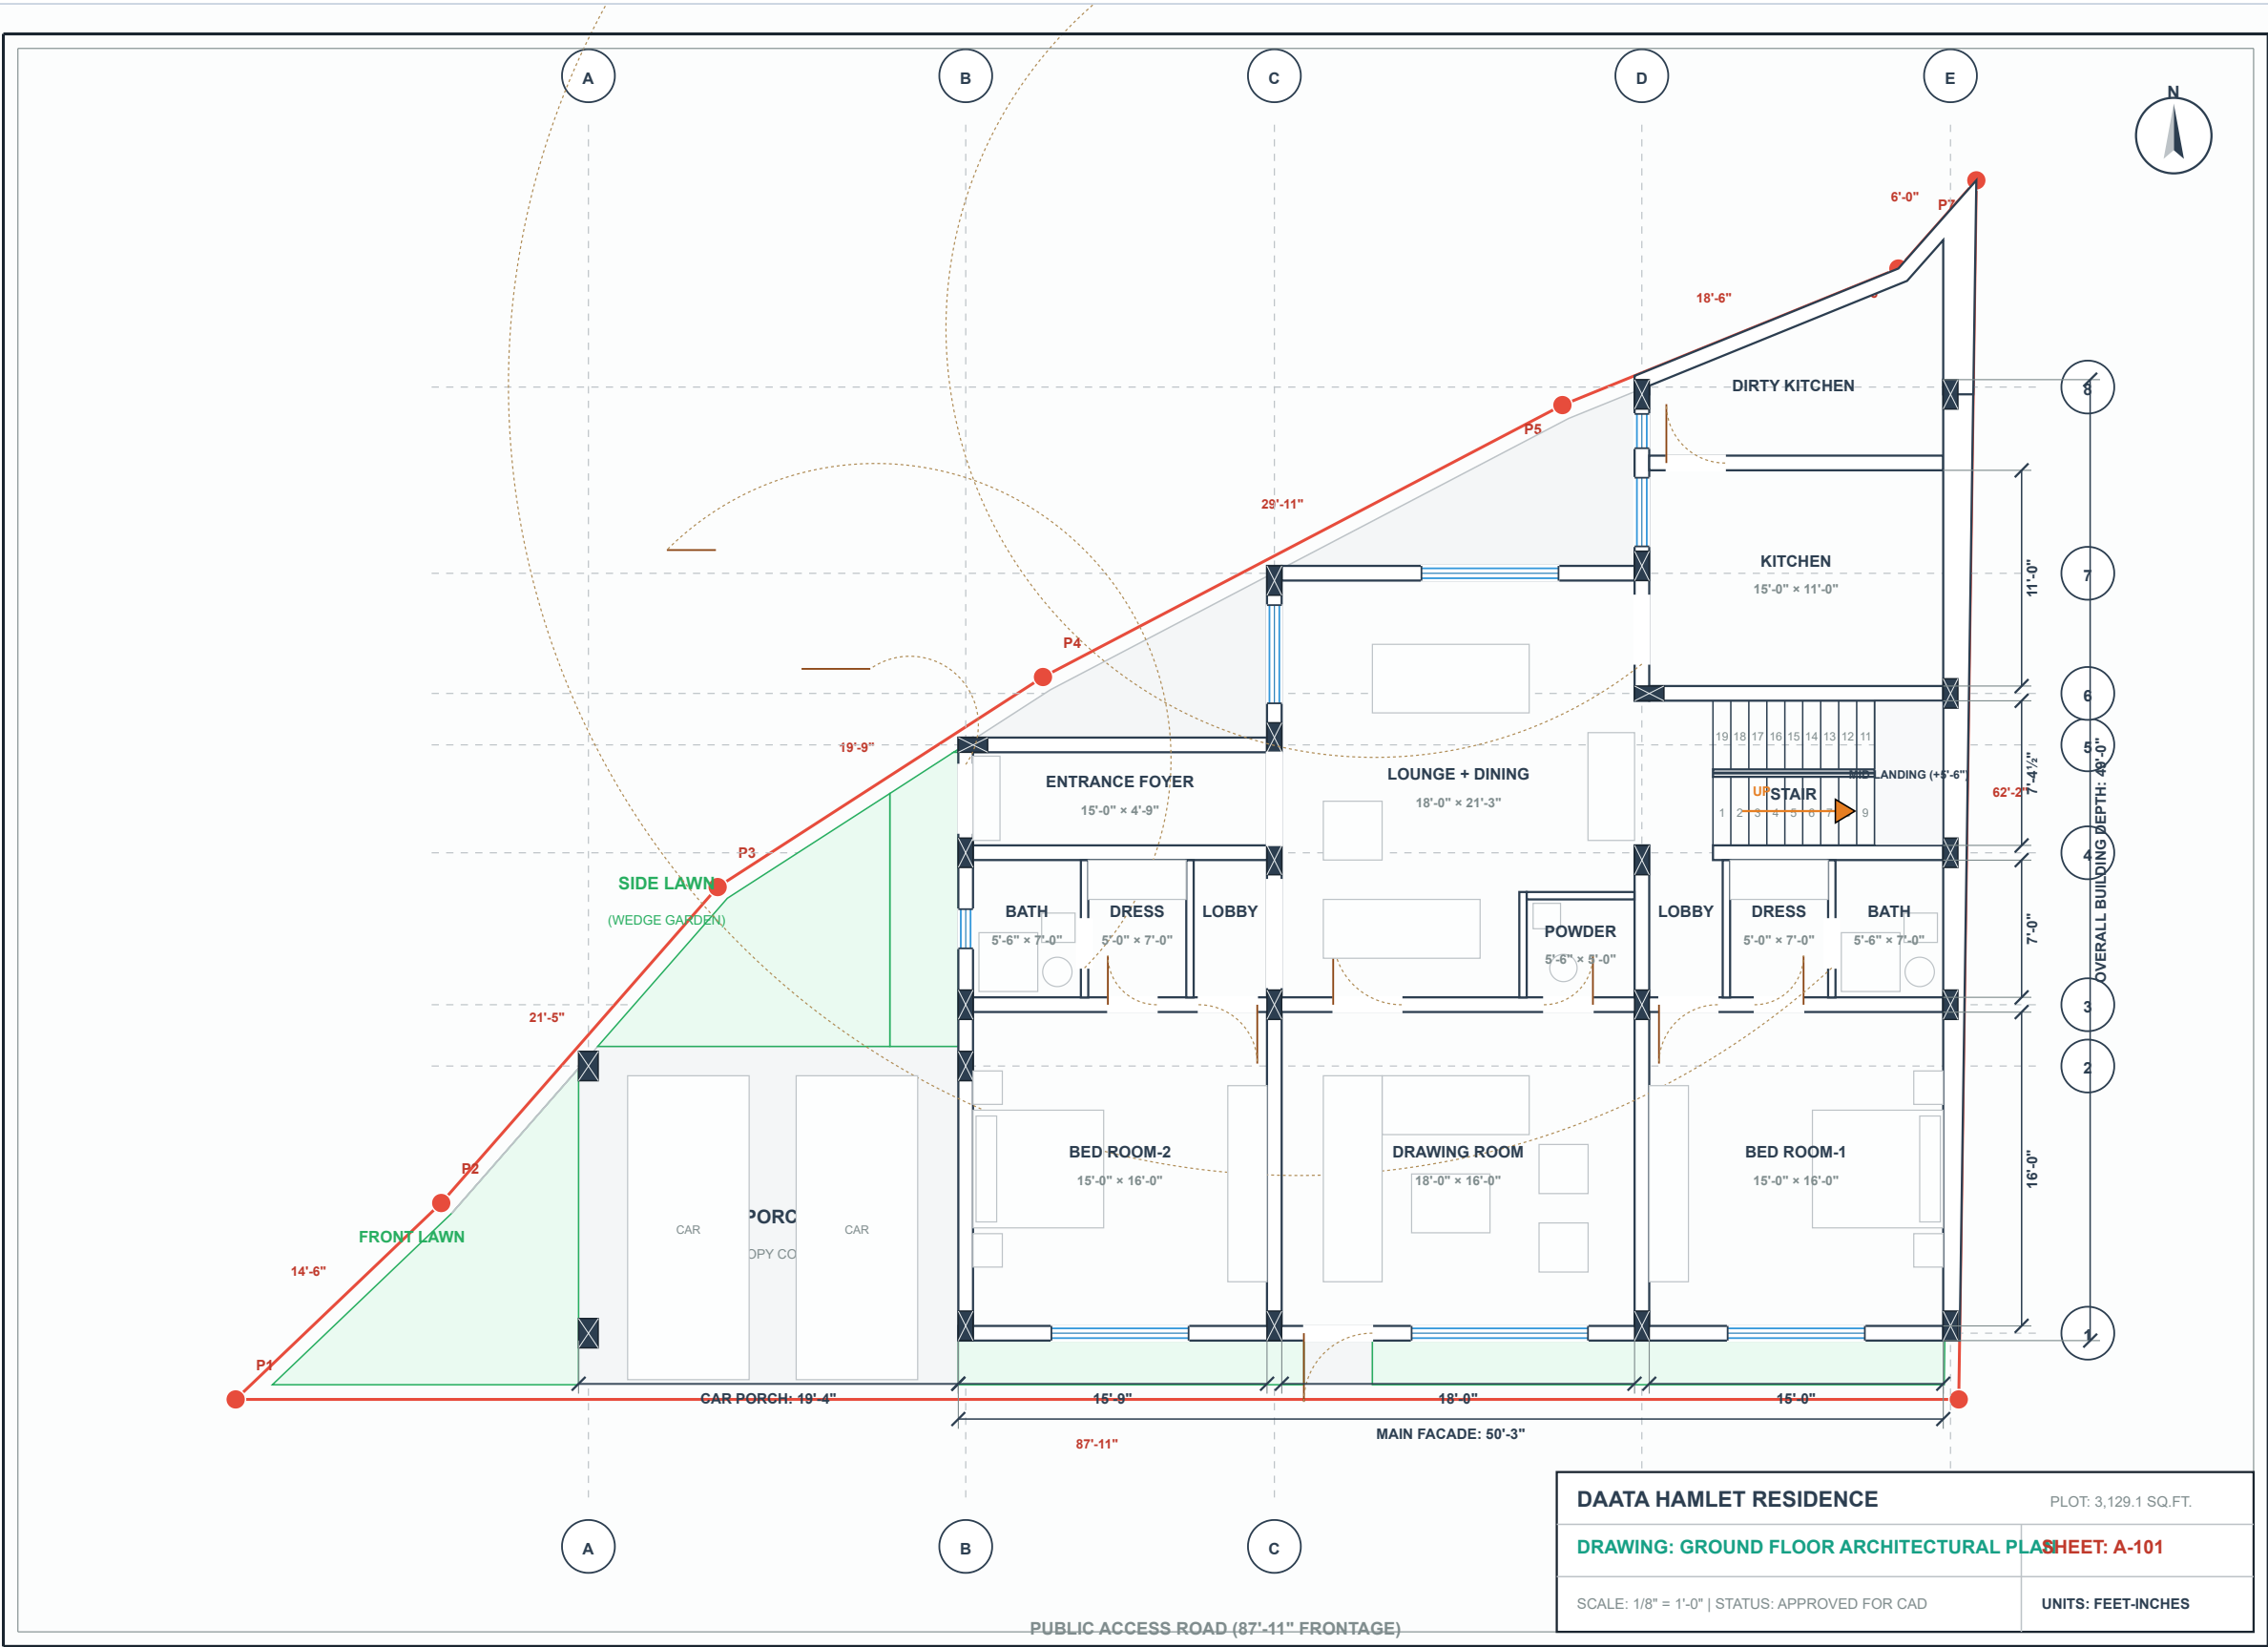

ACCOMMODATIONS

Drawing Room (18'x16'), 2 Master Beds (15'x16'), Lounge (25'x16'), Main & Dirty Kitchen, 2-Car Porch

DIRTY KITCHEN FEATURE

Custom 100 sft Tucked in NE Diagonal Apex (P5-P6-P7)

STATUS

ISSUED FOR TENDER

SCALE

1/4" = 1'-0" (1:50)

DRAWING SHEET


A-101

DAATA HAMLET RESIDENCE

FIRST FLOOR ARCHITECTURAL PLAN • FFL +11'-10" • COVERED AREA: 2,033 SQ.FT

FIRST FLOOR PLAN

SHEET A-102

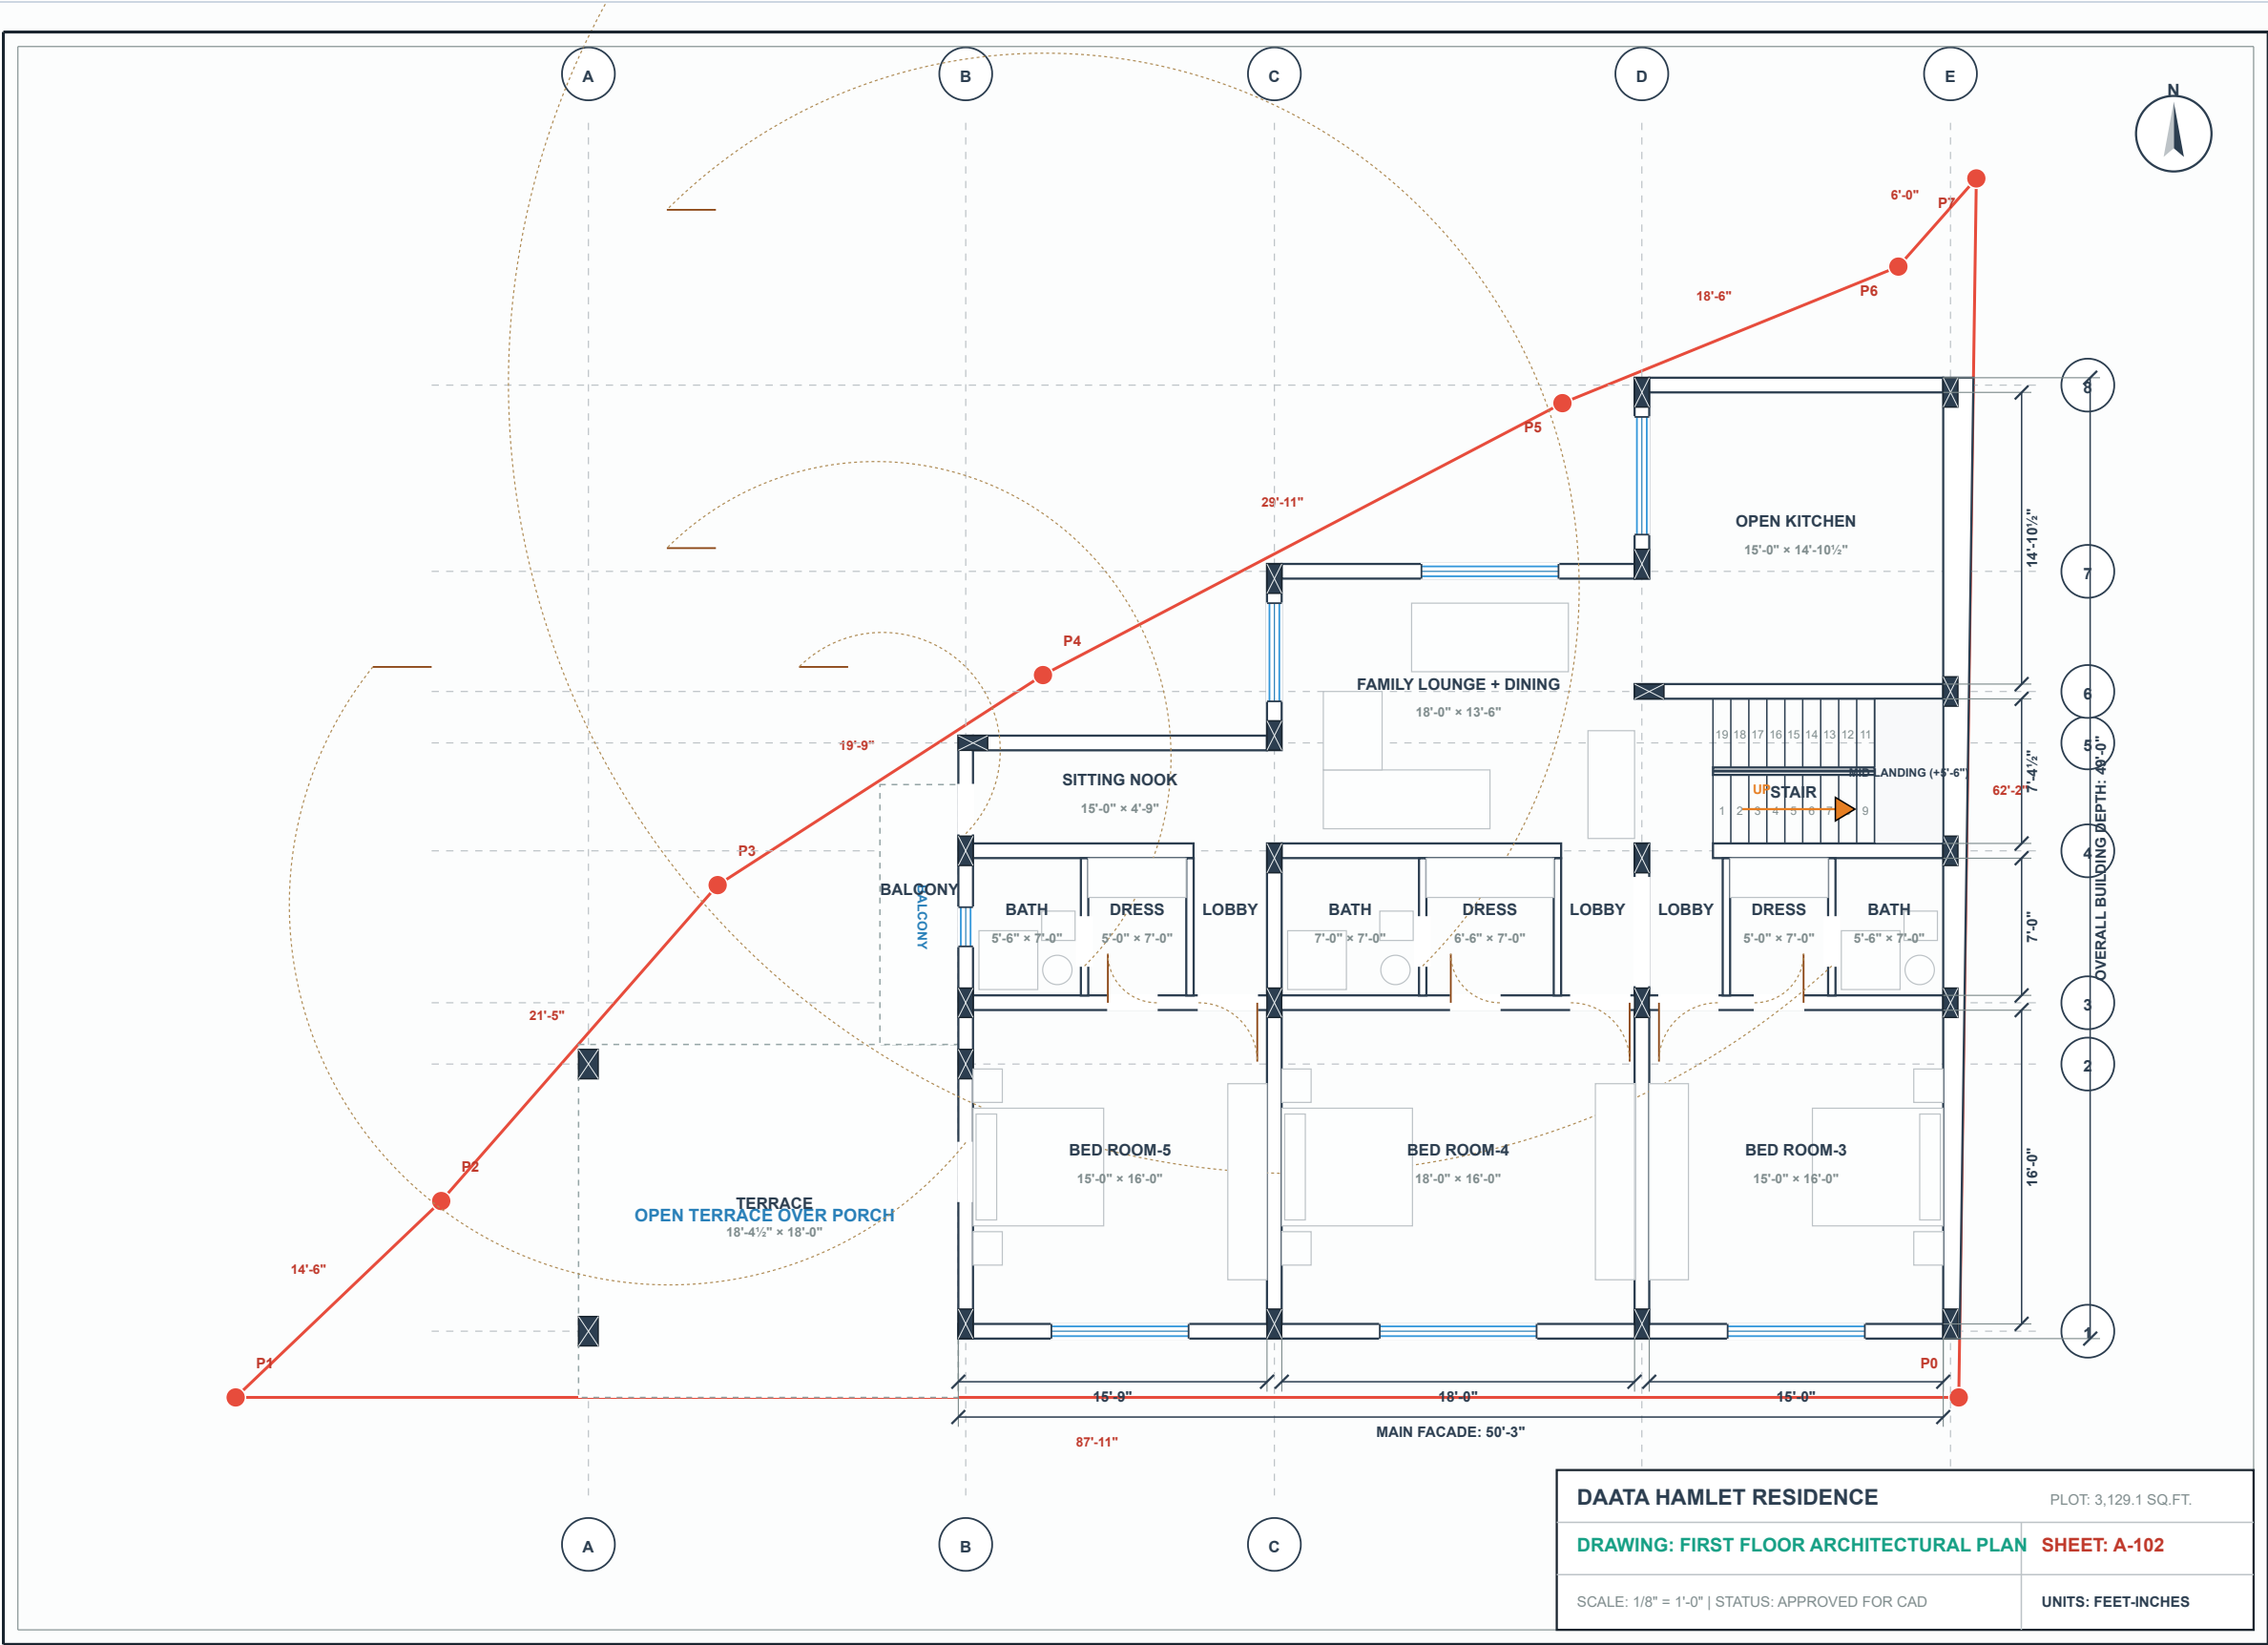

ACCOMMODATIONS

3 Master Suites (Beds 3, 4, 5 ≥ 15'x16'), Family Lounge (25'x16'), Open Kitchen, Porch Canopy Terrace

OUTDOOR TERRACES

Front Porch Canopy Terrace (346.5 sft) + West Balcony

STATUS

ISSUED FOR TENDER

SCALE

1/4" = 1'-0" (1:50)

DRAWING SHEET


A-102

DAATA HAMLET RESIDENCE

SECOND FLOOR ARCHITECTURAL PLAN • FFL +22'-2" • COVERED AREA: 1,282 SQ.FT

SECOND FLOOR PLAN

SHEET A-103

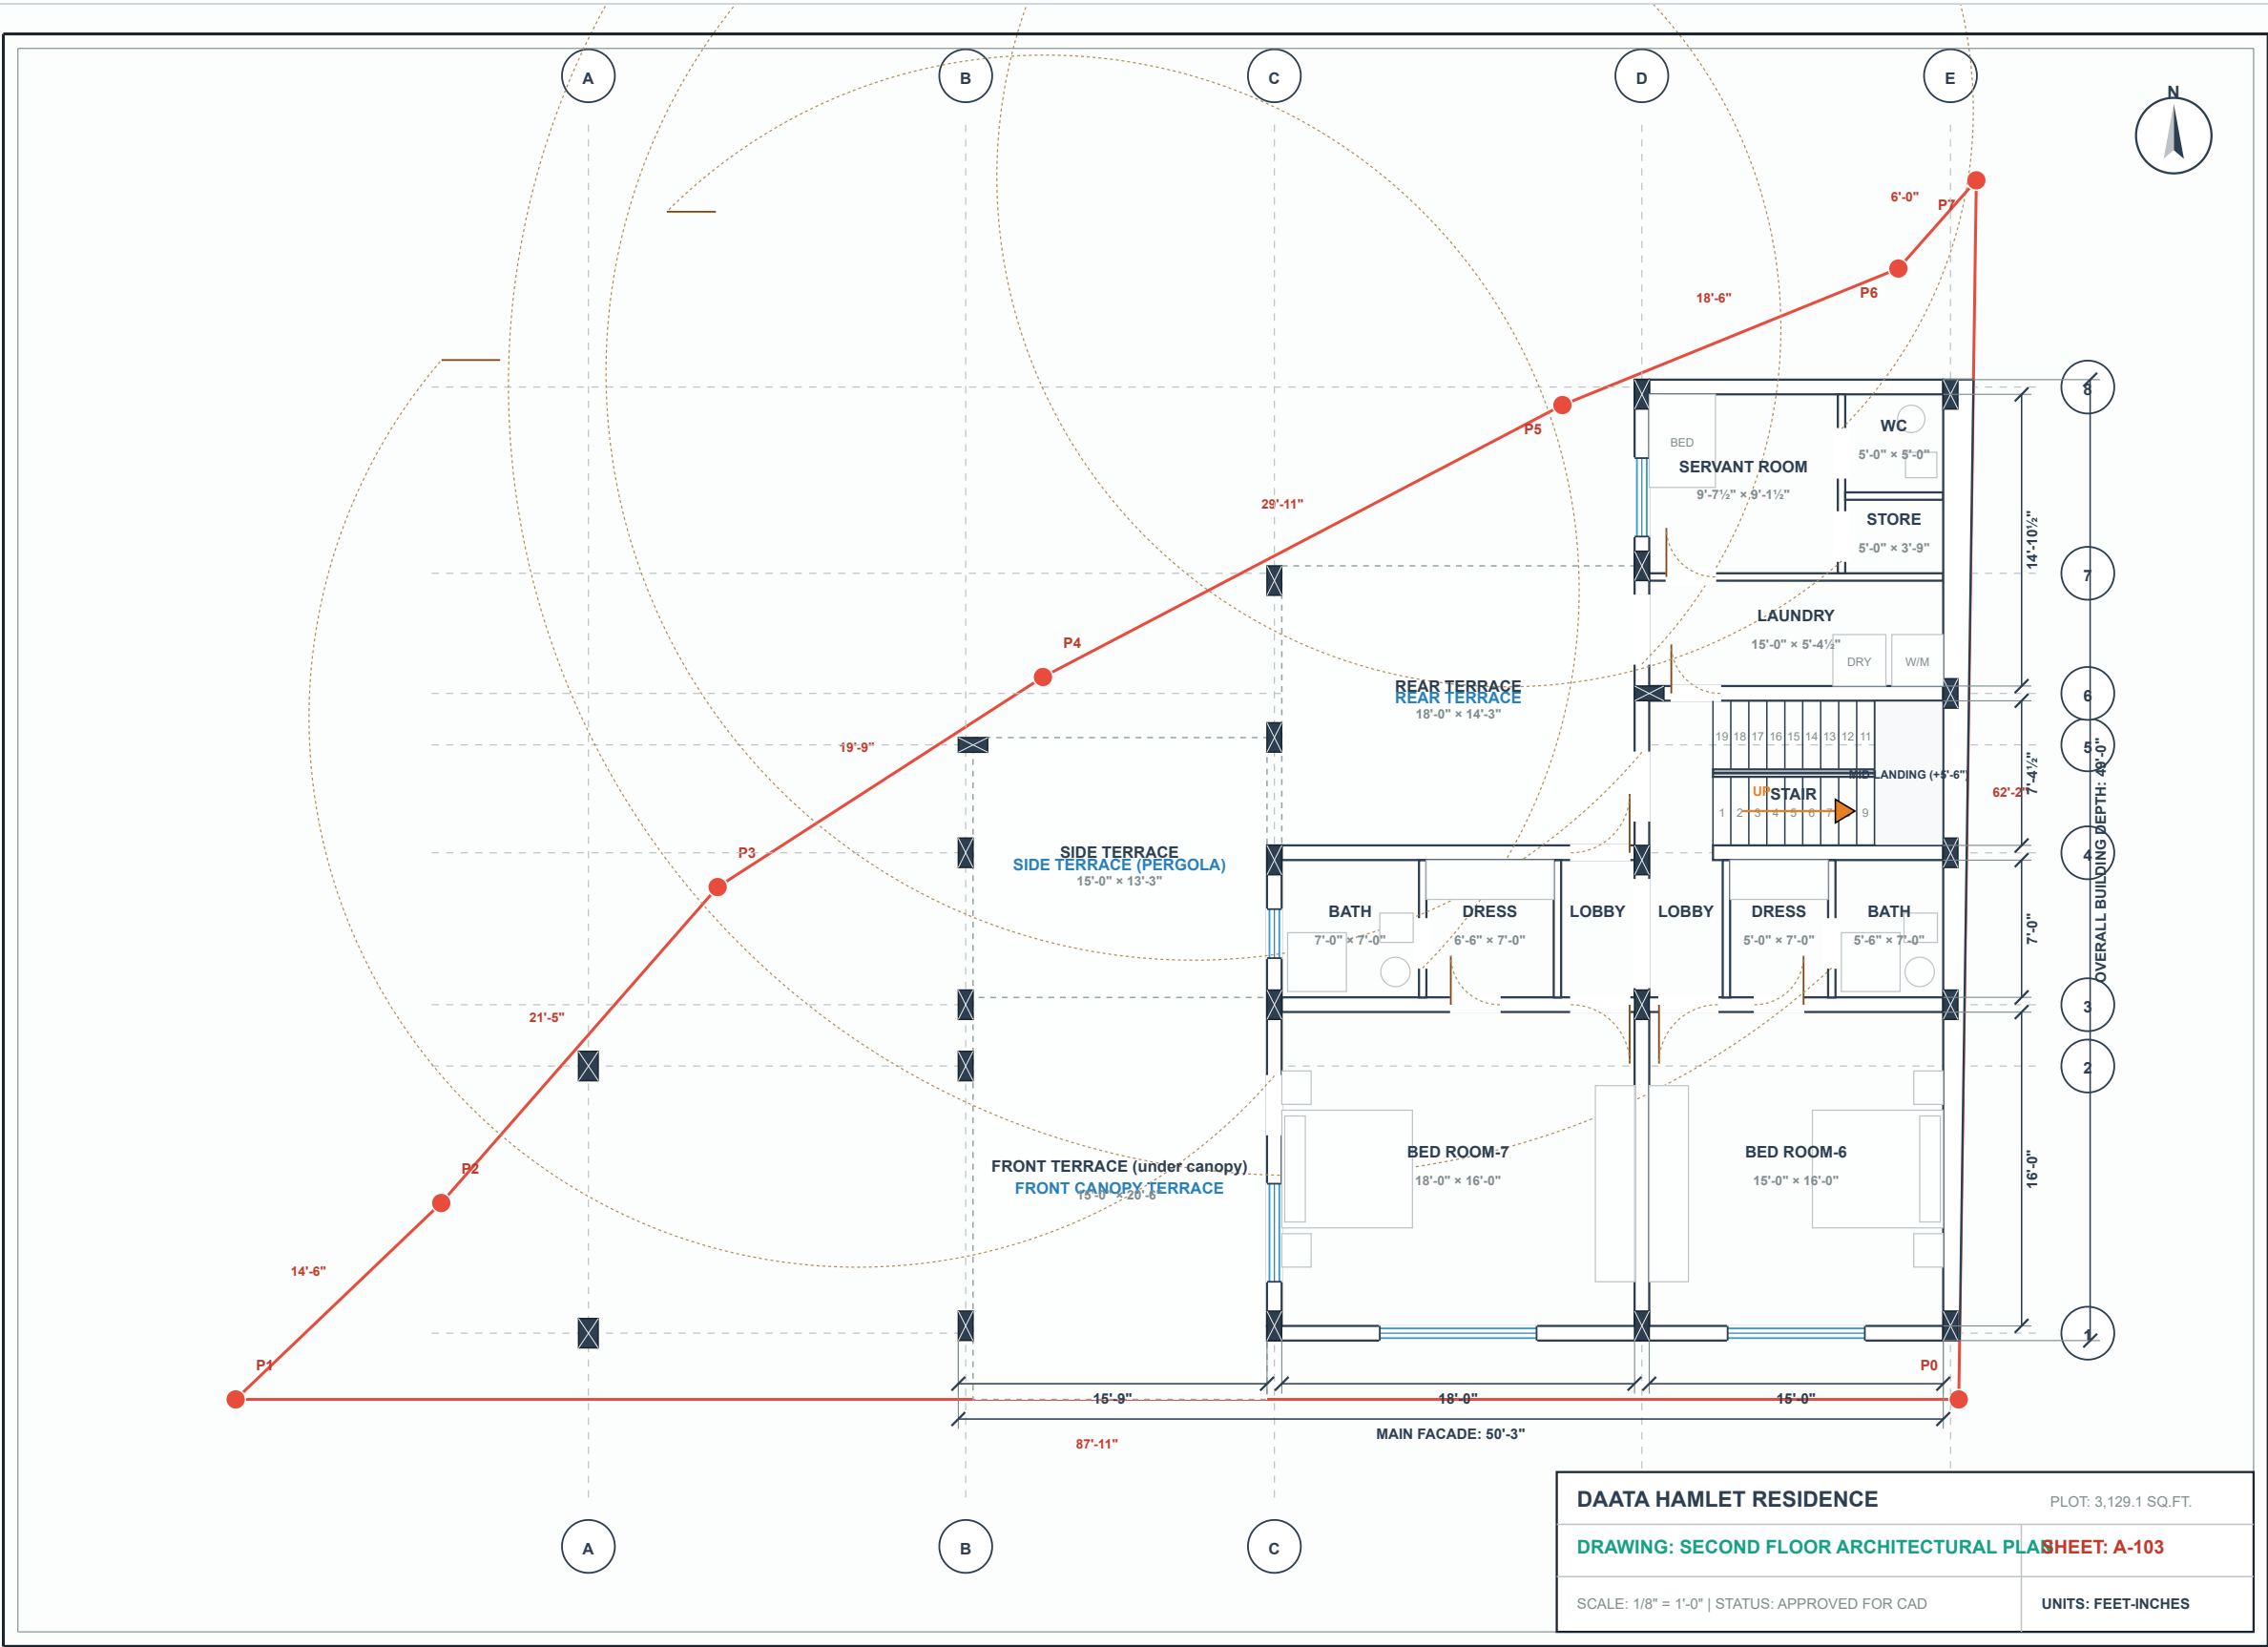

ACCOMMODATIONS

2 Master Suites (Beds 6, 7), Servant Room & Bath (10'x8'), Laundry & Store, Open Sun Terrace

TERRACES

Open-to-Sky Front Sun Terrace (307.5 sft) with Glass Balustrade

STATUS

ISSUED FOR TENDER

SCALE

1/4" = 1'-0" (1:50)

DRAWING SHEET

A-103



ELEMENTS

Stair Mumty Landing, 800-Gallon Water Tank Housing, Roof Terrace (1,850 sft Solar Zone)

PARAPET & DRAINAGE

3'-0" Solid Parapet Walls, 1:60 Waterproof Slope screed

STATUS

ISSUED FOR TENDER

SCALE

1/4" = 1'-0" (1:50)

DRAWING SHEET

A-104

 Structural Column Grid Layout

STRUCTURAL SYSTEM

22 Continuous 9"x18" RCC Columns running Ground -> First -> Second -> Mumty

CONCEALMENT DETAILS

100% Flush Concealed inside 9" Masonry Walls
(Zero Protrusion)

STATUS

STRUCTURAL APPROVED

SCALE

1/4" = 1'-0" (1:50)

DRAWING SHEET

S-101

DAATA HAMLET RESIDENCE

SOUTH FRONT ELEVATION • WITH BOUNDARY WALL (BACKGROUND OF LAWN & CAR PORCH ONLY)

FRONT ELEVATION • WITH WALL

SHEET A-201A



KEY ARCHITECTURE

Open 2F Sun Terrace, Rising Mumty Tower (+42'-0"), Separate Drawing (7'x6') & Lounge/Bed Windows

PORCH & BALUSTRADES

2 Rear-Facing Cars in Porch, Dual 1F/2F 12mm Frameless Glass Railings

STATUS

WORKING ELEVATION

SCALE

1/4" = 1'-0" (1:50)

DRAWING SHEET

A-201A

DAATA HAMLET RESIDENCE

SOUTH FRONT ELEVATION • PURE ARCHITECTURAL CANOPY ELEVATION (WITHOUT BOUNDARY WALL)

FRONT ELEVATION • OPEN

SHEET A-201B



ELEVATION FEATURES

Unobstructed Floating Cantilevered Canopies, Stepped Silhouette, Travertine Cladding

MATERIALS

Charcoal Bronze Fascias, Natural Teak Soffits, 12mm Tempered Glass

STATUS

PRESENTATION DRAWING

SCALE

1/4" = 1'-0" (1:50)

DRAWING SHEET

A-201B

DAATA HAMLET RESIDENCE

3D ARCHITECTURAL VISUALIZATIONS • BLENDER 5.1 CYCLES PHOTOREALISTIC RENDERS

3D PERSPECTIVES

SHEET A-301

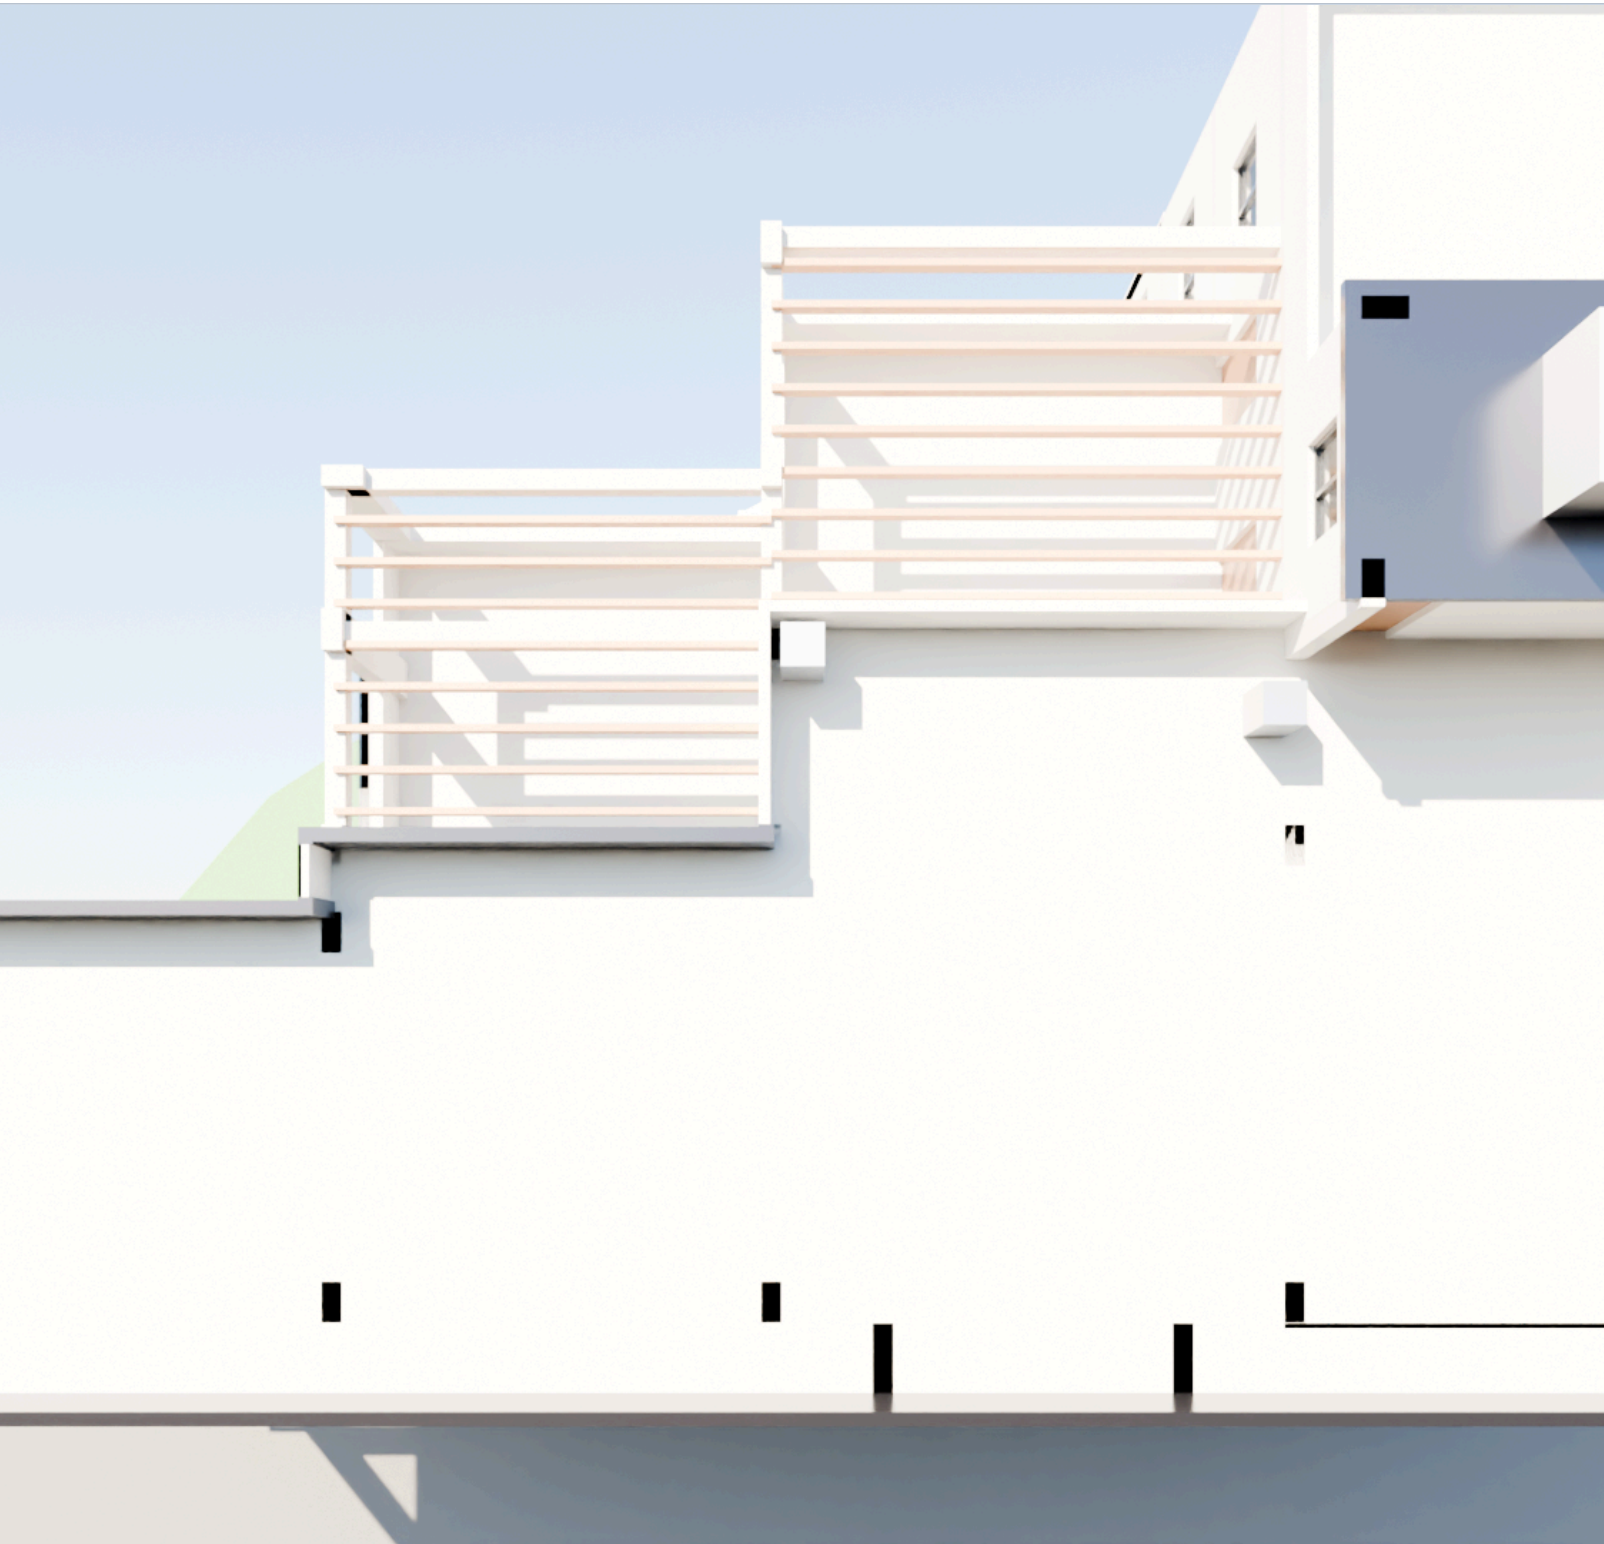


FIG 1: SIGNATURE CANOPY FRONT SOUTH ELEVATION PERSPECTIVE

4:30 PM GOLDEN HOUR LIGHTING

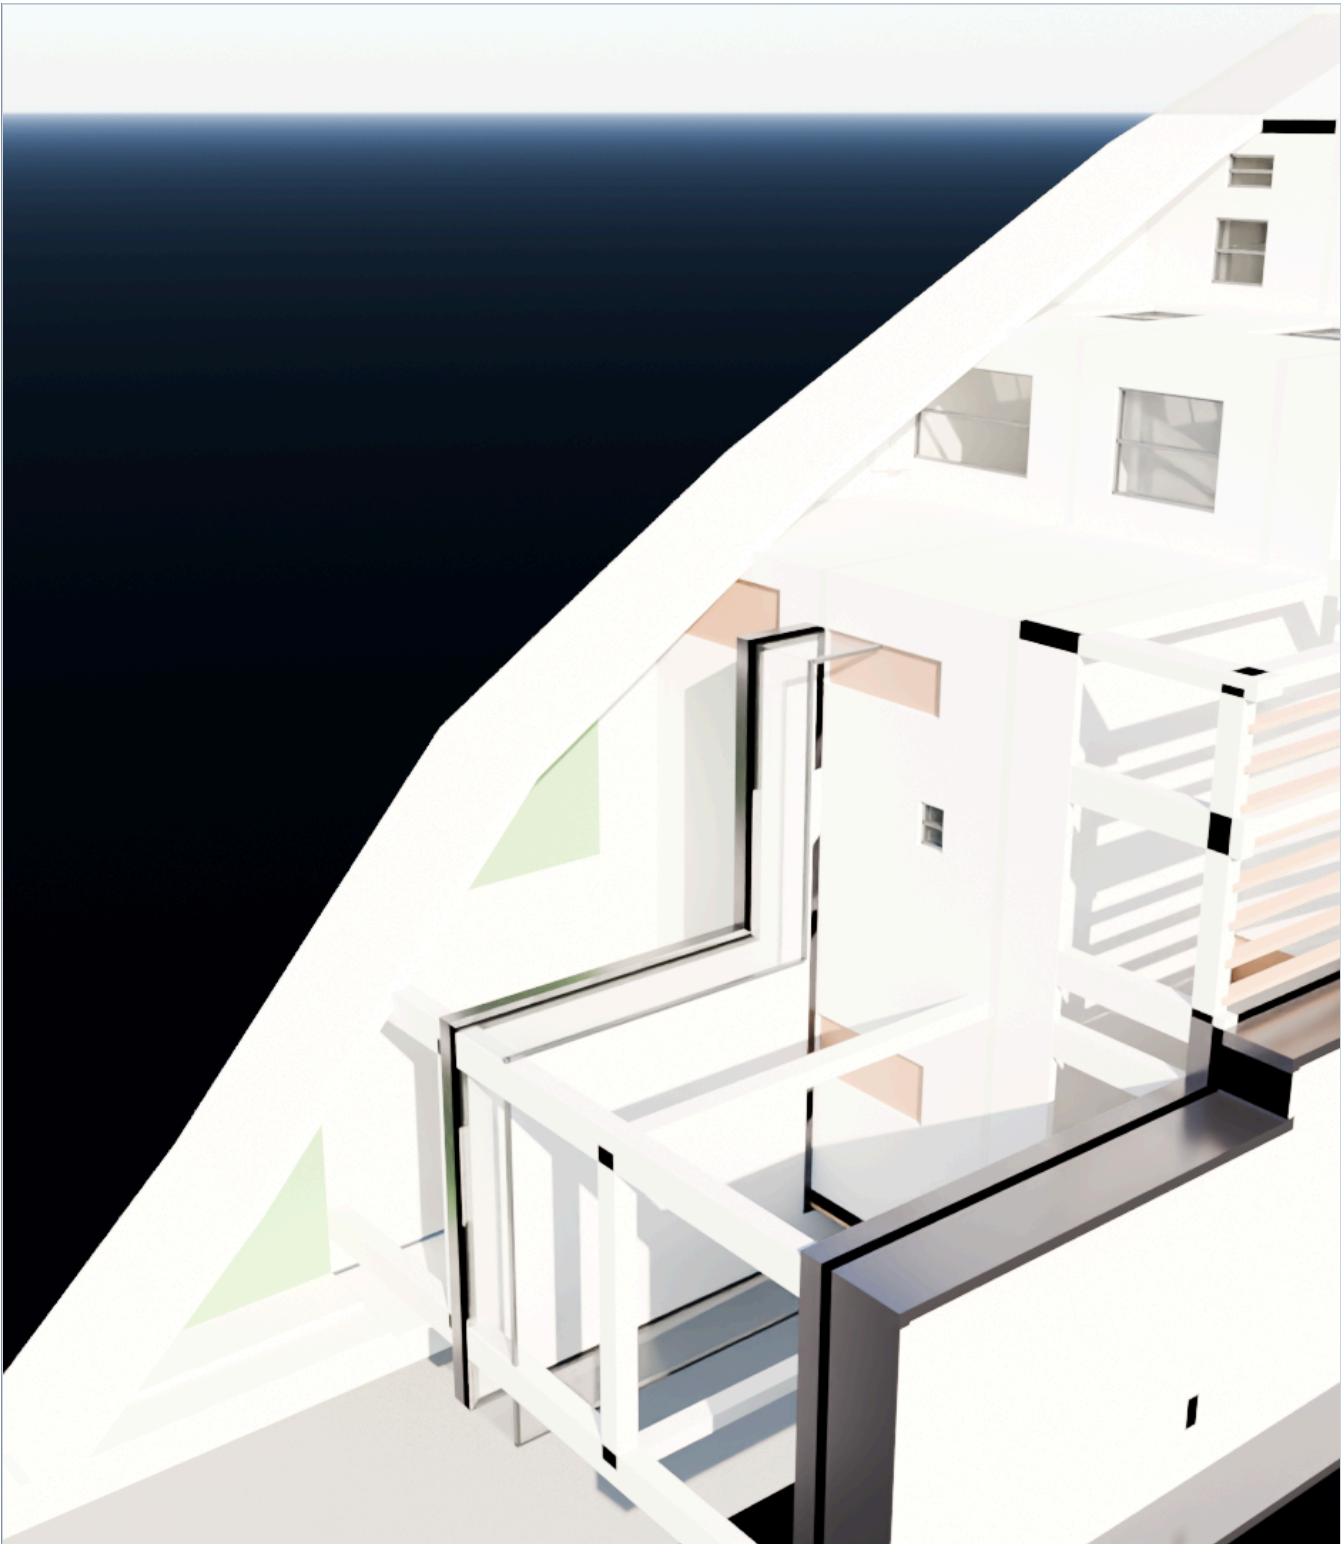


FIG 2: BIRD'S EYE 3/4 AERIAL PERSPECTIVE

SITE CONTAINMENT • ROOF CANOPY • NE APEX KITCHEN